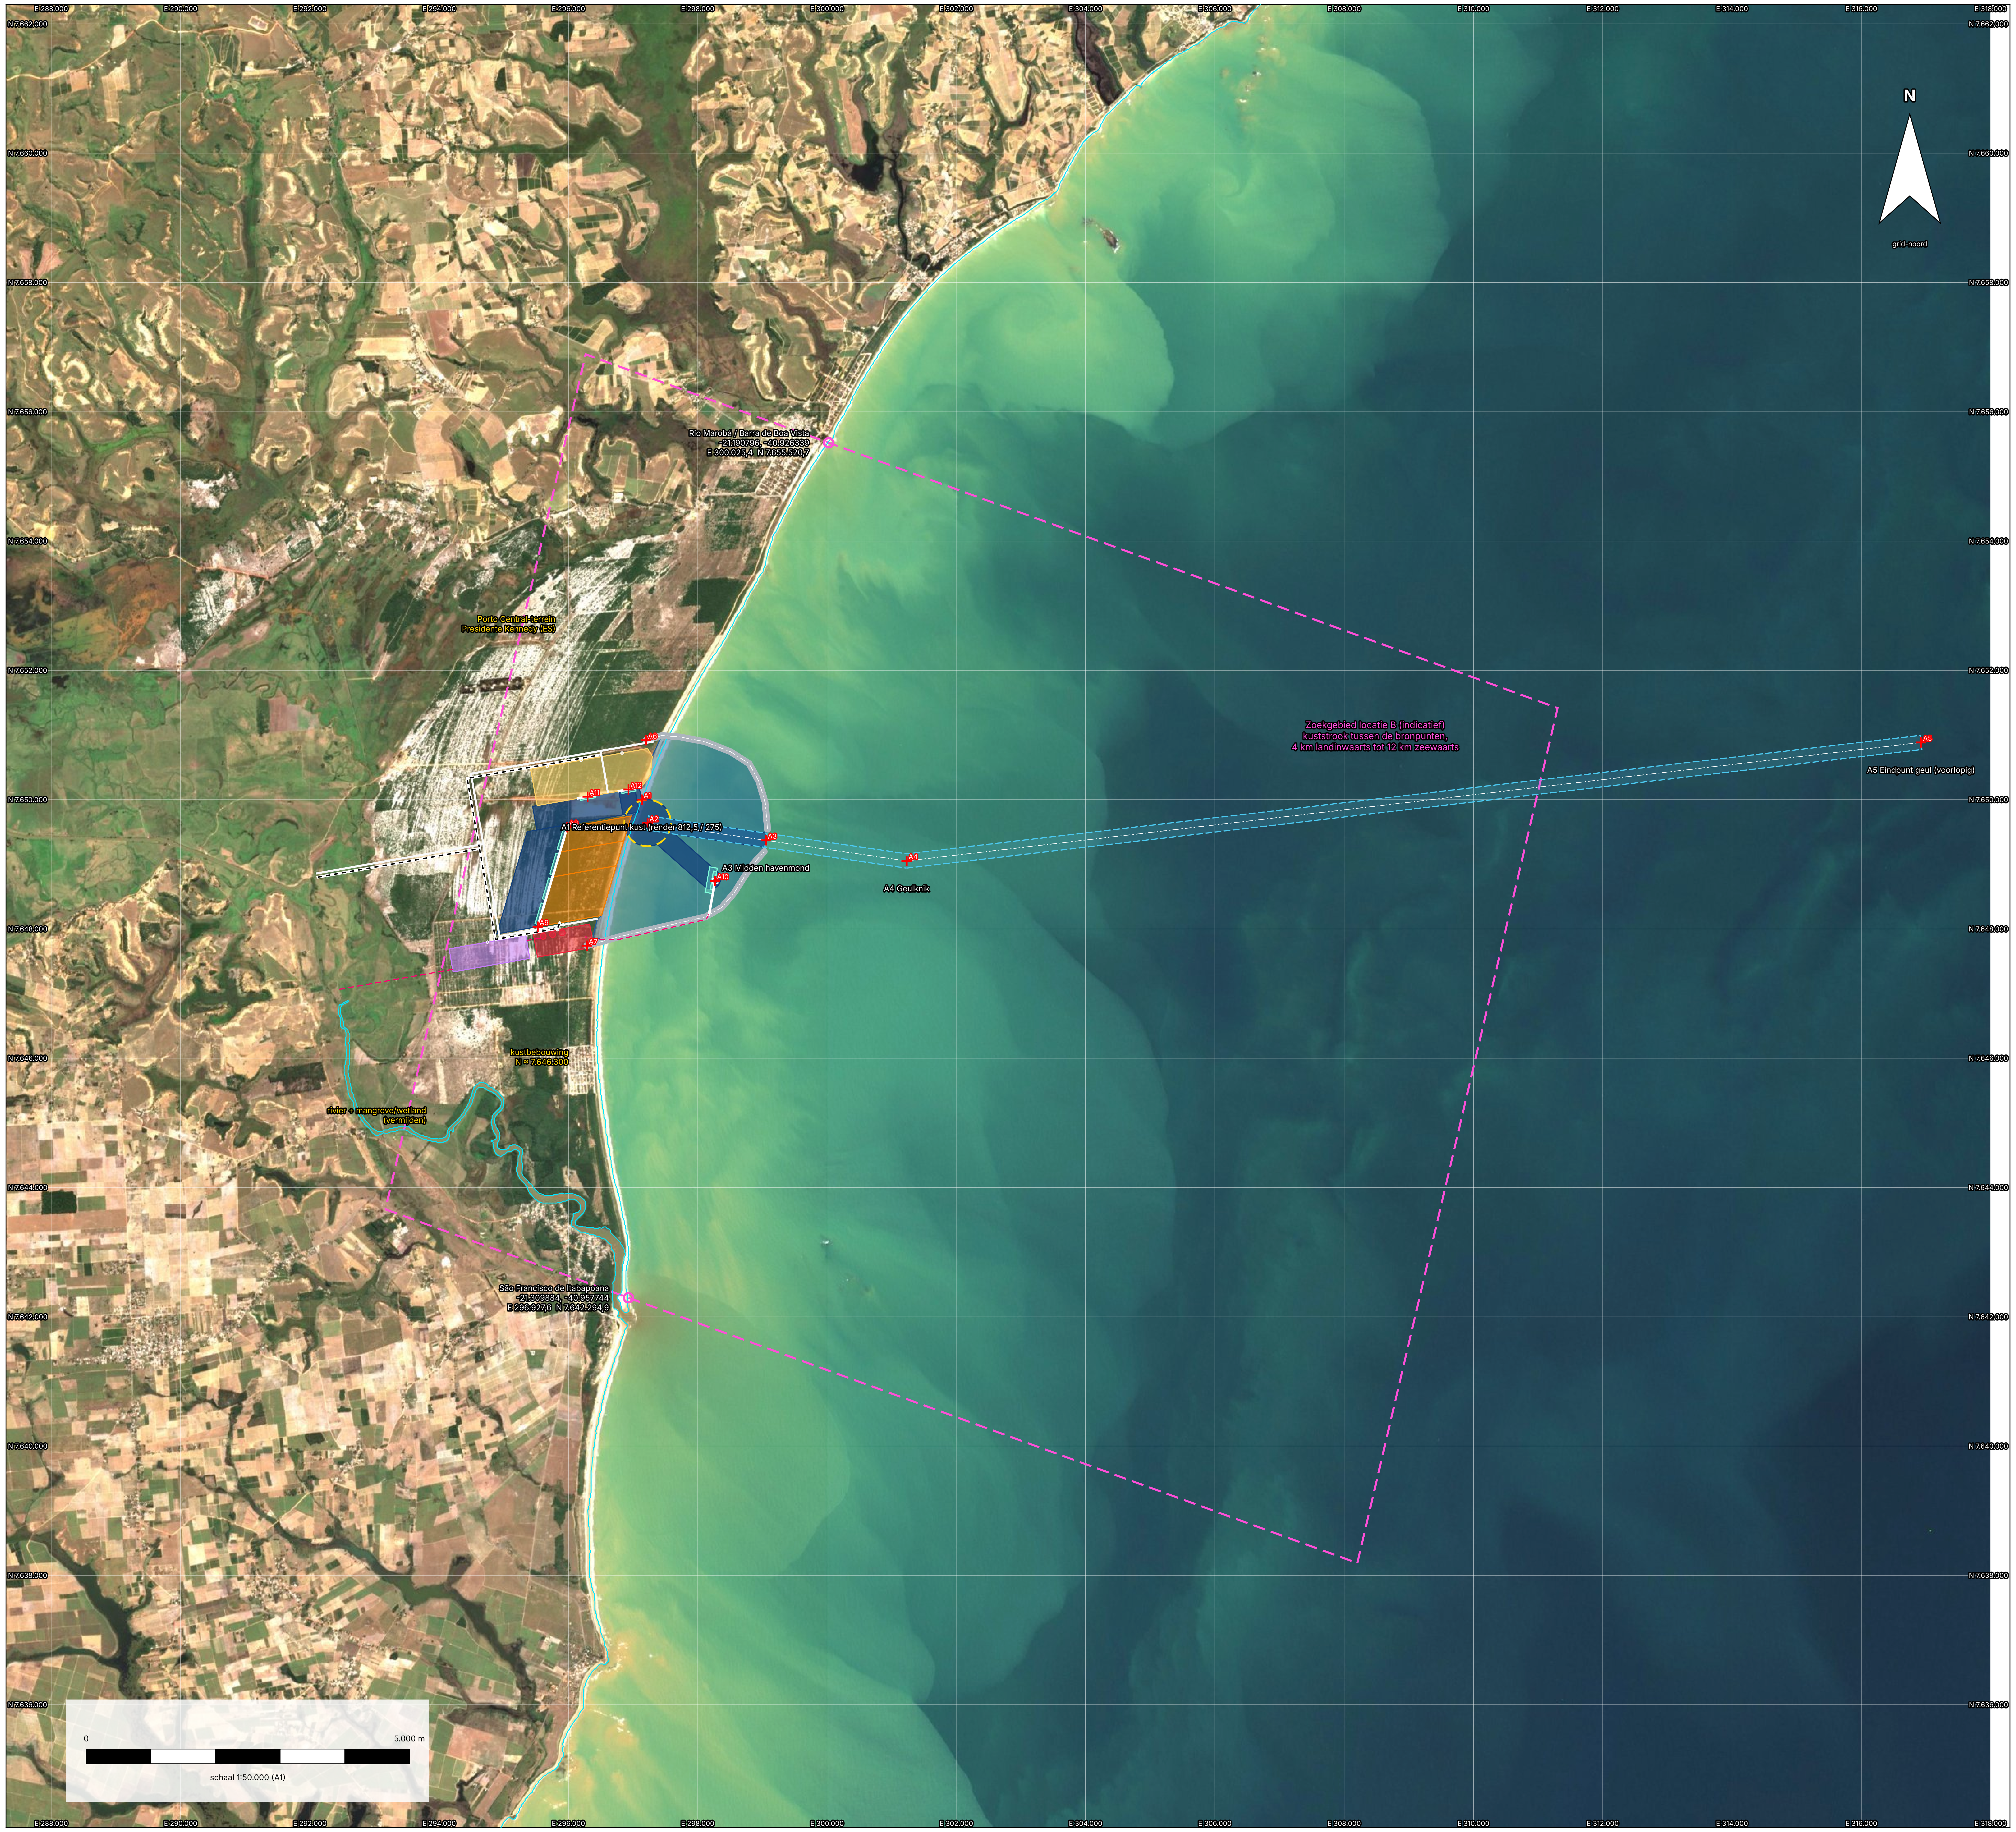

LEGENDA

━	Waterlijn 3-7-2026 (NDWI, geen MLWS-lijn)
╌	Zoekgebied locatie B (indicatief)
■	Voorhaven binnen de dammen (strandwal ontgraven)
■	Gebaggerd tot -18,20 m MLWS (voorlopig)
⬚	Geul 220 m bodembreedte
⬚	Vrije draaikom D = 720 m
⬚	Havenmond vrij 350 m
■	Golfbreker (footprint 90 m, voorlopig)
	Kade / steiger
■	Scheepsenveloppe aan ligplaats
■	Containerterminal
■	Graanterminal
■	LNG-steiger, tanks en hervergassing
■	Centrale + utilities (reservering)
━	Hoofdweg + terminalinritten
╌	Spoor
╌	LNG/gasleiding, koelwater (indicatief)
+	Ontwerpankerpunt (E/N in maatstaat)

Havenligging (vastgesteld)
Porto Central, Presidente Kennedy - ES, 29350-000
Havenas haaks op de kust: azimut 110 gr (kust 20.1 gr).
A1 kustpunt: E 297.135,0 N 7.650.000,0
= -21.240329, -40.954826 (WGS84)
Havenas door het bouwterrein fase 1 aan het strand
(lichte rechthoek op de luchtfoto 03-07-2026);
bekkens landinwaarts op het kale Porto Central-terrein.

Georeferentiecontrole
GSHHS-kust vs. S2-waterlijn: gem. 14 m, sd 66 m
(15 profielen, N 7.642-7.656 km)
Bekende afstand bronpunten: 13.582,4 m geodetisch,
13.583,8 m in grid (k = 1.00010)
Noordrichting: convergentie 0.70 gr

Vormreferentie: Porto Central masterplan 2016, p. 9 (ANTT)

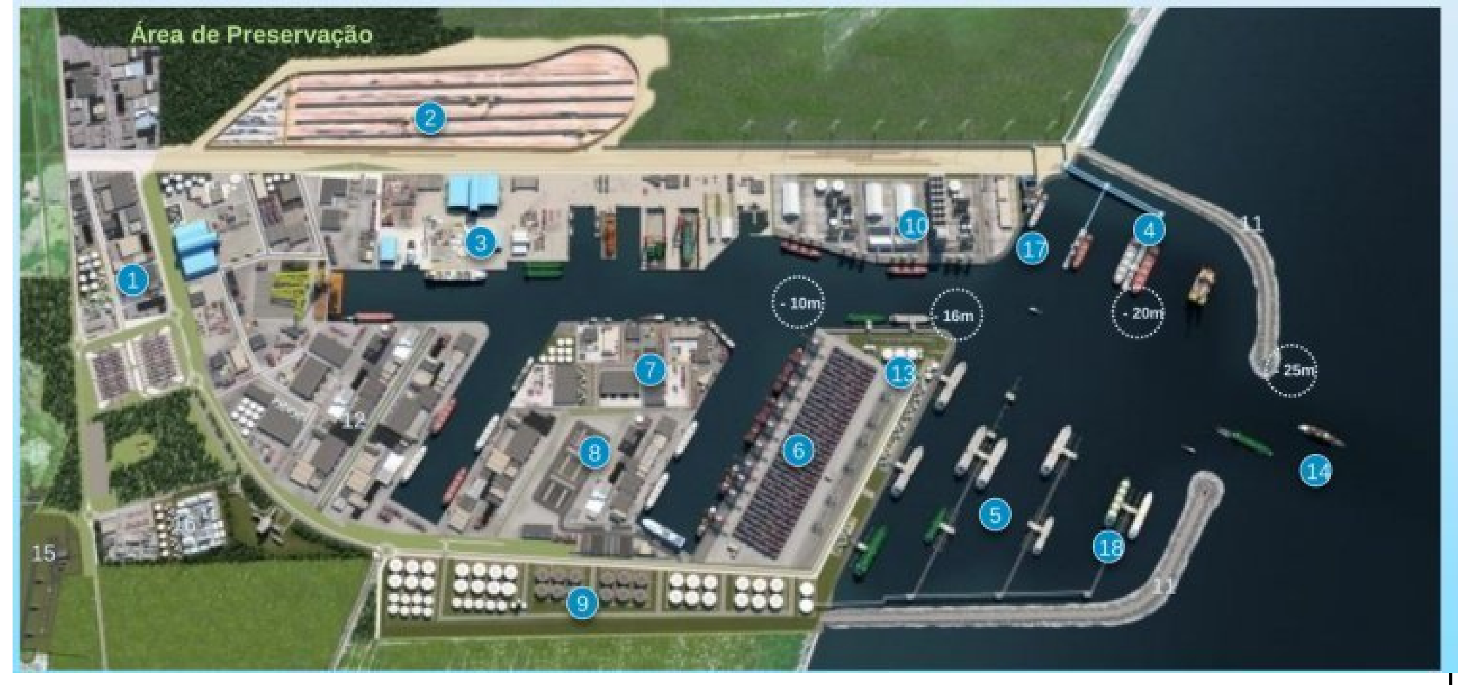

Overgenomen: 11/14 dammen en ingang | 6 containervingers | 10 graan (+ RoRo) | 9 tankpark
(LNG + centrale) | 18 LNG-steiger. Weggelaten (niet in opdracht): 2, 3, 5, 7/8, 12, 1

Project	Havenontwerp Porto Central, Presidente Kennedy (ES) - Groep 1
Module	Atelier De Haven A | NHL Stenden Civiele Techniek
Bladnaam	**Overzicht zoekgebied en havenligging**
Status	**SCHETSONTWERP (SO)**
Blad / versie	SO-01 | versie 3.0 | 22-10-2026
Schaal	1:50.000 op A1 (841 × 594 mm)
Stelsel	SIRGAS 2000 / UTM zone 24S EPSG:31984 eenheid m
Hoogtedatum	diepten in m t.o.v. MLWS, voorlopig; MLWS-DHN te verifiëren
Kaartbron	Copernicus Sentinel-2 L2A (ESA), 03-07-2026, 10 m
	tegels 24KTB/24KUB, AWS Open Data COG; geraadpleegd 22-10-2026
Kustlijn	waterlijn 03-07-2026 uit NDWI (geen MLWS-lijn)

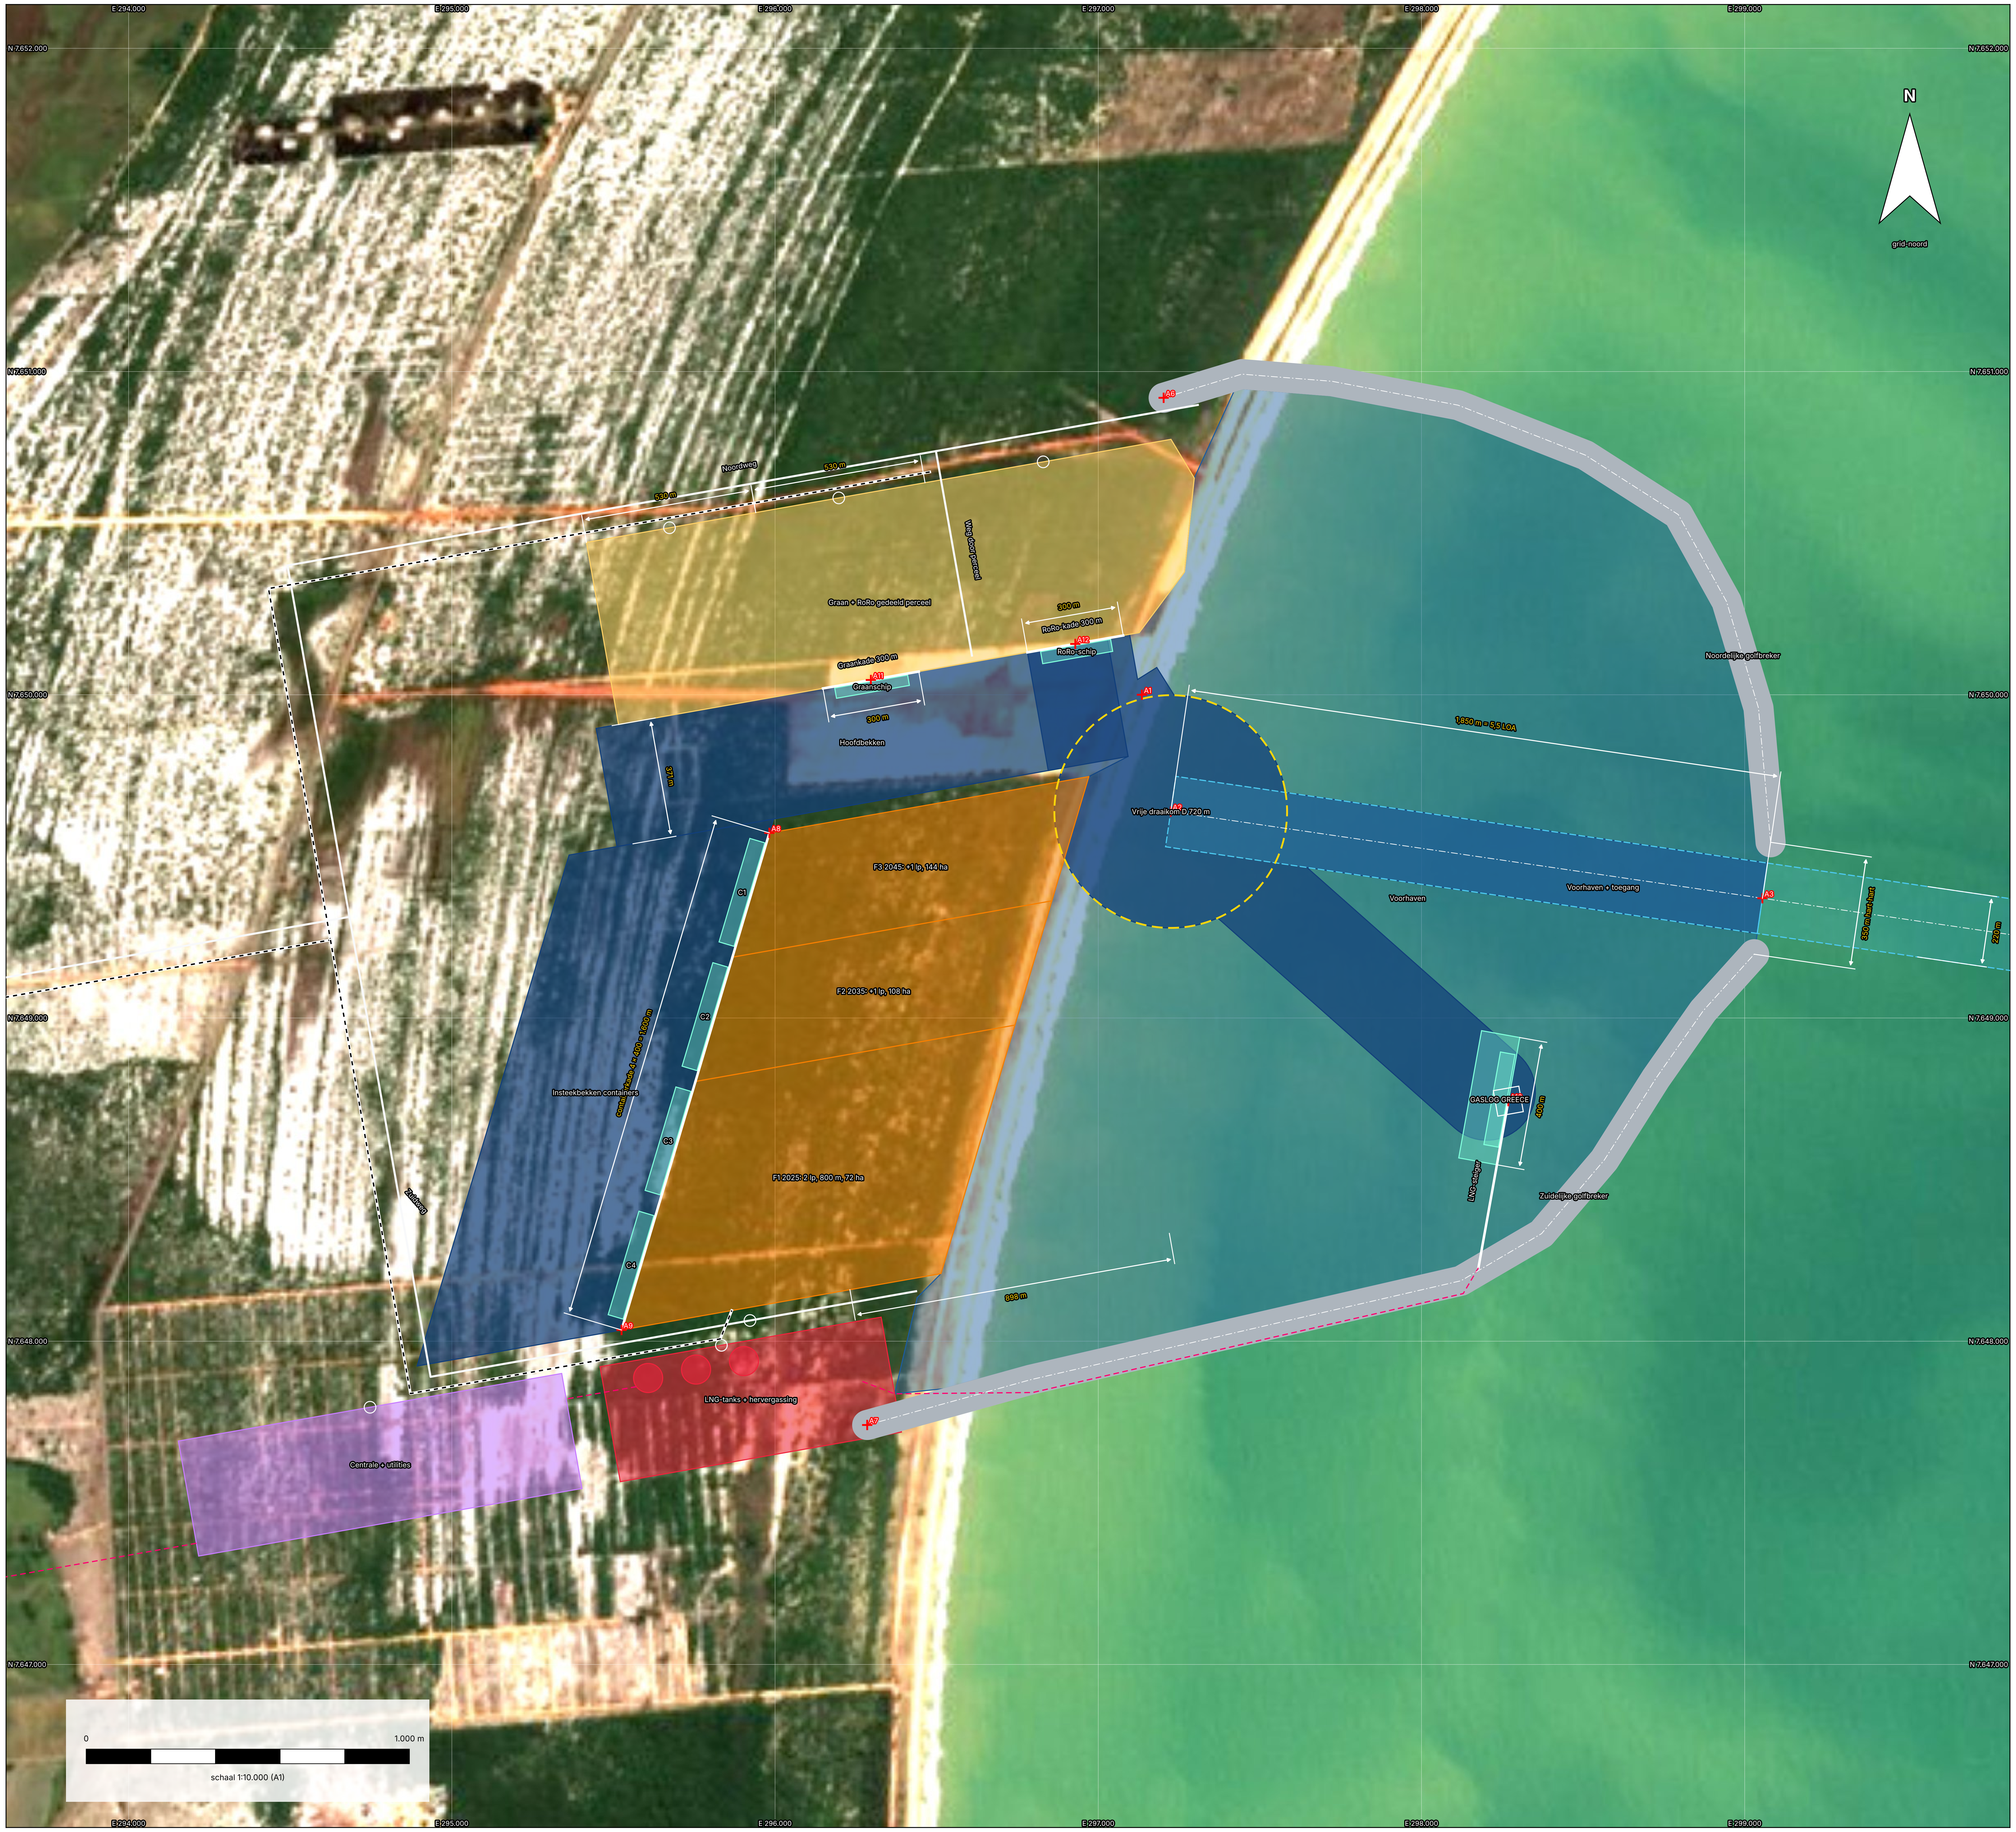

LEGENDA

━	Waterlijn 3-7-2026 (NDWI, geen MLWS-lijn)
– –	Zoekgebied locatie B (indicatief)
■	Voorhaven binnen de dammen (strandwal ontgraven)
■	Gebaggerd tot -18,20 m MLWS (voorlopig)
▭	Geul 220 m bodembreedte
▭	Vrije draaikom D = 720 m
▭	Havenmond vrij 350 m
■	Golfbreker (footprint 90 m, voorlopig)
	Kade / steiger
■	Scheepsenveloppe aan ligplaats
■	Containerterminal
■	Graanterminal
■	LNG-steiger, tanks en hervergassing
■	Centrale + utilities (reservering)
━	Hoofdweg + terminalinritten
- - -	Spoor
– – ·	LNG/gasleiding, koelwater (indicatief)
+	Ontwerpankerpunt (E/N in maatstaat)

Hoofdmaten (gemeten in tekening)
Geul bodembreedte 220 m, bodem -18,20 m MLWS (voorlopig)
Geul buiten de mond: 18.000 m (voorlopig)
Havenmond vrij tussen dammen: 260 m
Draaikom D 720 m; vrij van schepen 167 m
Stopweg mond-draaikom 1.850 m = 5,5 LOA
Containerkade 802 / 1.203 / 1.604 m
Containerterrein 72,0 / 108,0 / 144,0 ha
Graan 103,8 ha, RoRo 103,8 ha, kades 300 m
LNG-zone 31,9 ha; centrale (reservering) 43,5 ha
Vrije breedte binnenbekken 329 m
Fasen (globaal)
F1 = zuideinde containervinger, F2/F3 richting hoofdbekken (zie DO)

Vormreferentie: Porto Central masterplan 2016, p. 9 (ANTT)

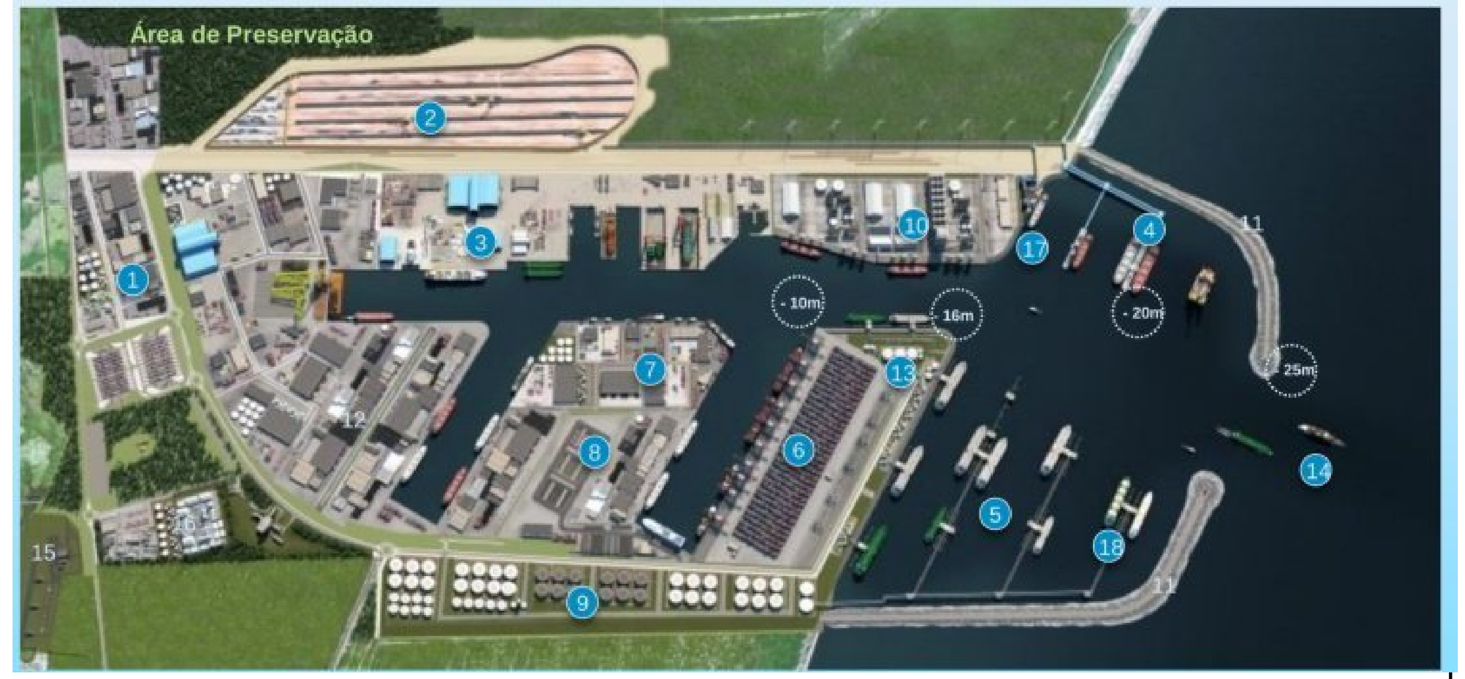

Overgenomen: 11/14 dammen en ingang | 6 containervinger | 10 graan (+ RoRo) | 9 tankpark (LNG + centrale) | 18 LNG-steiger. Weggelaten (niet in opdracht): 2, 3, 5, 7/8, 12, 1

Project	Havenontwerp Porto Central, Presidente Kennedy (ES) - Groep 1
Module	Atelier De Haven A | NHL Stenden Civiele Techniek
Bladnaam	**Havenindeling**
Status	**SCHETSONTWERP (SO)**
Blad / versie	SO-02 | versie 3.0 | 22-10-2026
Schaal	1:10.000 op A1 (841 × 594 mm)
Stelsel	SIRGAS 2000 / UTM zone 24S EPSG:31984 eenheid m
Hoogtedatum	diepten in m t.o.v. MLWS, voorlopig; MLWS-DHN te verifiëren
Kaartbron	Copernicus Sentinel-2 L2A (ESA), 03-07-2026, 10 m
	tegels 24KTB/24KUB, AWS Open Data COG; geraadpleegd 22-10-2026
Kustlijn	waterlijn 03-07-2026 uit NDWI (geen MLWS-lijn)

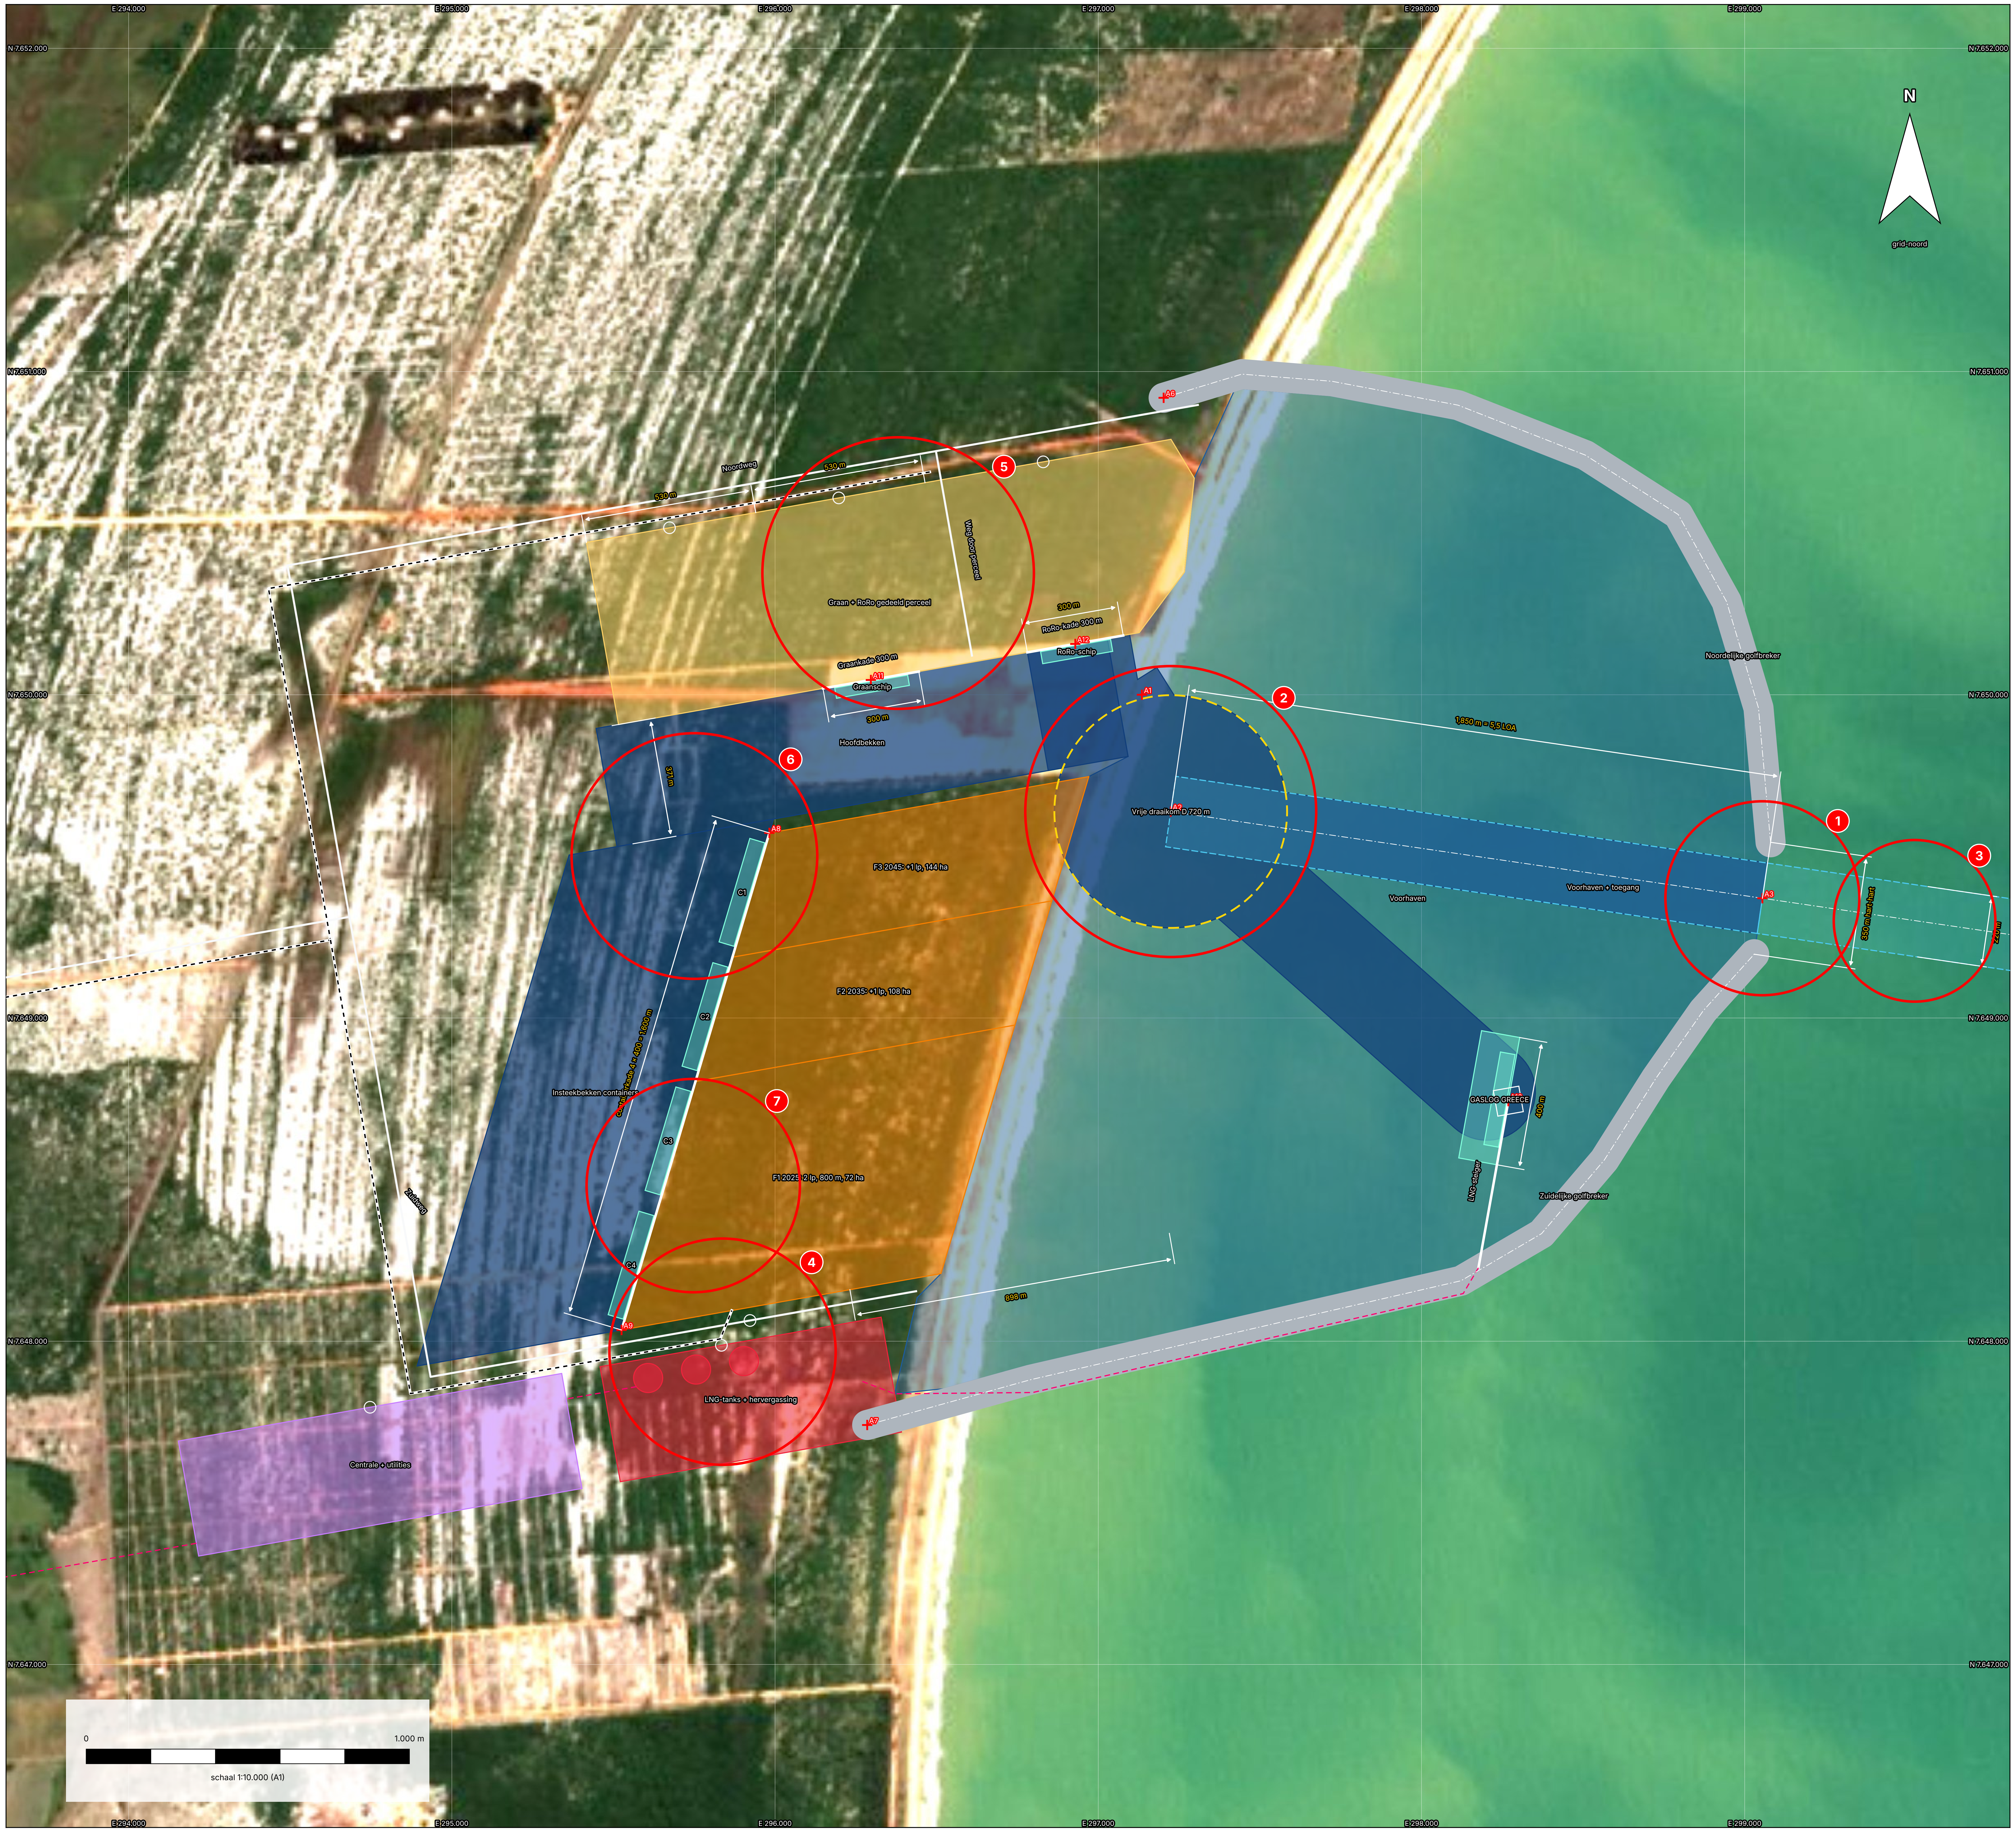

LEGENDA

▬ Waterlijn 3-7-2026 (NDWI, geen MLWS-lijn)
– – Zoekgebied locatie B (indicatief)
▨ Voorhaven binnen de dammen (strandwal ontgraven)
■ Gebaggerd tot -18,20 m MLWS (voorlopig)
▨ Geul 220 m bodembreedte
▭ Vrije draaikom D = 720 m
▭ Havenmond vrij 350 m
■ Golfbreker (footprint 90 m, voorlopig)
Kade / steiger
▨ Scheepsenveloppe aan ligplaats
▨ Containerterminal
▨ Graanterminal
▨ LNG-steiger, tanks en hervergassing
▨ Centrale + utilities (reservering)
▬ Hoofdweg + terminalinritten
- - - Spoor
– – · LNG/gasleiding, koelwater (indicatief)
+ Ontwerpankerpunt (E/N in maatstaat)

Bespreekpunten SO (zie rode markering)

1. Havenmond 260 m vrij tussen dammen (350 m hart-hart gemeten)
2. Draaikom overlapt de containervinger (1,5 ha)
3. Geen sleepbootkoppelpunt; geul knikt 15 gr op 2,2 km buiten de mond
4. LNG-tanks op 116 m van het containerterrein
5. Graan + RoRo op één perceel aan de noordkade; weg kruist het terrein
6. Containerschip 334 m moet 63 gr draaien van hoofdbekken (370 m) naar insteek: niet haalbaar
7. Containers F1 aan het zuideinde van de insteek; alles in F1 baggeren

Vormreferentie: Porto Central masterplan 2016, p. 9 (ANTT)

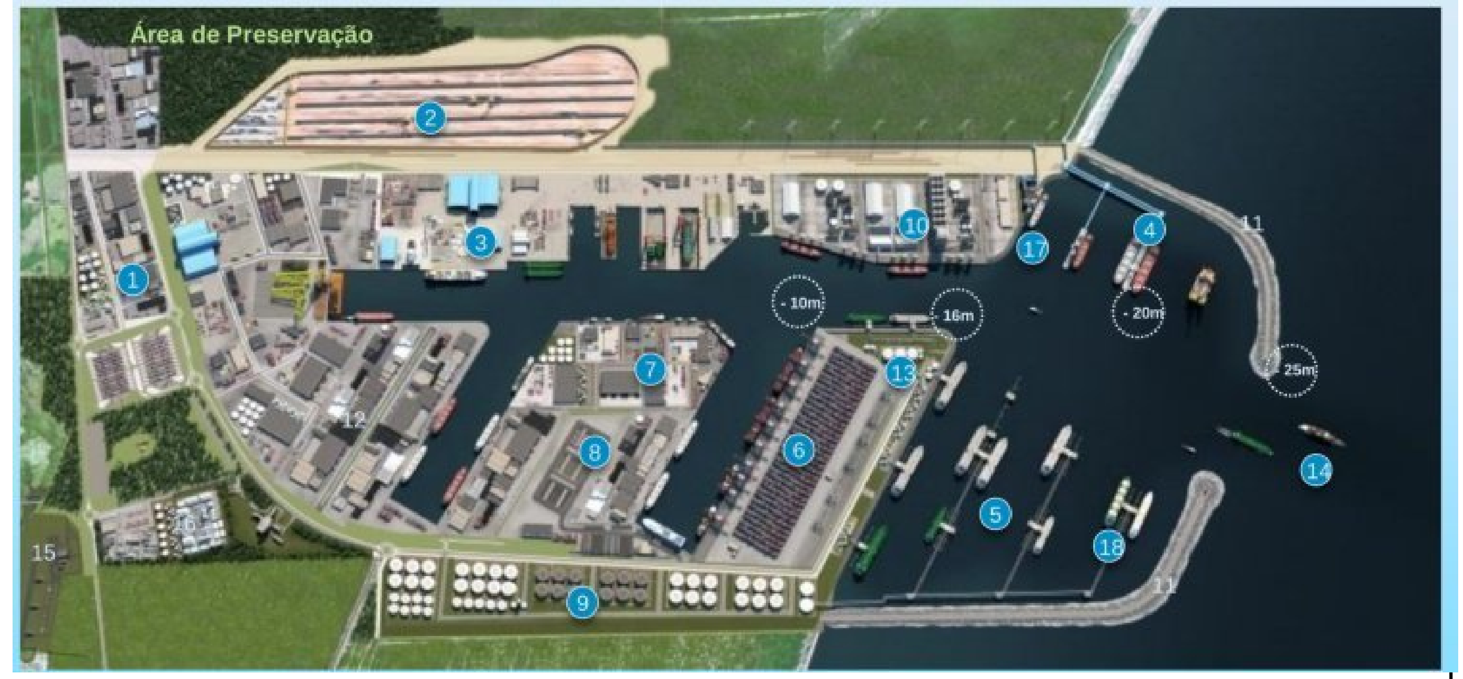

Overgenomen: 11/14 dammen en ingang | 6 containervinger | 10 graan (+ RoRo) | 9 tankpark (LNG + centrale) | 18 LNG-steiger. Weggelaten (niet in opdracht): 2, 3, 5, 7/8, 12, 1

Project	Havenontwerp Porto Central, Presidente Kennedy (ES) - Groep 1
Module	Atelier De Haven A | NHL Stenden Civiele Techniek
Bladnaam	**Bespreking SO - bespreekpunten**
Status	**SCHETSONTWERP (SO)**
Blad / versie	SO-03 | versie 3.0 | 22-10-2026
Schaal	1:10.000 op A1 (841 × 594 mm)
Stelsel	SIRGAS 2000 / UTM zone 24S EPSG:31984 eenheid m
Hoogtedatum	diepten in m t.o.v. MLWS, voorlopig; MLWS-DHN te verifiëren
Kaartbron	Copernicus Sentinel-2 L2A (ESA), 03-07-2026, 10 m
	tegels 24KTB/24KUB, AWS Open Data COG; geraadpleegd 22-10-2026
Kustlijn	waterlijn 03-07-2026 uit NDWI (geen MLWS-lijn)