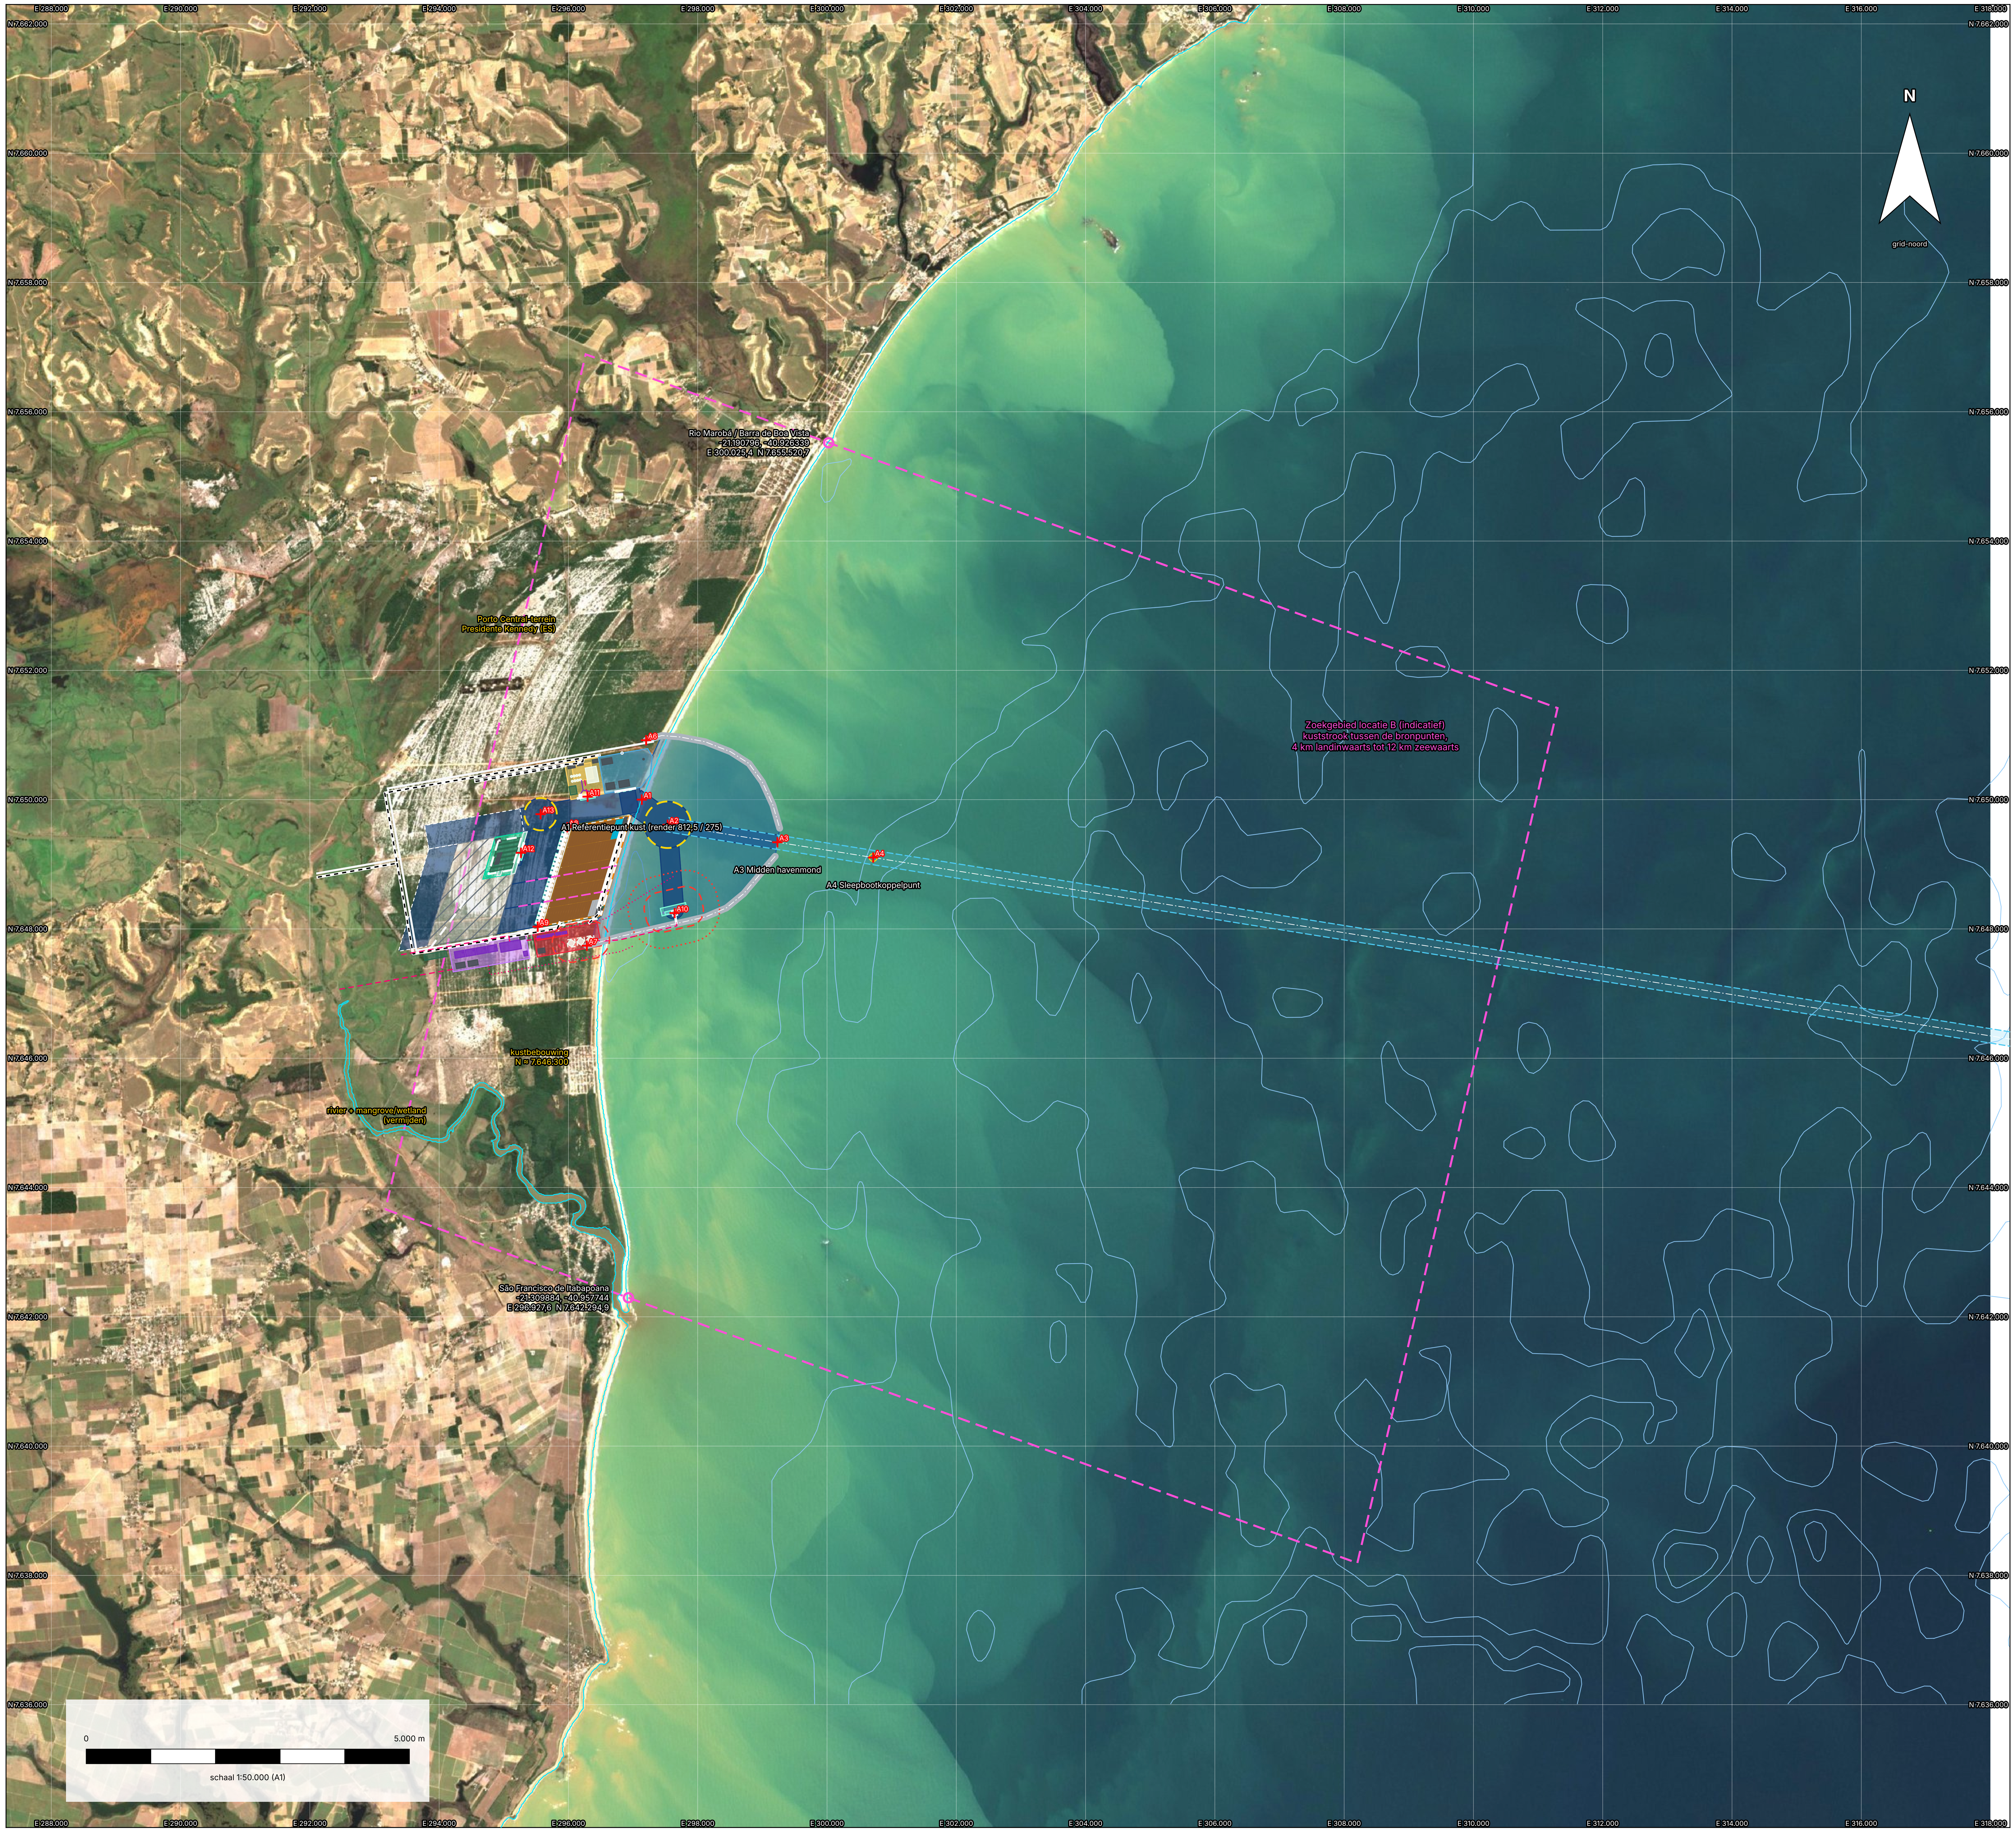

LEGENDA

━	Waterlijn 3-7-2026 (NDWI, geen MLWS-lijn)
- -	Zoekgebied locatie B (indicatief)
■	Voorhaven binnen de dammen (strandwal ontgraven)
■	Gebaggerd tot -18,20 m MLWS (voorlopig)
▭	Geul 220 m bodembreedte
▭	Vrije draaikom D = 720 m
▭	Havenmond vrij 350 m
■	Golfbreker (footprint 90 m, voorlopig)
	Kade / steiger
■	Scheepsenveloppe aan ligplaats
■	Containerterminal
■	Graanterminal
■	RoRo / voertuigenterminal
■	LNG-steiger, tanks en hervergassing
■	Centrale + utilities (reservering)
■	Havendiensten, sleepboten, loodsen
▨	Reserveterrein / latere uitbreiding
━	Hoofdweg + terminalinritten
- - -	Spoor
- -	LNG/gasleiding, koelwater (indicatief)
- -	Fasegrens 2025 / 2035 / 2045
▭	Sleepbootkoppelpunt
+	Ontwerpankerpunt (E/N in maatstaat)
- -	Veiligheidszone LNG 250 m / controlezone 500 m (indicatief)
━	Dieptelijn t.o.v. MLWS (GEBCO 2026, indicatief)
□	Detail: apron, rijstroken, stackzone
■	Detail: stackblokken containers (RTG)
■	Detail: reefervakken
■	Detail: lege containers
□	Detail: kranen, kraanbanen, laadarmen
■	Detail: gebouwen
□	Detail: silo's, tanks, opslag
■	Detail: parkeervakken
■	Detail: installaties en dolphins

Havenligging (vastgesteld)
Porto Central, Presidente Kennedy - ES, 29350-000
Havenas haaks op de kust: azimut 110 gr (kust 20.1 gr).
A1 kustpunt: E 297.135,0 N 7.650.000,0
= -21.240329, -40.954826 (WGS84)
Havenas door het bouwterrein fase 1 aan het strand
(lichte rechthoek op de luchtfoto 03-07-2026);
bekkens landinwaarts op het kale Porto Central-terrein.

Georeferentiecontrole
GSHHS-kust vs. S2-waterlijn: gem. 14 m, sd 66 m
(15 profielen, N 7.642-7.656 km)
Bekende afstand bronpunten: 13.582,4 m geodetisch,
13.583,8 m in grid (k = 1.00010)
Noordrichting: convergentie 0.70 gr

Referentie: Porto Central render (overgetrokken voor het DO)

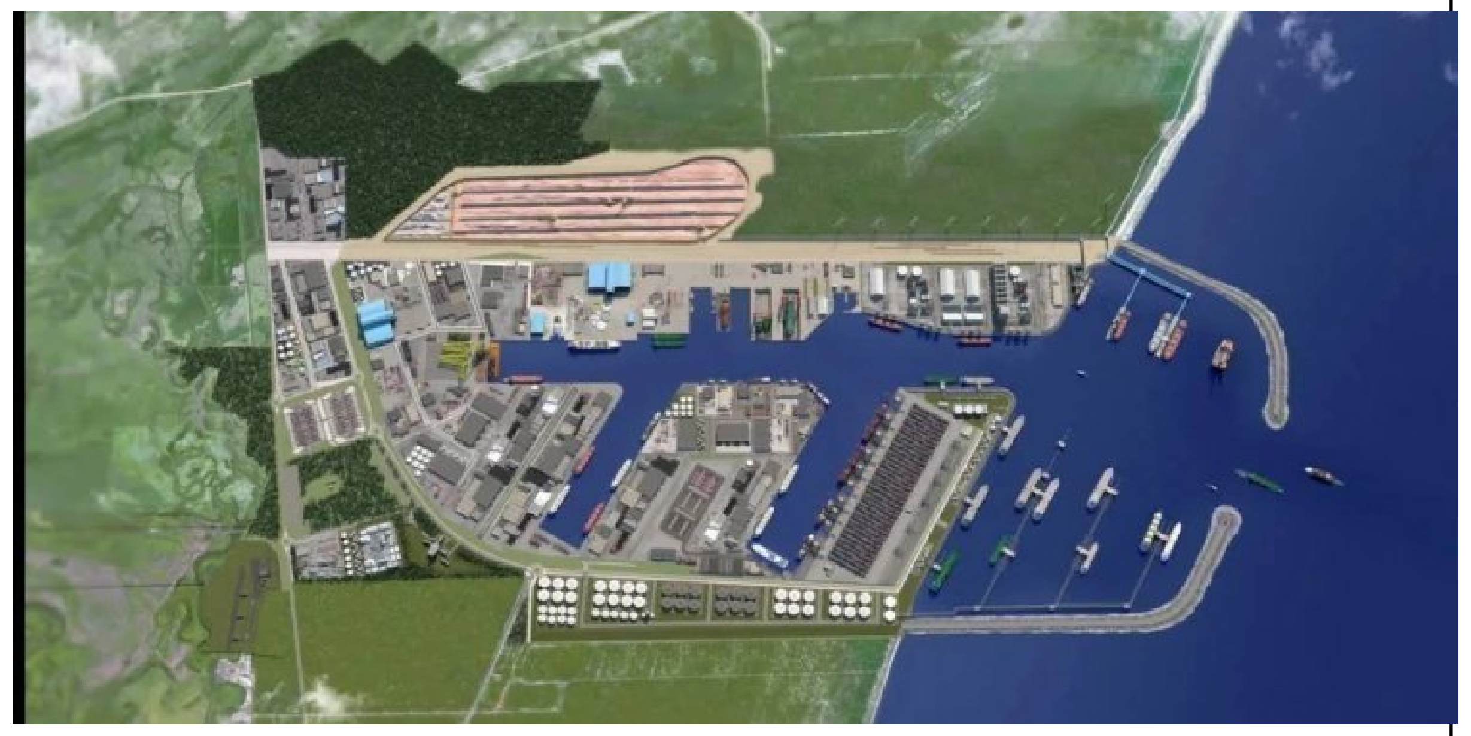

Overgenomen: 11/14 dammen | vingers en insteken | 6 containers | 10 graan | 7/8 RoRo
9 tankpark (LNG + centrale) | 18 LNG-steiger. Weggelaten (niet in opdracht): 2, 3, 5, 12, 1

Project	Havenontwerp Porto Central, Presidente Kennedy (ES) - Groep 1
Module	Atelier De Haven A | NHL Stenden Civiele Techniek
Bladnaam	**Overzicht zoekgebied en havenligging**
Status	**DEFINITIEF ONTWERP (DO)**
Blad / versie	DO-01 | versie 7.0 | 22-10-2026
Schaal	1:50.000 op A1 (841 × 594 mm)
Stelsel	SIRGAS 2000 / UTM zone 24S EPSG:31984 eenheid m
Hoogtedatum	diepten in m t.o.v. MLWS, voorlopig; MLWS-DHN te verifiëren
Kaartbron	Copernicus Sentinel-2 L2A (ESA), 03-07-2026, 10 m tegels 24KTB/24KUB, AWS Open Data COG; geraadpleegd 22-10-2026
Kustlijn	waterlijn 03-07-2026 uit NDWI (geen MLWS-lijn)
Bathymetrie	GEBCO 2026 (ca. 450 m) + Copernicus DEM 30 m; MSL→MLWS +0,7 m (aanname) geen lodingen: peiling (multibeam) nodig vóór uitvoering

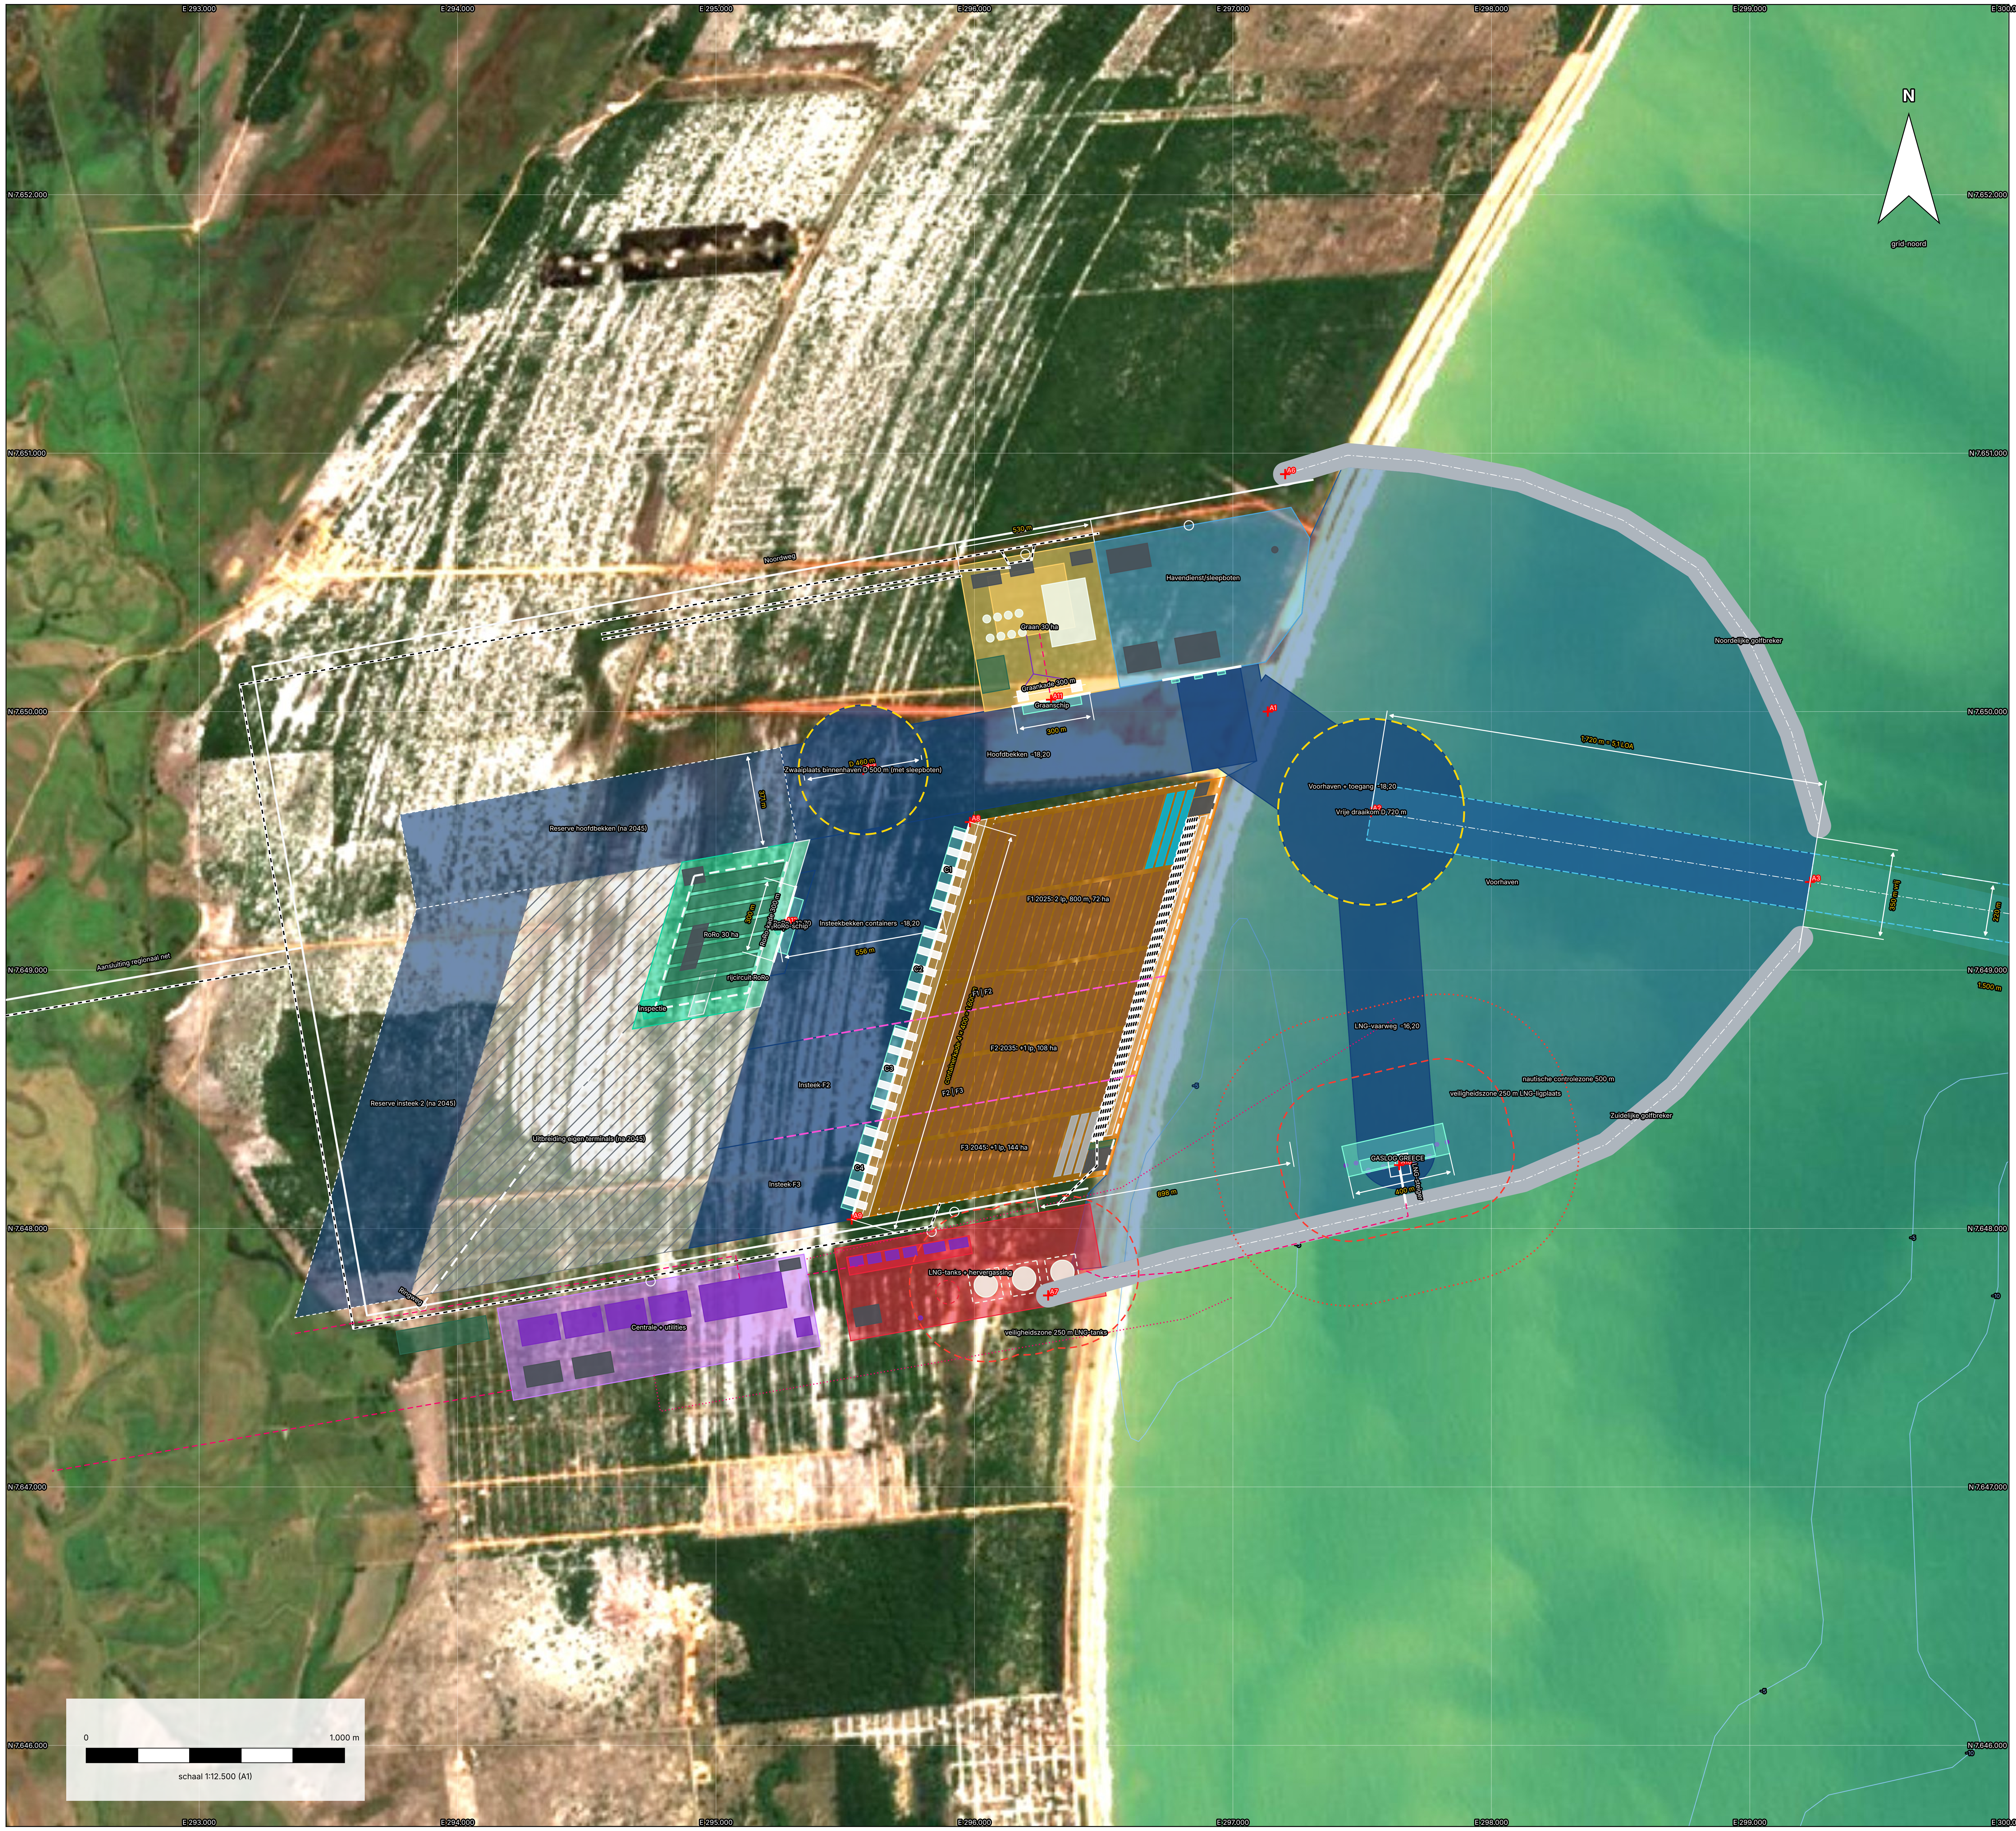

LEGENDA

- Waterlijn 3-7-2026 (NDWI, geen MLWS-lijn)
- Zoekgebied locatie B (indicatief)
- Voorhaven binnen de dammen (strandwal ontgraven)
- Gebaggerd tot -18,20 m MLWS (voorlopig)
- Geul 220 m bodembreedte
- Vrije draaikom D = 720 m
- Havenmond vrij 350 m
- Golfbreker (footprint 90 m, voorlopig)
- Kade / steiger
- Scheepsenveloppe aan ligplaats
- Containerterminal
- Graanterminal
- RoRo / voertuigenterminal
- LNG-steiger, tanks en hervergassing
- Centrale + utilities (reservering)
- Havendiensten, sleepboten, loodsen
- Reserveterrein / latere uitbreiding
- Hoofdweg + terminalinritten
- Spoor
- LNG/gasleiding, koelwater (indicatief)
- Fasegrens 2025 / 2035 / 2045
- Sleepbootkoppelpunt
- + Ontwerpankerpunt (E/N in maatstaat)
- Veiligheidszone LNG 250 m / controlezone 500 m (indicatief)
- Dieptelijn t.o.v. MLWS (GEBCO 2026, indicatief)
- Detail: apron, rijstroken, stackzone
- Detail: stackblokken containers (RTG)
- Detail: reefervakken
- Detail: lege containers
- Detail: kranen, kraanbanen, laadarmen
- Detail: gebouwen
- Detail: silo's, tanks, opslag
- Detail: parkeervakken
- Detail: installaties en dolphins

Hoofdmaten (gemeten in tekening)

Geul 220 m breed, 35.000 m buiten de mond (GEBCO: pas
daar natuurlijk -18,2 m; -15 m op 24.000 m), zie DO-10
Dieptezones (diepgang + 3,7 m): containers/graan/geul -18,20;
LNG-vaarweg en -ligplaats -16,20; RoRo -13,70 m MLWS
Havenmond vrij 350 m; stopweg 1.720 m = 5,1 LOA
Draaikom voorhaven D 720 m, vrij van schepen 416 m
Zwaaiplaats binnenhaven D 500 m (1,5 LOA, met sleepboten),
165 m vrij van schepen, 91 m van de oever
Containerkade westzijde vinger 6 (in de insteek, beschut):
802 / 1.203 / 1.604 m; terrein 72,0 / 108,0 / 144,0 ha
Graan 30,4 ha, RoRo 30,2 ha, kades 300 m
LNG-zone 36,3 ha; steiger achter de zuidelijke dam
veiligheidszone 250 m, nautische controlezone 500 m
Golftoets: alle ligplaatsen voldoen (zie DO-09)

Referentie: Porto Central render (overgetrokken voor het DO)

Overgenomen: 11/14 dammen | vingers en insteken | 6 containers | 10 graan | 7/8 RoRo
9 tankpark (LNG + centrale) | 18 LNG-steiger. Weggelaten (niet in opdracht): 2, 3, 5, 12, 1

Project	Havenontwerp Porto Central, Presidente Kennedy (ES) - Groep 1
Module	Atelier De Haven A | NHL Stenden Civiele Techniek
Bladnaam	**Havenindeling**
Status	**DEFINITIEF ONTWERP (DO)**
Blad / versie	DO-02 | versie 7.0 | 22-10-2026
Schaal	1:12.500 op A1 (841 × 594 mm)
Stelsel	SIRGAS 2000 / UTM zone 24S EPSG:31984 eenheid m
Hoogtedatum	diepten in m t.o.v. MLWS, voorlopig; MLWS-DHN te verifiëren
Kaartbron	Copernicus Sentinel-2 L2A (ESA), 03-07-2026, 10 m
	tegels 24KTB/24KUB, AWS Open Data COG; geraadpleegd 22-10-2026
Kustlijn	waterlijn 03-07-2026 uit NDWI (geen MLWS-lijn)
Bathymetrie	GEBCO 2026 (ca. 450 m) + Copernicus DEM 30 m; MSL→MLWS +0,7 m (aanname)
	geen lodingen: peiling (multibeam) nodig vóór uitvoering

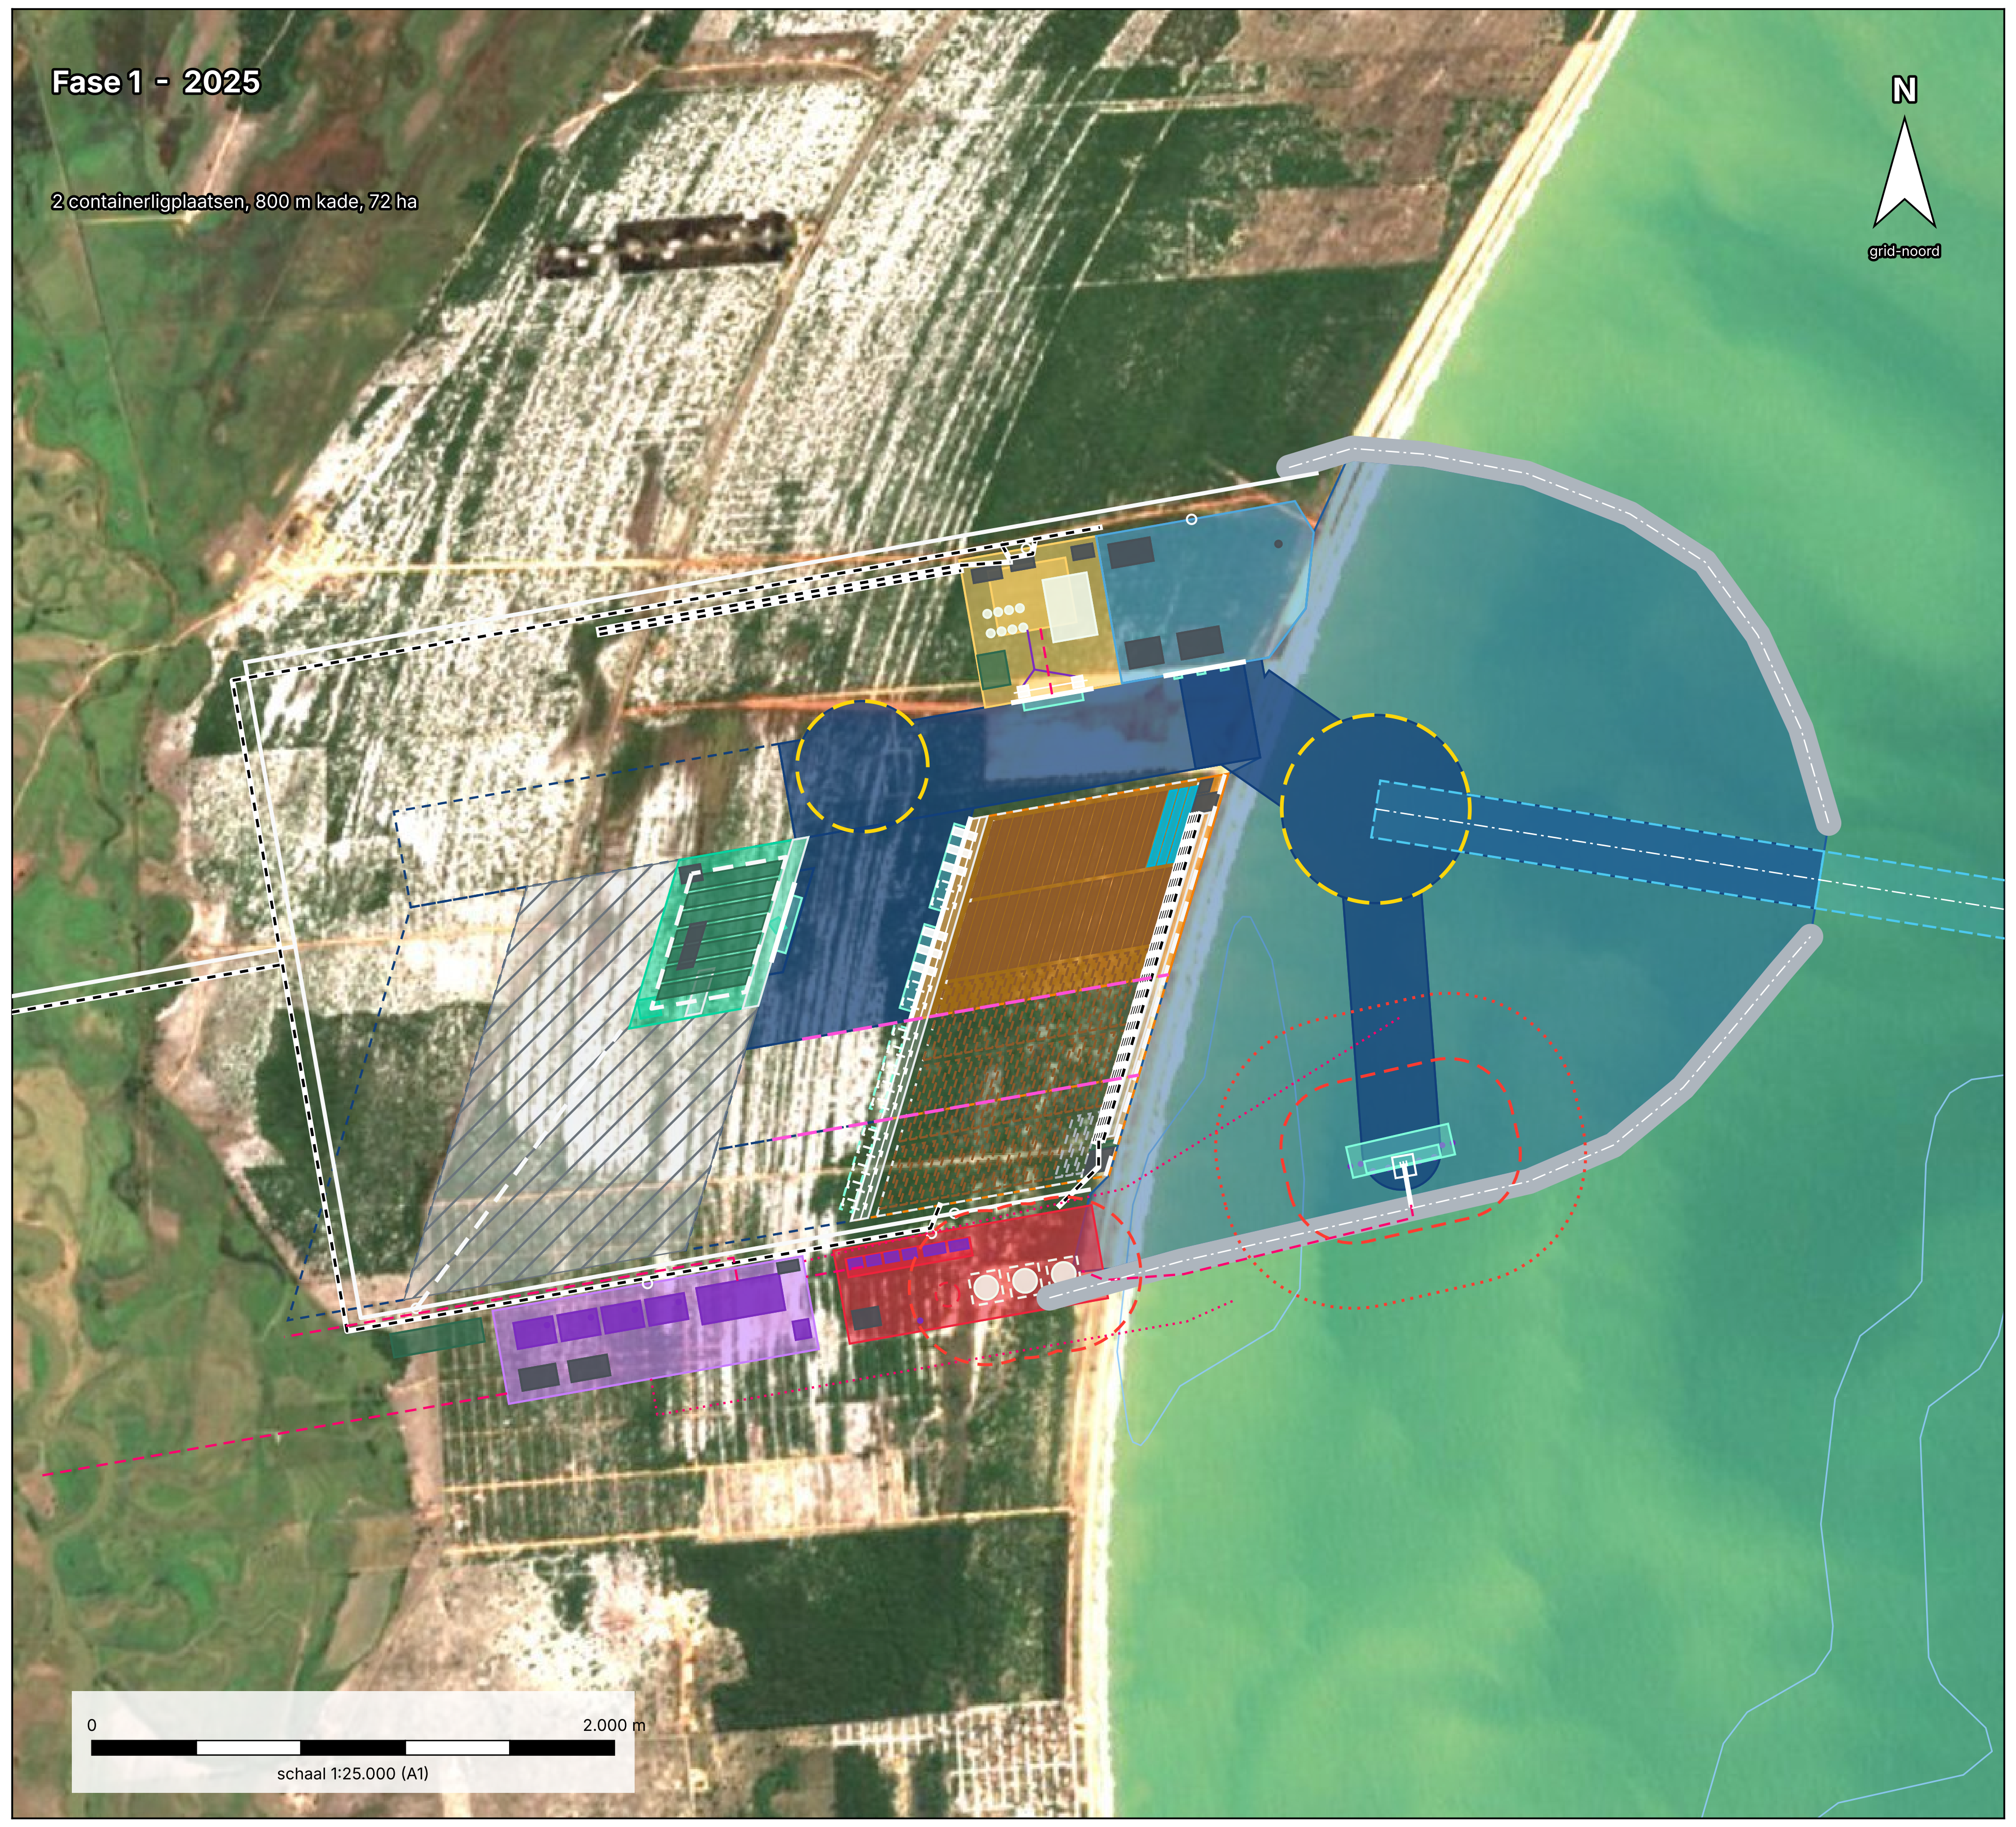

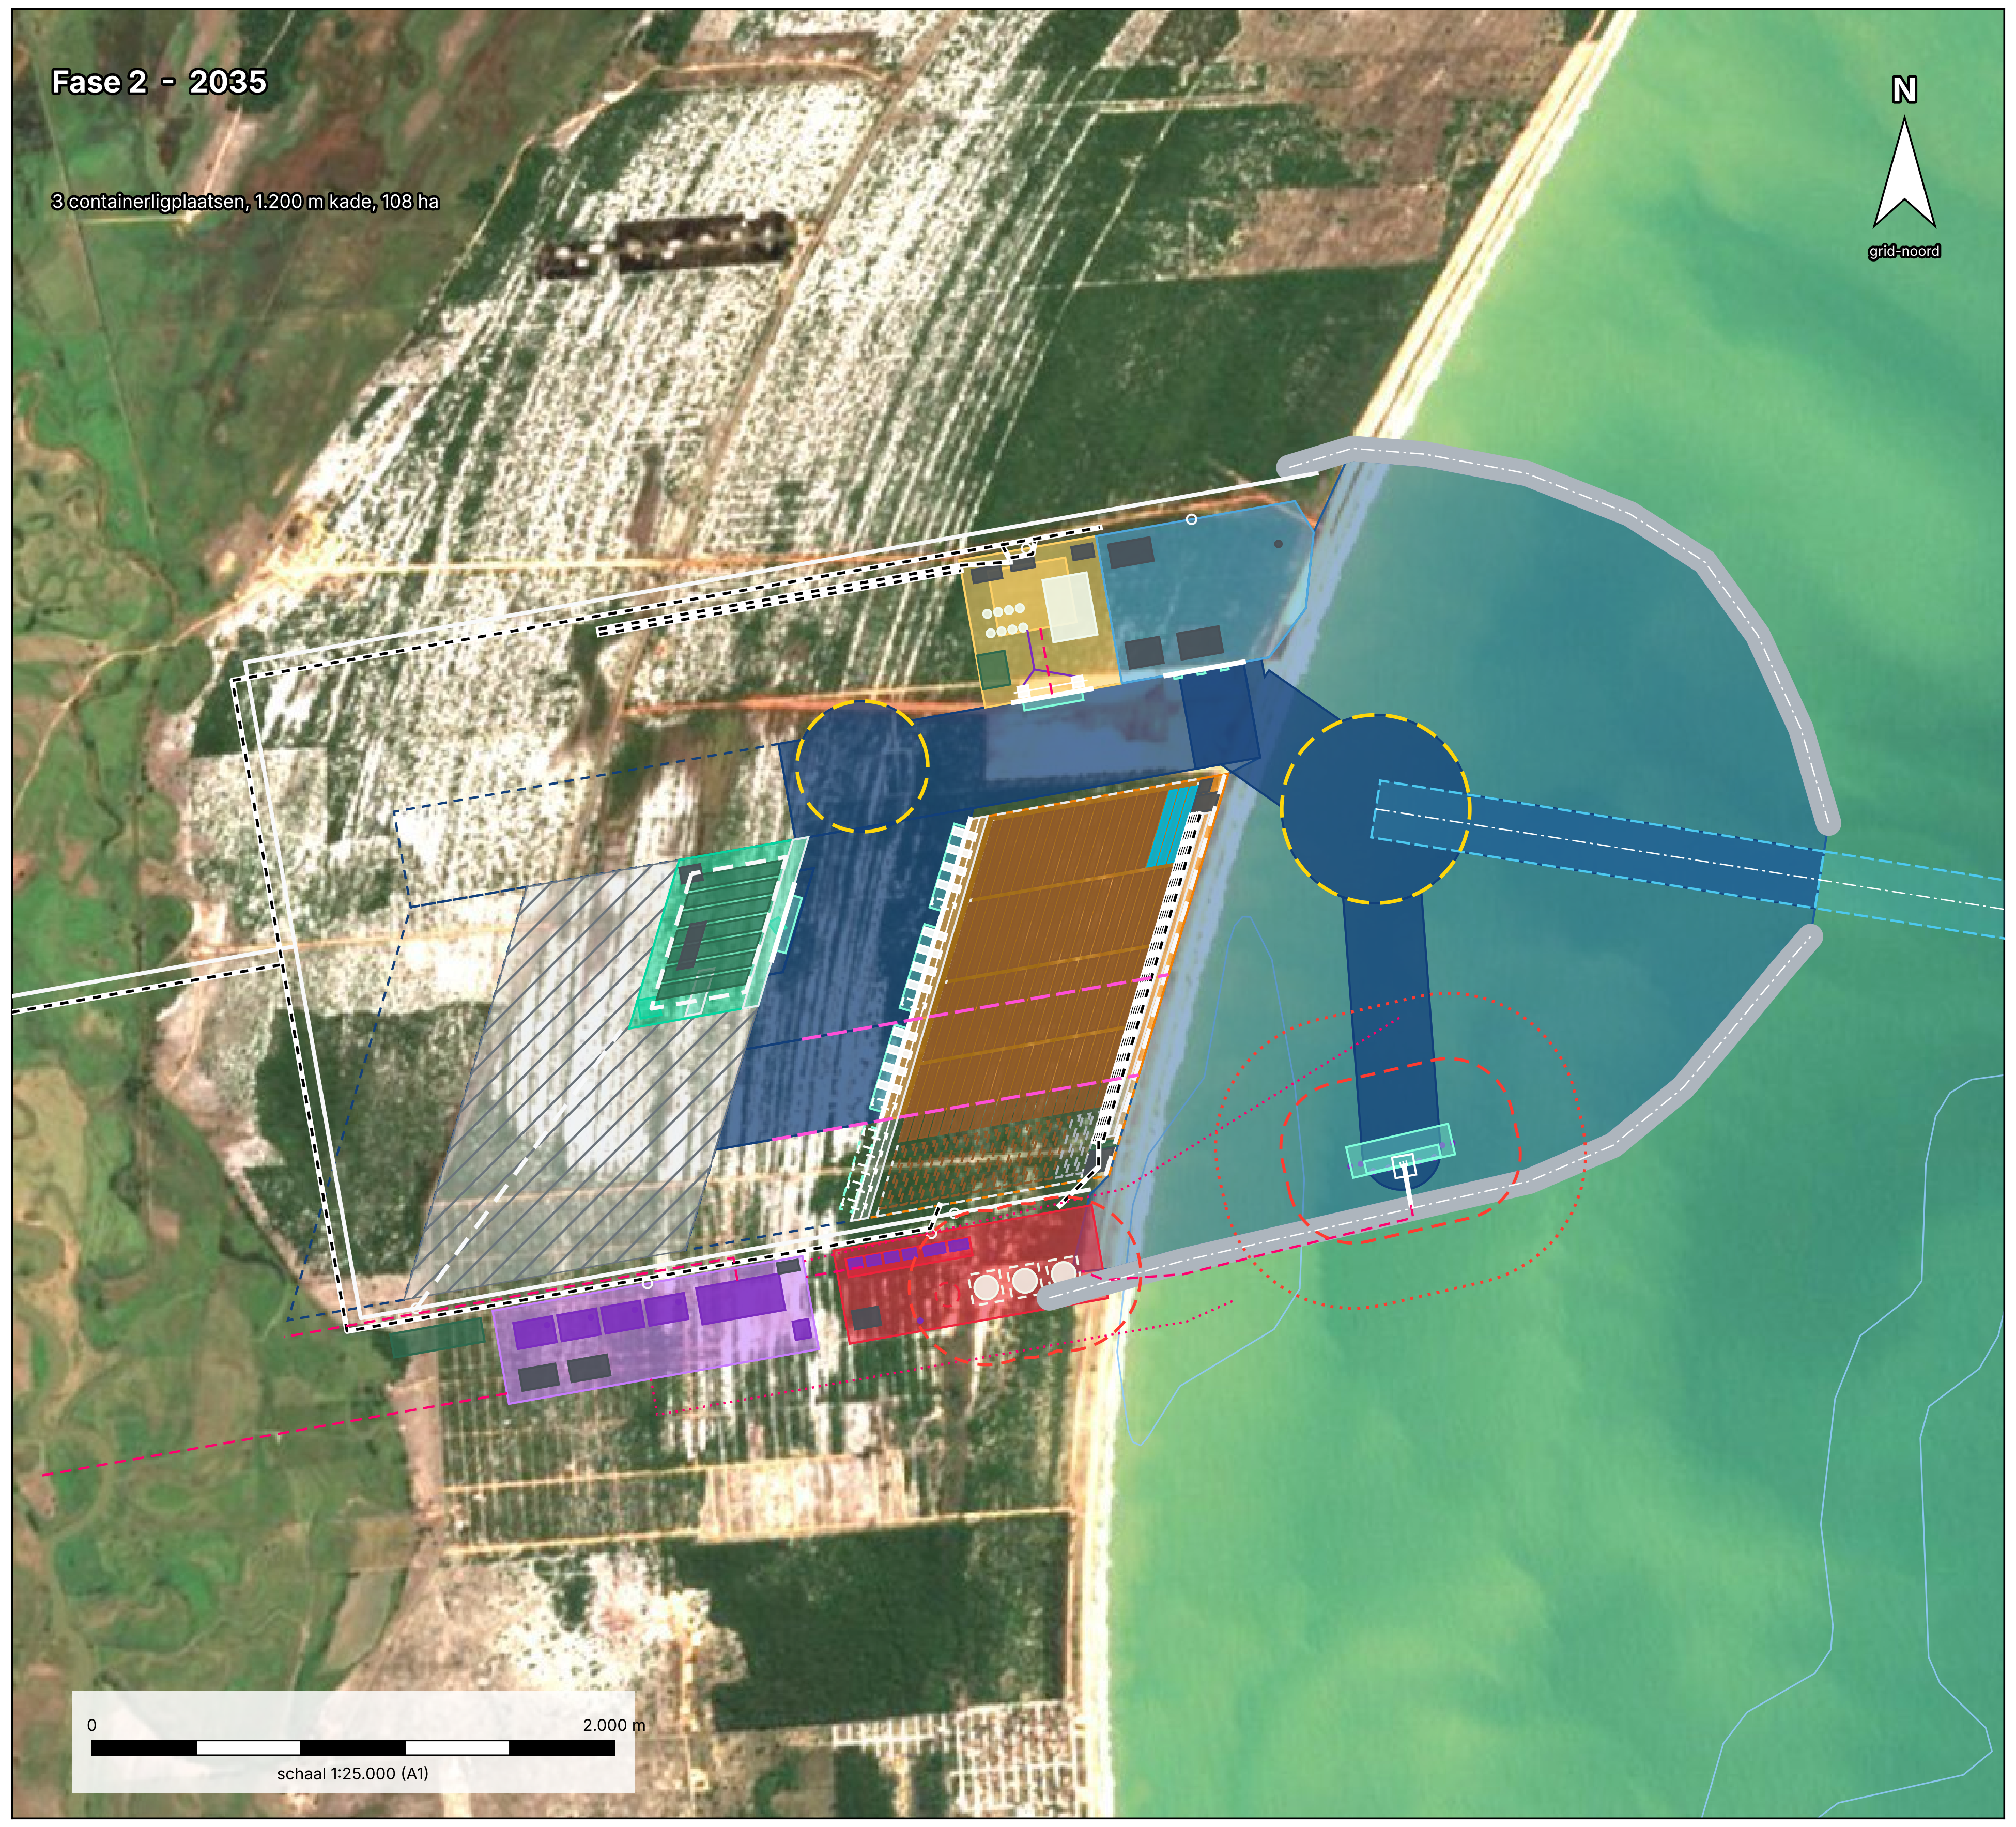

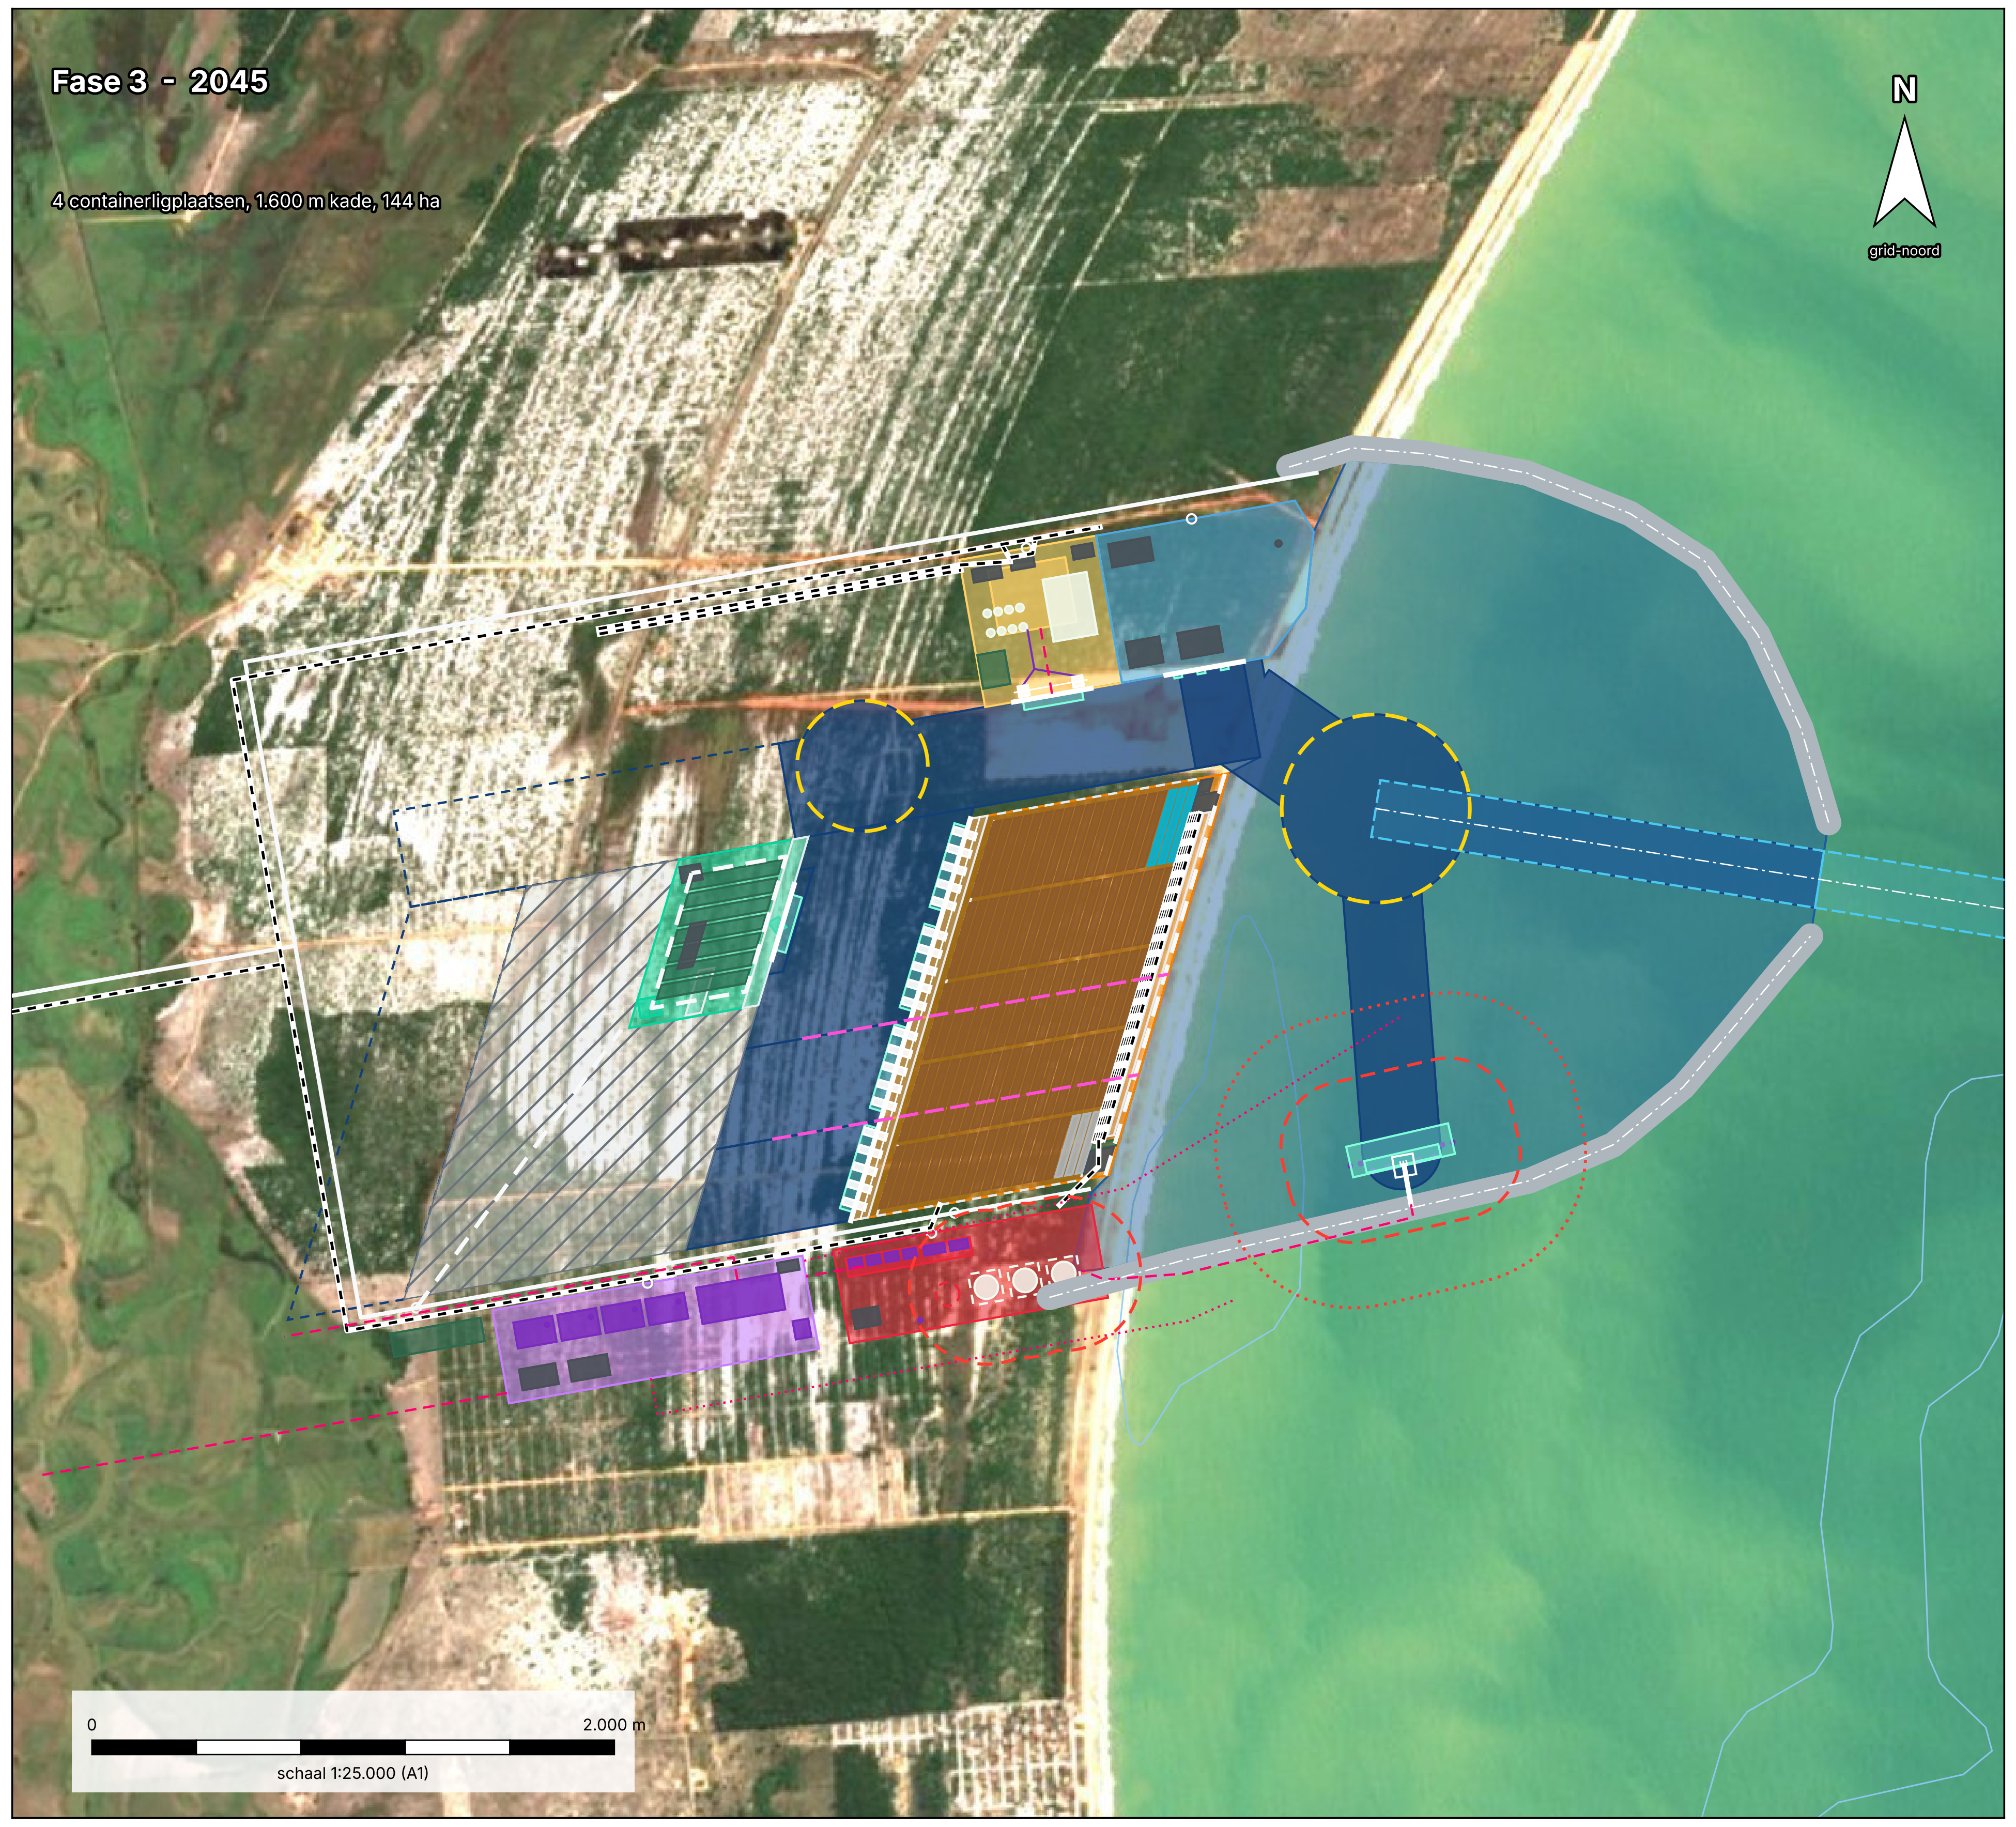

LEGENDA

- ━ Waterlijn 3-7-2026 (NDWI, geen MLWS-lijn)
- ╍ Zoekgebied locatie B (indicatief)
- ■ Voorhaven binnen de dammen (strandwal ontgraven)
- ■ Gebaggerd tot -18,20 m MLWS (voorlopig)
- ▭ Geul 220 m bodembreedte
- ▭ Vrije draaikom D = 720 m
- ▭ Havenmond vrij 350 m
- ■ Golfbreker (footprint 90 m, voorlopig)
- Kade / steiger
- ■ Scheepsenveloppe aan ligplaats
- ■ Containerterminal
- ■ Graanterminal
- ■ RoRo / voertuigenterminal
- ■ LNG-steiger, tanks en hervergassing
- ■ Centrale + utilities (reservering)
- ■ Havendiensten, sleepboten, loodsen
- ▨ Reserveterrein / latere uitbreiding
- ━ Hoofdweg + terminalinritten
- ╍ Spoor
- ╍ LNG/gasleiding, koelwater (indicatief)
- ╍ Fasegrens 2025 / 2035 / 2045
- ▭ Sleepbootkoppelpunt
- + Ontwerpankerpunt (E/N in maatstaat)
- ╍ Veiligheidszone LNG 250 m / controlezone 500 m (indicatief)
- ━ Dieptelijn t.o.v. MLWS (GEBCO 2026, indicatief)
- □ Detail: apron, rijstroken, stackzone
- ■ Detail: stackblokken containers (RTG)
- ■ Detail: reefervakken
- ■ Detail: lege containers
- □ Detail: kranen, kraanbanen, laadarmen
- ■ Detail: gebouwen
- □ Detail: silo's, tanks, opslag
- ■ Detail: parkeervakken
- ■ Detail: installaties en dolphins

Fasering (rekenboek Containers / Overige terminals)

Onderdeel	Fase 1 - 2025	Fase 2 - 2035	Fase 3 - 2045
Containerligplaatsen	2 (C1-C2)	3 (+C3)	4 (+C4)
Containerkade	800 m	1.200 m	1.600 m
Containerterrein	72 ha	108 ha	144 ha
Rekenvraag terrein	40,8 ha	67,9 ha	135,9 ha
Kranen per schip / totaal	3 / 6	4 / 12	5 / 20
Kadebezetting	60,0%	51,3%	63,1%
Bekkens gebaggerd	hoofd-, insteek-, containerb. N	+ containerbekken midden	+ containerbekken zuid
Graan / RoRo	1 lp, 30 ha elk	equipment +	pieken toetsen
LNG	steiger + 3 tanks	doorzet 6 mln m3	8 mln m3; N-1 besluit
Centrale	eindcapaciteit	-	-
Golfbrekers + geul	volledig	onderhoud	onderhoud

De containerkade ligt aan de westzijde van vinger 6 in het insteekbekken (beschut, DO-09) en groeit zuidwaarts; baggeren en kadebouw voor F2/F3 gebeuren aan het zuideinde van de insteek, achter de schepen aan C1/C2 en buiten de zwaaiplaats.
Toekomstige onderdelen zijn gestippeld; alleen functies uit de opdracht zijn getekend.
Golfbrekers, geul, draaikom, LNG-steiger en leidingcorridors worden in F1 op eindmaat aangelegd (latere uitbreiding is onevenredig duur, rapport par. 10).

Project	Havenontwerp Porto Central, Presidente Kennedy (ES) - Groep 1
Module	Atelier De Haven A | NHL Stenden Civiele Techniek
Bladnaam	**Fasering 2025 - 2035 - 2045**
Status	**DEFINITIEF ONTWERP (DO)**
Blad / versie	DO-03 | versie 7.0 | 22-10-2026
Schaal	1:25.000 op A1 (841 × 594 mm)
Stelsel	SIRGAS 2000 / UTM zone 24S EPSG:31984 eenheid m
Hoogtedatum	diepten in m t.o.v. MLWS, voorlopig; MLWS-DHN te verifiëren
Kaartbron	Copernicus Sentinel-2 L2A (ESA), 03-07-2026, 10 m tegels 24KTB/24KUB, AWS Open Data COG; geraadpleegd 22-10-2026
Kustlijn	waterlijn 03-07-2026 uit NDWI (geen MLWS-lijn)
Bathymetrie	GEBCO 2026 (ca. 450 m) + Copernicus DEM 30 m; MSL→MLWS +0,7 m (aanname) geen lodingen: peiling (multibeam) nodig vóór uitvoering

Maatstaat DO - tekening tegen rekenboek

Onderdeel	Gemeten in DO-tekening	Rekenboek	Status
Hoofdgeul bodembreedte	220 m	Nautiek D20 = 220	rekenuitkomst
Bodemhoogte geul/bekken	-18,20 m MLWS	Nautiek D25 = 18,20	voorlopig
Geullengte buiten mond	35.000 m	Nautiek D31 (GEBCO 2026)	geen peiling
Dieptezone LNG / RoRo	-16,20 / -13,70 m MLWS	diepgang 12,5 / 10,0 + 3,7	bespaart bagger
Vrije draaikom voorhaven	D 720 m	Nautiek D28 = 720	vrij getoetst
Zwaaiplaats binnenhaven	D 500 m	1,5 LOA met sleepboten	vrij getoetst
afstand tot schepen/kades	416 / 397 m	> 0	voldoet
Havenmond vrij (footprints)	350 m	Nautiek D29 = 350	voldoet
Stopweg mond - draaikom	1.720 m	5 LOA = 1.670 m	voldoet
Sleepbootkoppelpunt	1.500 m buiten mond	rapport par. 5.1	ingetekend
Containerkade F1/F2/F3	802 / 1.203 / 1.604 m	800/1.200/1.600	gelijk
Containerterrein F1/F2/F3	72,0 / 108,0 / 144,0 ha	72/108/144 (vraag 40,8/67,9/135,9)	gelijk
Graankade / terrein	300 m / 30,4 ha	300 m / 30 ha (vraag 5,1)	gelijk
RoRo-kade / terrein	300 m / 30,2 ha	300 m / 30 ha (vraag 26,9)	gelijk
LNG-ligplaatsenvelop	400 m	ca. 400 m	dolphins indicatief
LNG-envelop tot draaikom	876 m	> 250 m zone	voldoet
Schepen/gebouwen in LNG-zone	0 / 0	0 (250 m)	QRA volgt
LNG-zone (3 tanks + optie 4e)	36,3 ha	3 × 180.000 m3	N-1 open
Centrale + utilities	43,5 ha	geen vast oppervlak	reservering
Vrije breedte binnenbekken	334 m	>= 220 m	voldoet
Havenbekken baggervak (zone 1)	278,3 ha	Grondwerk C6	ingevuld
Geul buiten mond (zone 2+3)	770,0 ha	Grondwerk C7+C8	split op -15 m
Terreinophoging	327,3 ha	Grondwerk D21	ingevuld
Baggervolume zone 1/2/3	59,1 / 29,9 / 3,6 mln m3	celmethode GEBCO/DEM	indicatief
Besparing dieptezones	0,75 mln m3	t.o.v. overal -18,20	

Ontwerpankerpunten - EPSG:31984 (E/N) en WGS84 (lat/lon)

Punt	Omschrijving	E (m)	N (m)	Lat	Lon
A1	Referentiepunt kust (render 812,5 / 275)	297.135,0	7.650.000,0	-21.240329	-40.954826
A2	Middelpunt vrije draaikom	297.534,6	7.649.611,9	-21.243878	-40.951023
A3	Midden havenmond	299.233,2	7.649.340,8	-21.246515	-40.934695
A4	Sleepbootkoppelpunt	300.714,4	7.649.104,3	-21.248813	-40.920454
A5	Eindpunt geul (voorlopig)	333.795,6	7.643.823,8	-21.299835	-40.602281
A6	Wortel noordelijke golfbreker	297.202,3	7.650.918,8	-21.232040	-40.954069
A7	Wortel zuidelijke golfbreker	296.285,1	7.647.740,8	-21.260634	-40.963283
A8	Containerkade noordeinde	295.982,5	7.649.572,6	-21.244060	-40.965978
A9	Containerkade zuideinde	295.525,1	7.648.034,8	-21.257895	-40.970569
A10	LNG-steigerkop	297.643,1	7.648.245,2	-21.256232	-40.950141
A11	Graankade midden	296.296,5	7.650.045,7	-21.239822	-40.962897
A12	RoRo-kade midden	295.265,7	7.649.177,7	-21.247545	-40.972930
A13	Middelpunt draaikom binnenhaven	295.569,8	7.649.775,0	-21.242186	-40.969929

Geometrie overgetrokken van de Porto Central-render (Referentie/Porto_Central_render.png), pixel (x, y omlaag):
schaal 10,035 m/px, draaiing 10,0 gr; render (812,5; 275) = A1. Kustfit: gemiddeld 31 m.
E = a x + b y + c; N = d x + e y + f met a..f in Maatstaat/maatstaat.json (render_affine).
Alle maten in de DXF staan direct in projectcoördinaten; er is geen lokale verschuiving meer nodig.

Georeferentie - bronpunten en controles

Bronpunt case	WGS84	E	N	tot waterlijn
São Francisco de Itabapoana	-21.309884, -40.957744	296.927,6	7.642.294,9	18 m
Rio Marobá / Barra de Boa Vista	-21.190796, -40.926339	300.025,4	7.655.520,7	14 m

Kustlijncontrole: Sentinel-2 tegen onafhankelijke GSHHS-kust (full)

N (m)	E waterlijn S2	E kust GSHHS	dE (m)
7.642.000	296.762	296.821	58
7.643.000	296.930	296.914	-16
7.644.000	296.748	296.716	-32
7.645.000	296.570	296.527	-43
7.646.000	296.450	296.431	-19
7.647.000	296.460	296.416	-44
7.648.000	296.590	296.490	-100
7.649.000	296.818	296.829	11
7.650.000	297.136	297.126	-10
7.651.000	297.562	297.579	17
7.652.000	298.106	298.168	62
7.653.000	298.712	298.678	-34
7.654.000	299.148	299.246	98
7.655.000	299.669	299.815	146
7.656.000	300.280	300.391	111

Gemiddelde dE 13,8 m, sd 65,6 m: geen systematische verschuiving.
GSHHS heeft een nauwkeurigheid van orde 50-100 m; de spreiding past daarbij.
Bekende afstand bronpunten: geodetisch 13.582,4 m, grid 13.583,8 m,
verschil 1,38 m = schaalfactor k 1.000101 (UTM, verwacht).
Noordrichting: meridiaanconvergentie 0.70 gr; blad is grid-noord.
Bronresolutie 10 m (1 pixel). Sentinel-2 L2A wordt geleverd in WGS84/UTM 24S
(EPSG:32724); verschil met SIRGAS 2000 is < 0,1 m en verwaarloosbaar.
In Civil 3D nog te doen: drie herkenningspunten tegen Map Aerial
(GEOMAPIMAGE) meten en de afwijking in de maatstaat invullen.

Project	Havenontwerp Porto Central, Presidente Kennedy (ES) - Groep 1
Module	Atelier De Haven A │ NHL Stenden Civiele Techniek
Bladnaam	**Maatstaat, ankerpunten en georeferentie**
Status	**DEFINITIEF ONTWERP (DO)**
Blad / versie	DO-04 │ versie 7.0 │ 22-10-2026
Schaal	n.v.t. op A1 (841 × 594 mm)
Stelsel	SIRGAS 2000 / UTM zone 24S EPSG:31984 eenheid m
Hoogtedatum	diepten in m t.o.v. MLWS, voorlopig; MLWS-DHN te verifiëren
Kaartbron	Copernicus Sentinel-2 L2A (ESA), 03-07-2026, 10 m
	tegels 24KTB/24KUB, AWS Open Data COG; geraadpleegd 22-10-2026
Kustlijn	waterlijn 03-07-2026 uit NDWI (geen MLWS-lijn)
Bathymetrie	GEBCO 2026 (ca. 450 m) + Copernicus DEM 30 m; MSL→MLWS +0,7 m (aanname)
	geen lodingen: peiling (multibeam) nodig vóór uitvoering

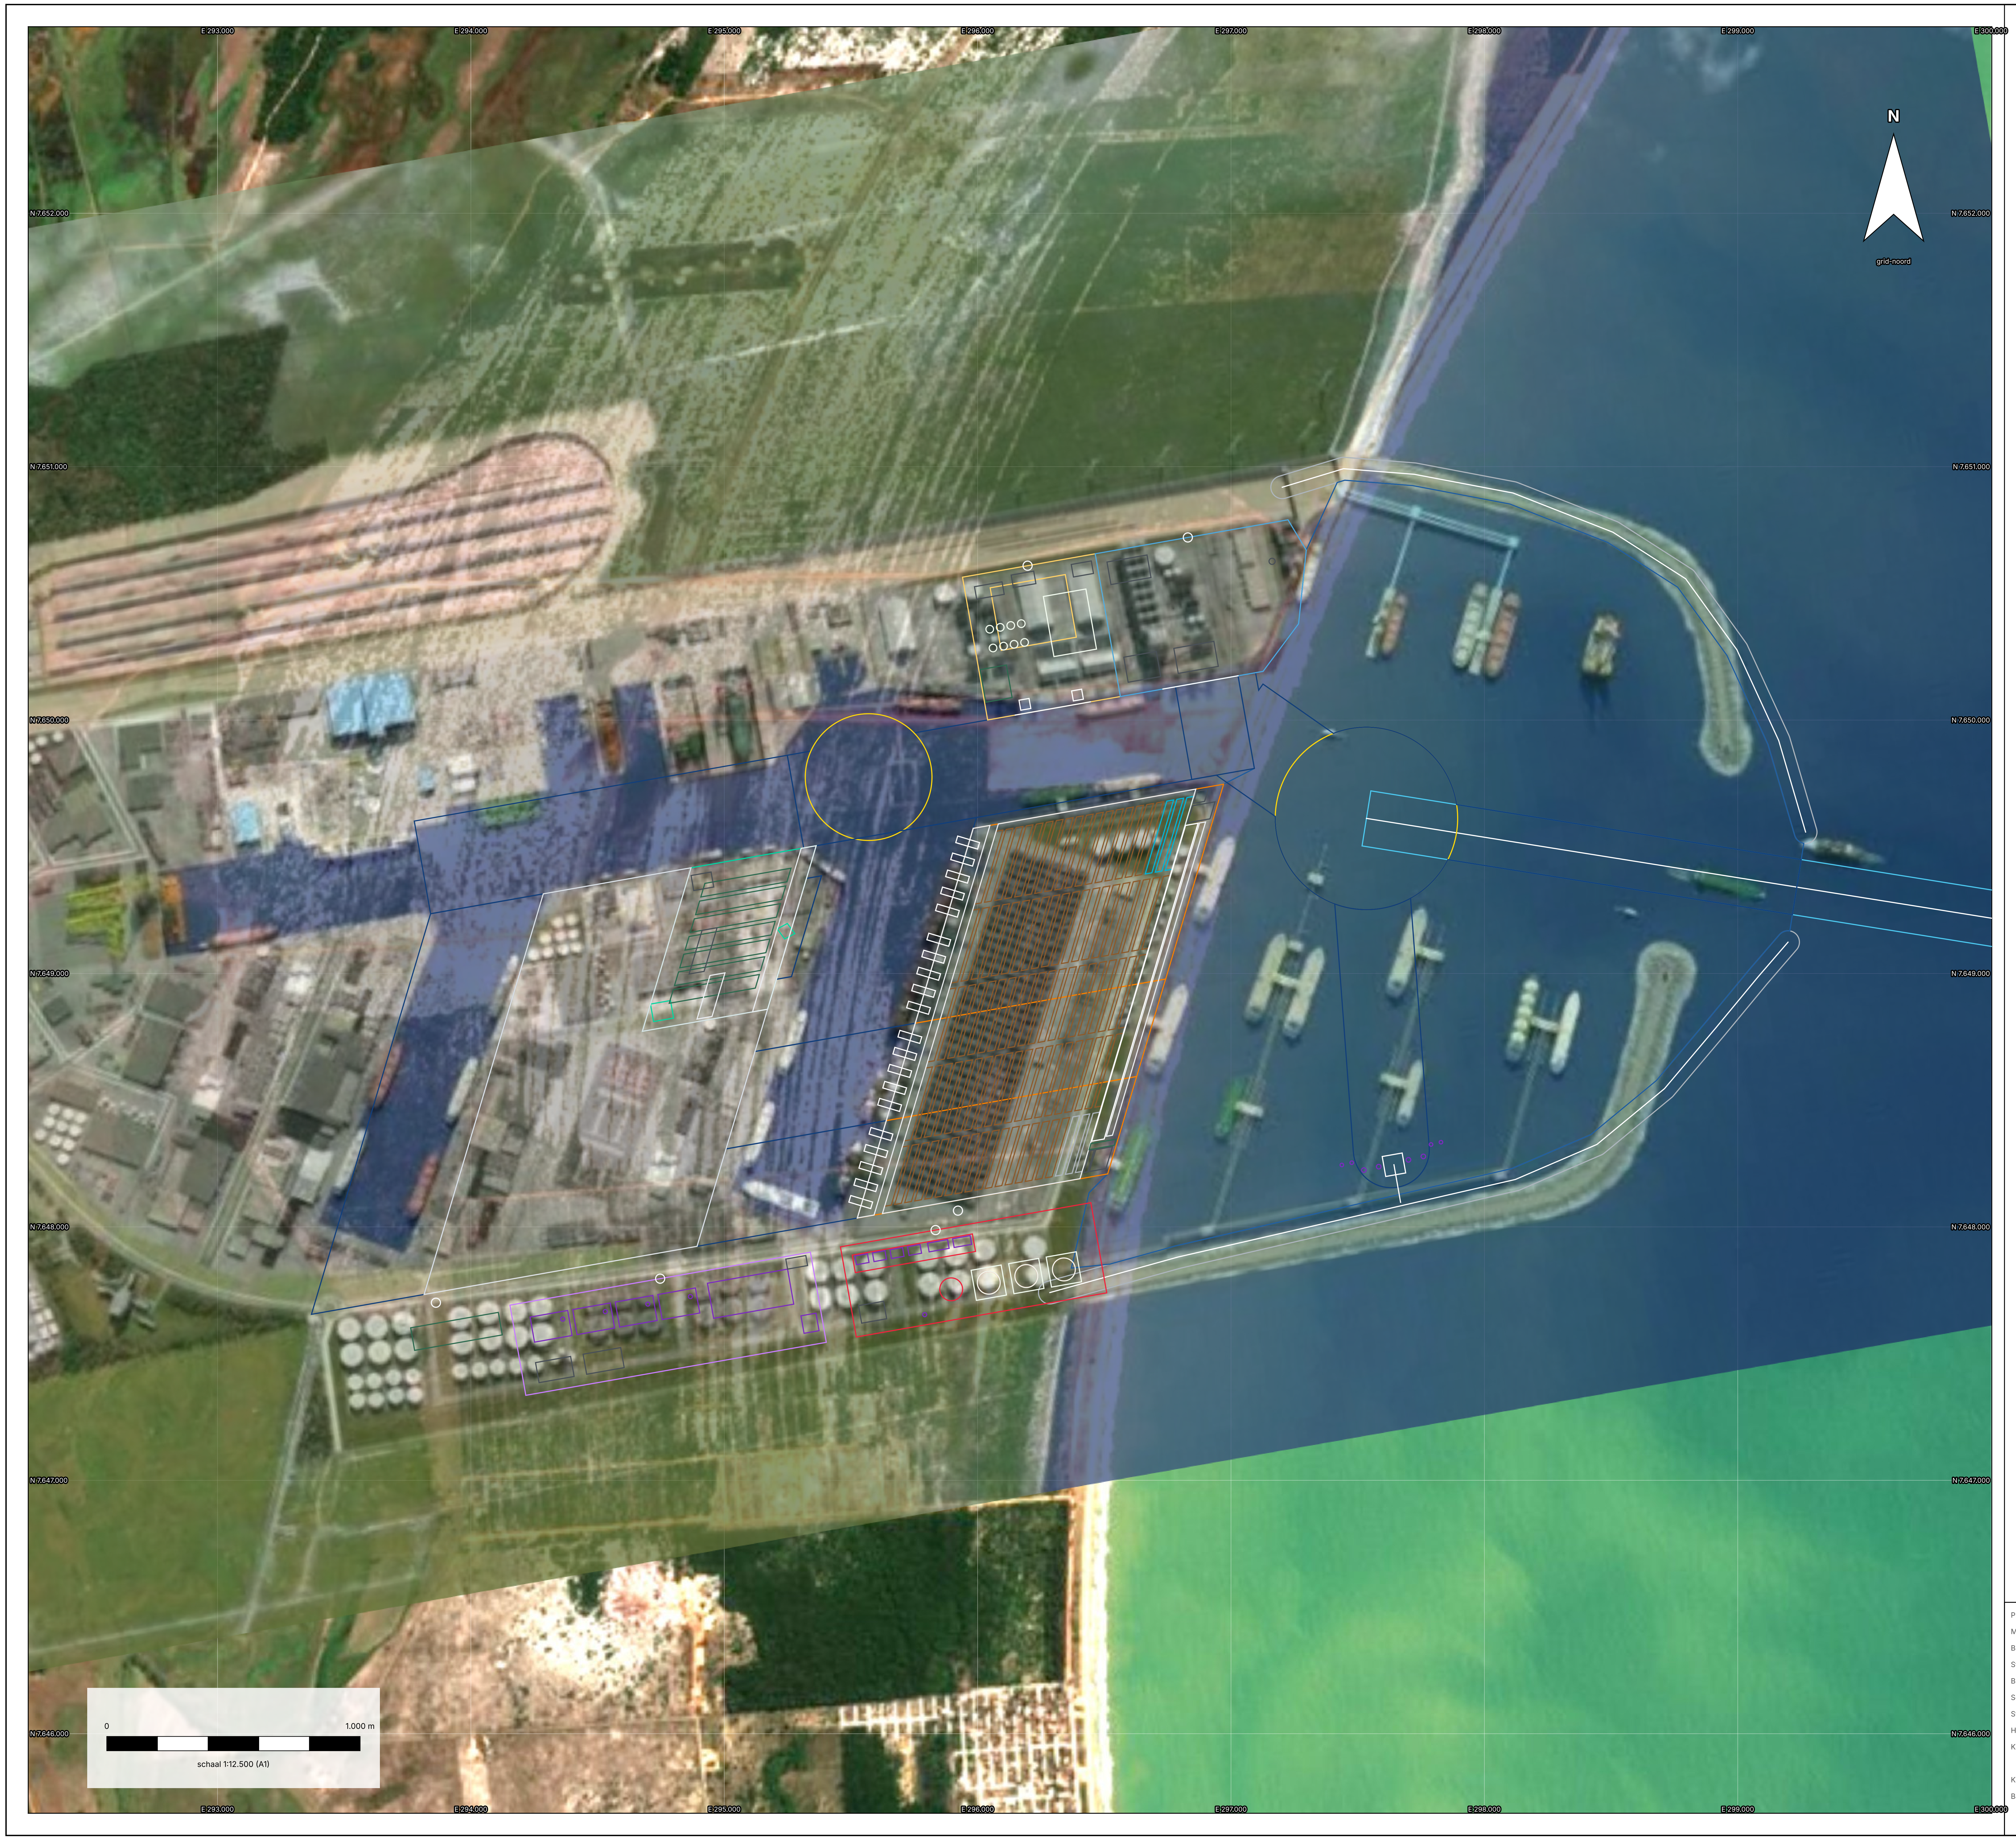

LEGENDA

▬	Waterlijn 3-7-2026 (NDWI, geen MLWS-lijn)
– –	Zoekgebied locatie B (indicatief)
■	Voorhaven binnen de dammen (strandwal ontgraven)
■	Gebaggerd tot -18,20 m MLWS (voorlopig)
▭	Geul 220 m bodembreedte
▭	Vrije draaikom D = 720 m
▭	Havenmond vrij 350 m
■	Golfbreker (footprint 90 m, voorlopig)
	Kade / steiger
■	Scheepsenveloppe aan ligplaats
■	Containerterminal
■	Graanterminal
■	RoRo / voertuigenterminal
■	LNG-steiger, tanks en hervergassing
■	Centrale + utilities (reservering)
■	Havendiensten, sleepboten, loodsen
▨	Reserveterrein / latere uitbreiding
▬	Hoofdweg + terminalinritten
- - -	Spoor
– – ·	LNG/gasleiding, koelwater (indicatief)
– – ·	Fasegrens 2025 / 2035 / 2045
▭	Sleepbootkoppelpunt
+	Ontwerpankerpunt (E/N in maatstaat)
– – ·	Veiligheidszone LNG 250 m / controlezone 500 m (indicatief)
▬	Dieptelijn t.o.v. MLWS (GEBCO 2026, indicatief)
□	Detail: apron, rijstroken, stackzone
■	Detail: stackblokken containers (RTG)
■	Detail: reefervakken
■	Detail: lege containers
□	Detail: kranen, kraanbanen, laadarmen
■	Detail: gebouwen
□	Detail: silo's, tanks, opslag
■	Detail: parkeervakken
■	Detail: installaties en dolphins

Controle overtrek

De render is op schaal en op de echte kust gelegd:
schaal 10,035 m per pixel, draaiing 10,0 gr;
kustlijn render tegen waterlijn: gem. 31 m.
Gekleurde lijnen = definitief ontwerp (DO).
Afwijkingen van de render zijn bewust:

- havenmond 350 m vrij (render ca. 640 m);
- alleen functies uit de opdracht: erts, werf, industrie en olie weggelaten;
- zwaaiplaats binnenhaven D 500 m (met sleepboten);
- containerkade aan de westzijde van vinger 6, in de insteek: beschut tegen golven (DO-09);
- LNG-steiger achter de zuidelijke dam, tanks oostelijk in de zone: kortere cryogene leiding;
- maten volgen het rekenboek.

In de DXF staat de render op laag HV-REFERENTIE (uit); aanzetten om zelf verder over te trekken.

Project	Havenontwerp Porto Central, Presidente Kennedy (ES) - Groep 1
Module	Atelier De Haven A | NHL Stenden Civiele Techniek
Bladnaam	**Overtrek Porto Central-render op luchtfoto**
Status	**DEFINITIEF ONTWERP (DO)**
Blad / versie	DO-05 | versie 7.0 | 22-10-2026
Schaal	1:12.500 op A1 (841 × 594 mm)
Stelsel	SIRGAS 2000 / UTM zone 24S EPSG:31984 eenheid m
Hoogtedatum	diepten in m t.o.v. MLWS, voorlopig; MLWS-DHN te verifiëren
Kaartbron	Copernicus Sentinel-2 L2A (ESA), 03-07-2026, 10 m
	tegels 24KTB/24KUB, AWS Open Data COG; geraadpleegd 22-10-2026
Kustlijn	waterlijn 03-07-2026 uit NDWI (geen MLWS-lijn)
Bathymetrie	GEBCO 2026 (ca. 450 m) + Copernicus DEM 30 m; MSL→MLWS +0,7 m (aanname)
	geen lodingen: peiling (multibeam) nodig vóór uitvoering

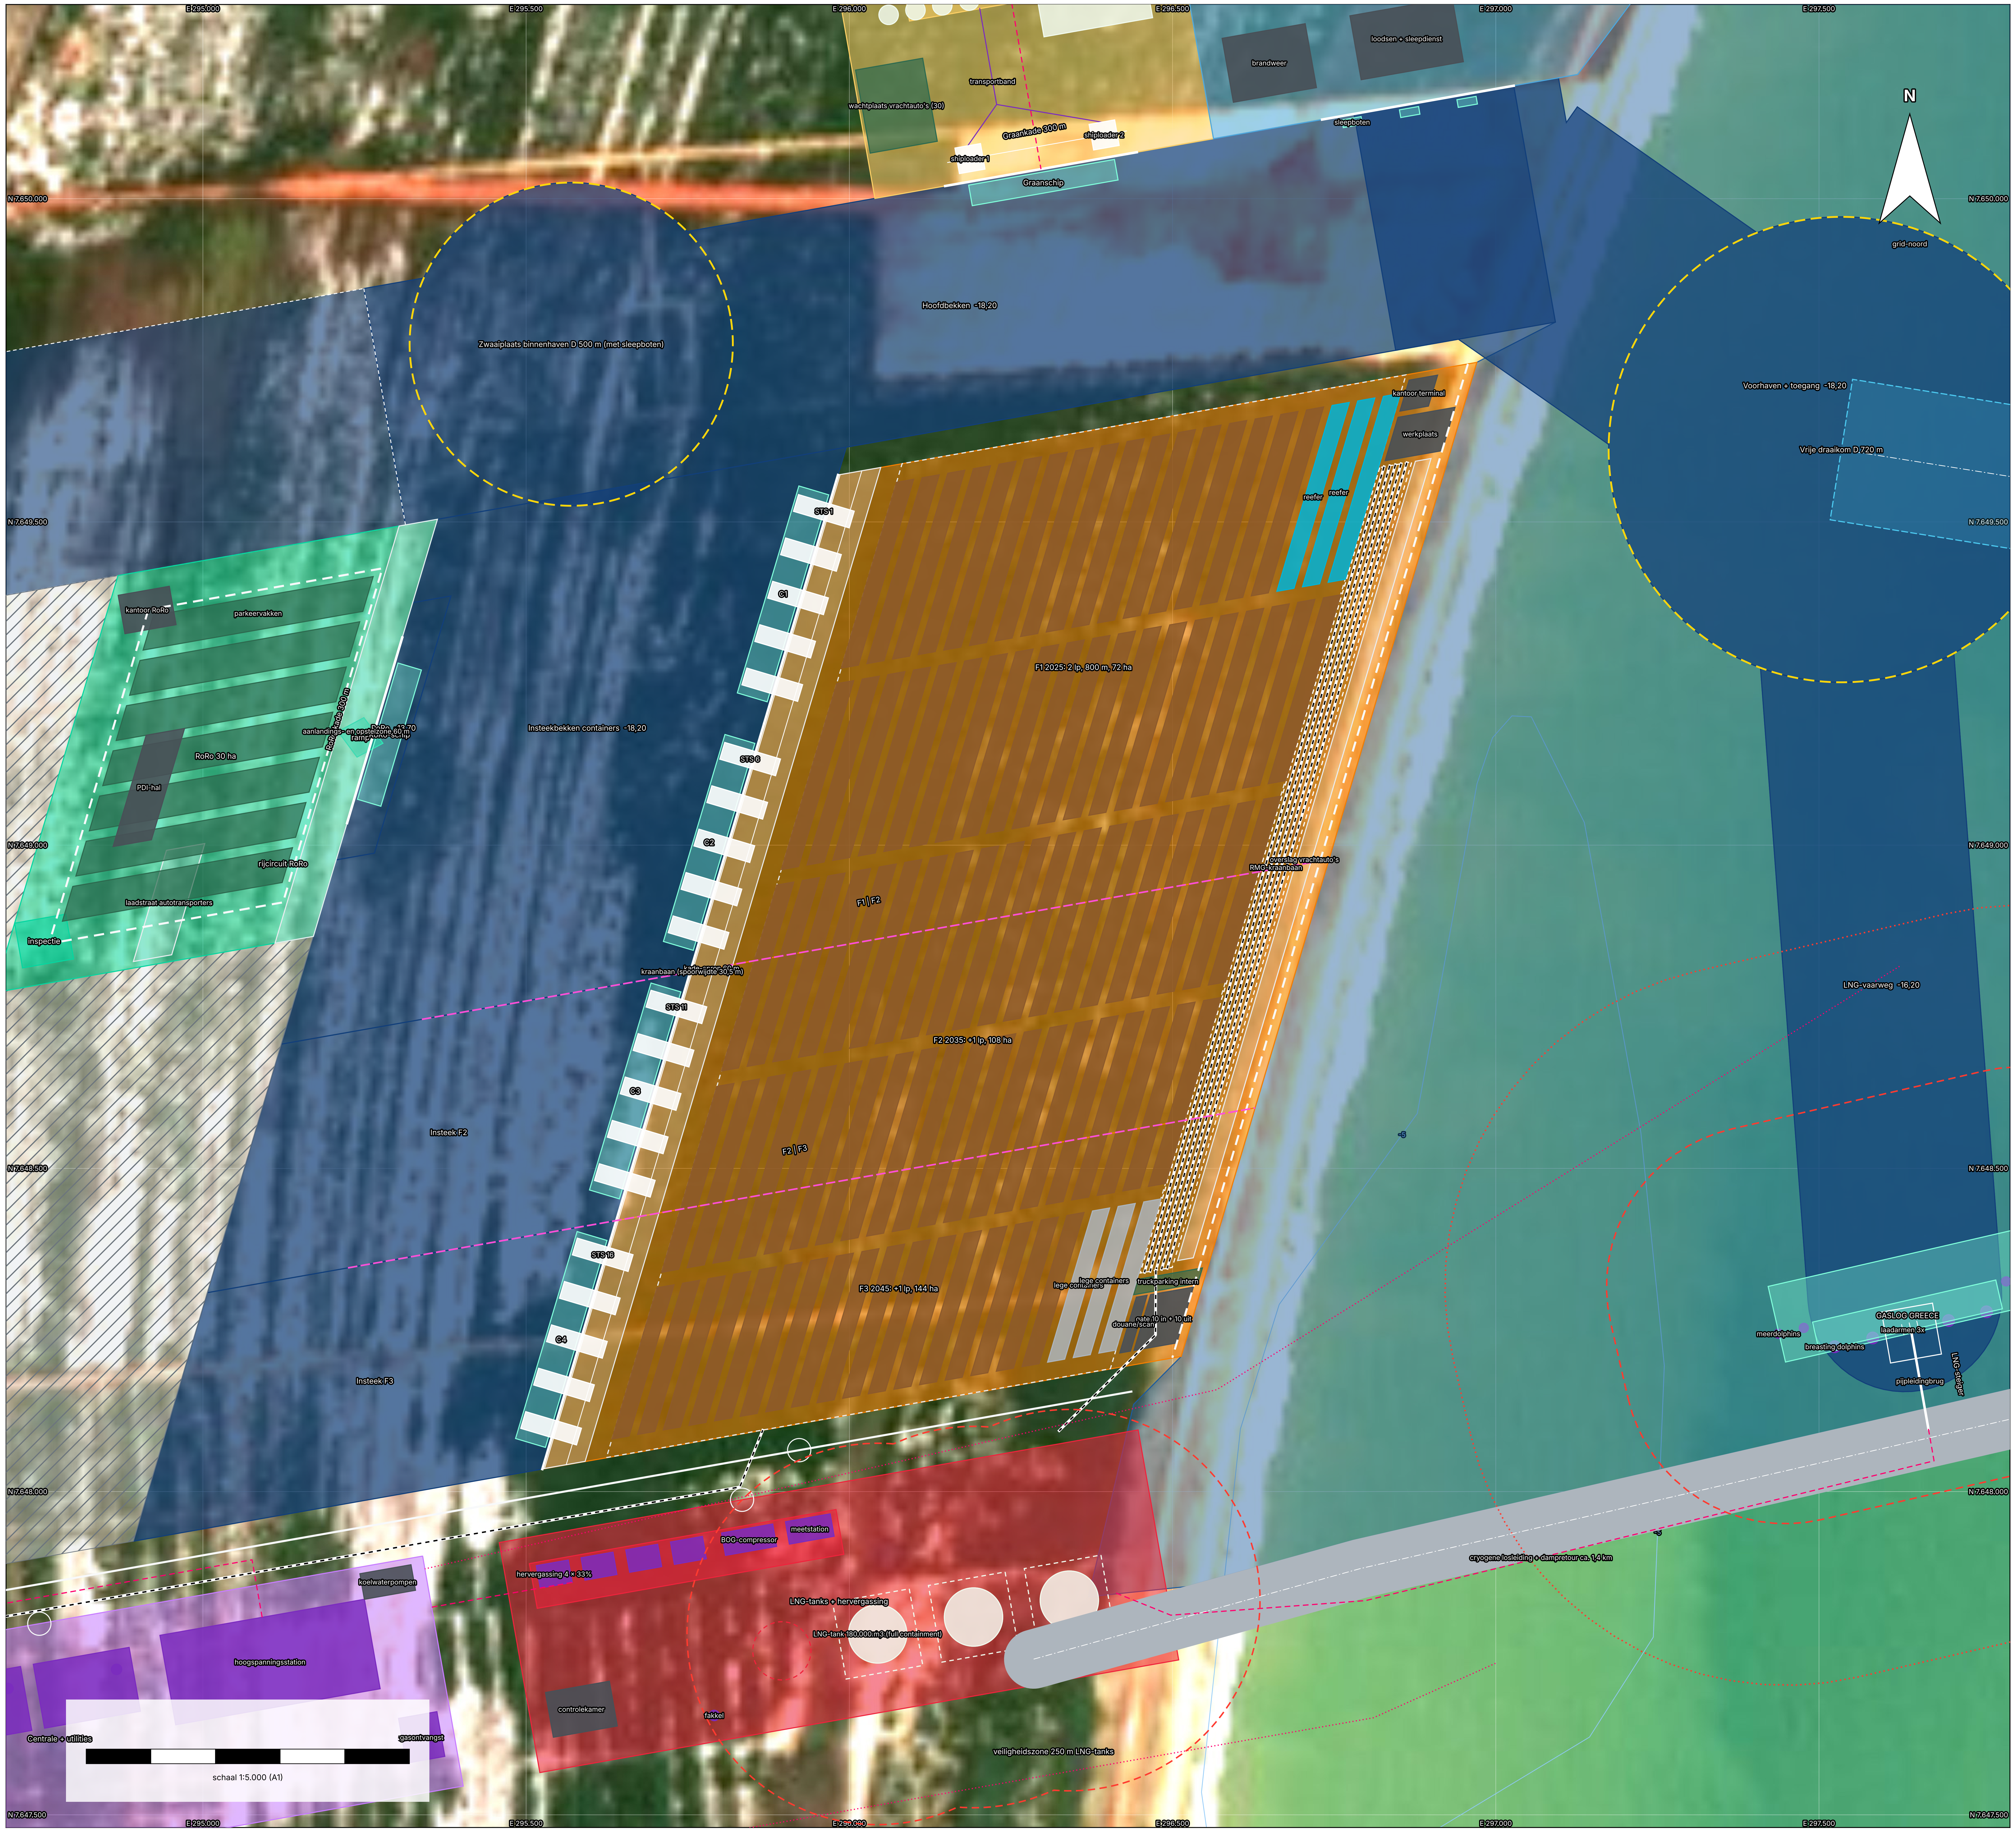

LEGENDA

—	Waterlijn 3-7-2026 (NDWI, geen MLWS-lijn)
- -	Zoekgebied locatie B (indicatief)
■	Voorhaven binnen de dammen (strandwal ontgraven)
■	Gebaggerd tot -18,20 m MLWS (voorlopig)
⬚	Geul 220 m bodembreedte
⬚	Vrije draaikom D = 720 m
⬚	Havenmond vrij 350 m
■	Golfbreker (footprint 90 m, voorlopig)
	Kade / steiger
■	Scheepsenveloppe aan ligplaats
■	Containerterminal
■	Graanterminal
■	RoRo / voertuigenterminal
■	LNG-steiger, tanks en hervergassing
■	Centrale + utilities (reservering)
■	Havendiensten, sleepboten, loodsen
▨	Reserveterrein / latere uitbreiding
—	Hoofdweg + terminalinritten
- - -	Spoor
- - ·	LNG/gasleiding, koelwater (indicatief)
- - ·	Fasegrens 2025 / 2035 / 2045
⬚	Sleepbootkoppelpunt
+	Ontwerpankerpunt (E/N in maatstaat)
- - ·	Veiligheidszone LNG 250 m / controlezone 500 m (indicatief)
—	Dieptelijn t.o.v. MLWS (GEBCO 2026, indicatief)
□	Detail: apron, rijstroken, stackzone
■	Detail: stackblokken containers (RTG)
■	Detail: reefervakken
■	Detail: lege containers
□	Detail: kranen, kraanbanen, laadarmen
■	Detail: gebouwen
□	Detail: silo's, tanks, opslag
■	Detail: parkeervakken
■	Detail: installaties en dolphins

Overslagketen containers
schip → STS-kraan → terminaltrekker → RTG-stack
Kade aan de westzijde van vinger 6 (insteek): Hs < 0,1 m
→ vrachtauto (gate) of trein (RMG-railterminal)
Kade: 5 STS x 30 box/u = 150 box/u per schip; apron 60 m
STS-kranen F1/F2/F3: 6 / 12 / 20 (6 / 12 / 20)
Stack: TEU-grondslots 20.284 / 30.426 / 40.558
benodigd 12.133 / 20.222 / 40.444 (28 m2/slot)
Landzijde 2045 (aannamen: 70% weg, 30% spoor)
Piekuur 527 truckbezoeken (10% van piekdag)
→ 9 rijstroken per richting nodig; getekend
10 in + 10 uit (60 trucks/u/rijstrook)
Pre-gate buffer 30 min = 264 trucks = 2,6 ha;
getekend 3,2 ha aan de ringweg
Spoor: 32,6 treinen/piekdag; 5 sporen x 1.300 m =
10 treinposities x 4 = 40 treinen/dag (6 u per trein)
Reefer- en legecontainervakken aan de landzijde

Project	Havenontwerp Porto Central, Presidente Kennedy (ES) - Groep 1
Module	Atelier De Haven A | NHL Stenden Civiele Techniek
Bladnaam	**Containerterminal**
Status	**DEFINITIEF ONTWERP (DO)**
Blad / versie	DO-06 | versie 7.0 | 22-10-2026
Schaal	1:5.000 op A1 (841 × 594 mm)
Stelsel	SIRGAS 2000 / UTM zone 24S EPSG:31984 eenheid m
Hoogtedatum	diepten in m t.o.v. MLWS, voorlopig; MLWS-DHN te verifiëren
Kaartbron	Copernicus Sentinel-2 L2A (ESA), 03-07-2026, 10 m
	tegels 24KTB/24KUB, AWS Open Data COG; geraadpleegd 22-10-2026
Kustlijn	waterlijn 03-07-2026 uit NDWI (geen MLWS-lijn)
Bathymetrie	GEBCO 2026 (ca. 450 m) + Copernicus DEM 30 m; MSL→MLWS +0,7 m (aanname)
	geen lodingen: peiling (multibeam) nodig vóór uitvoering

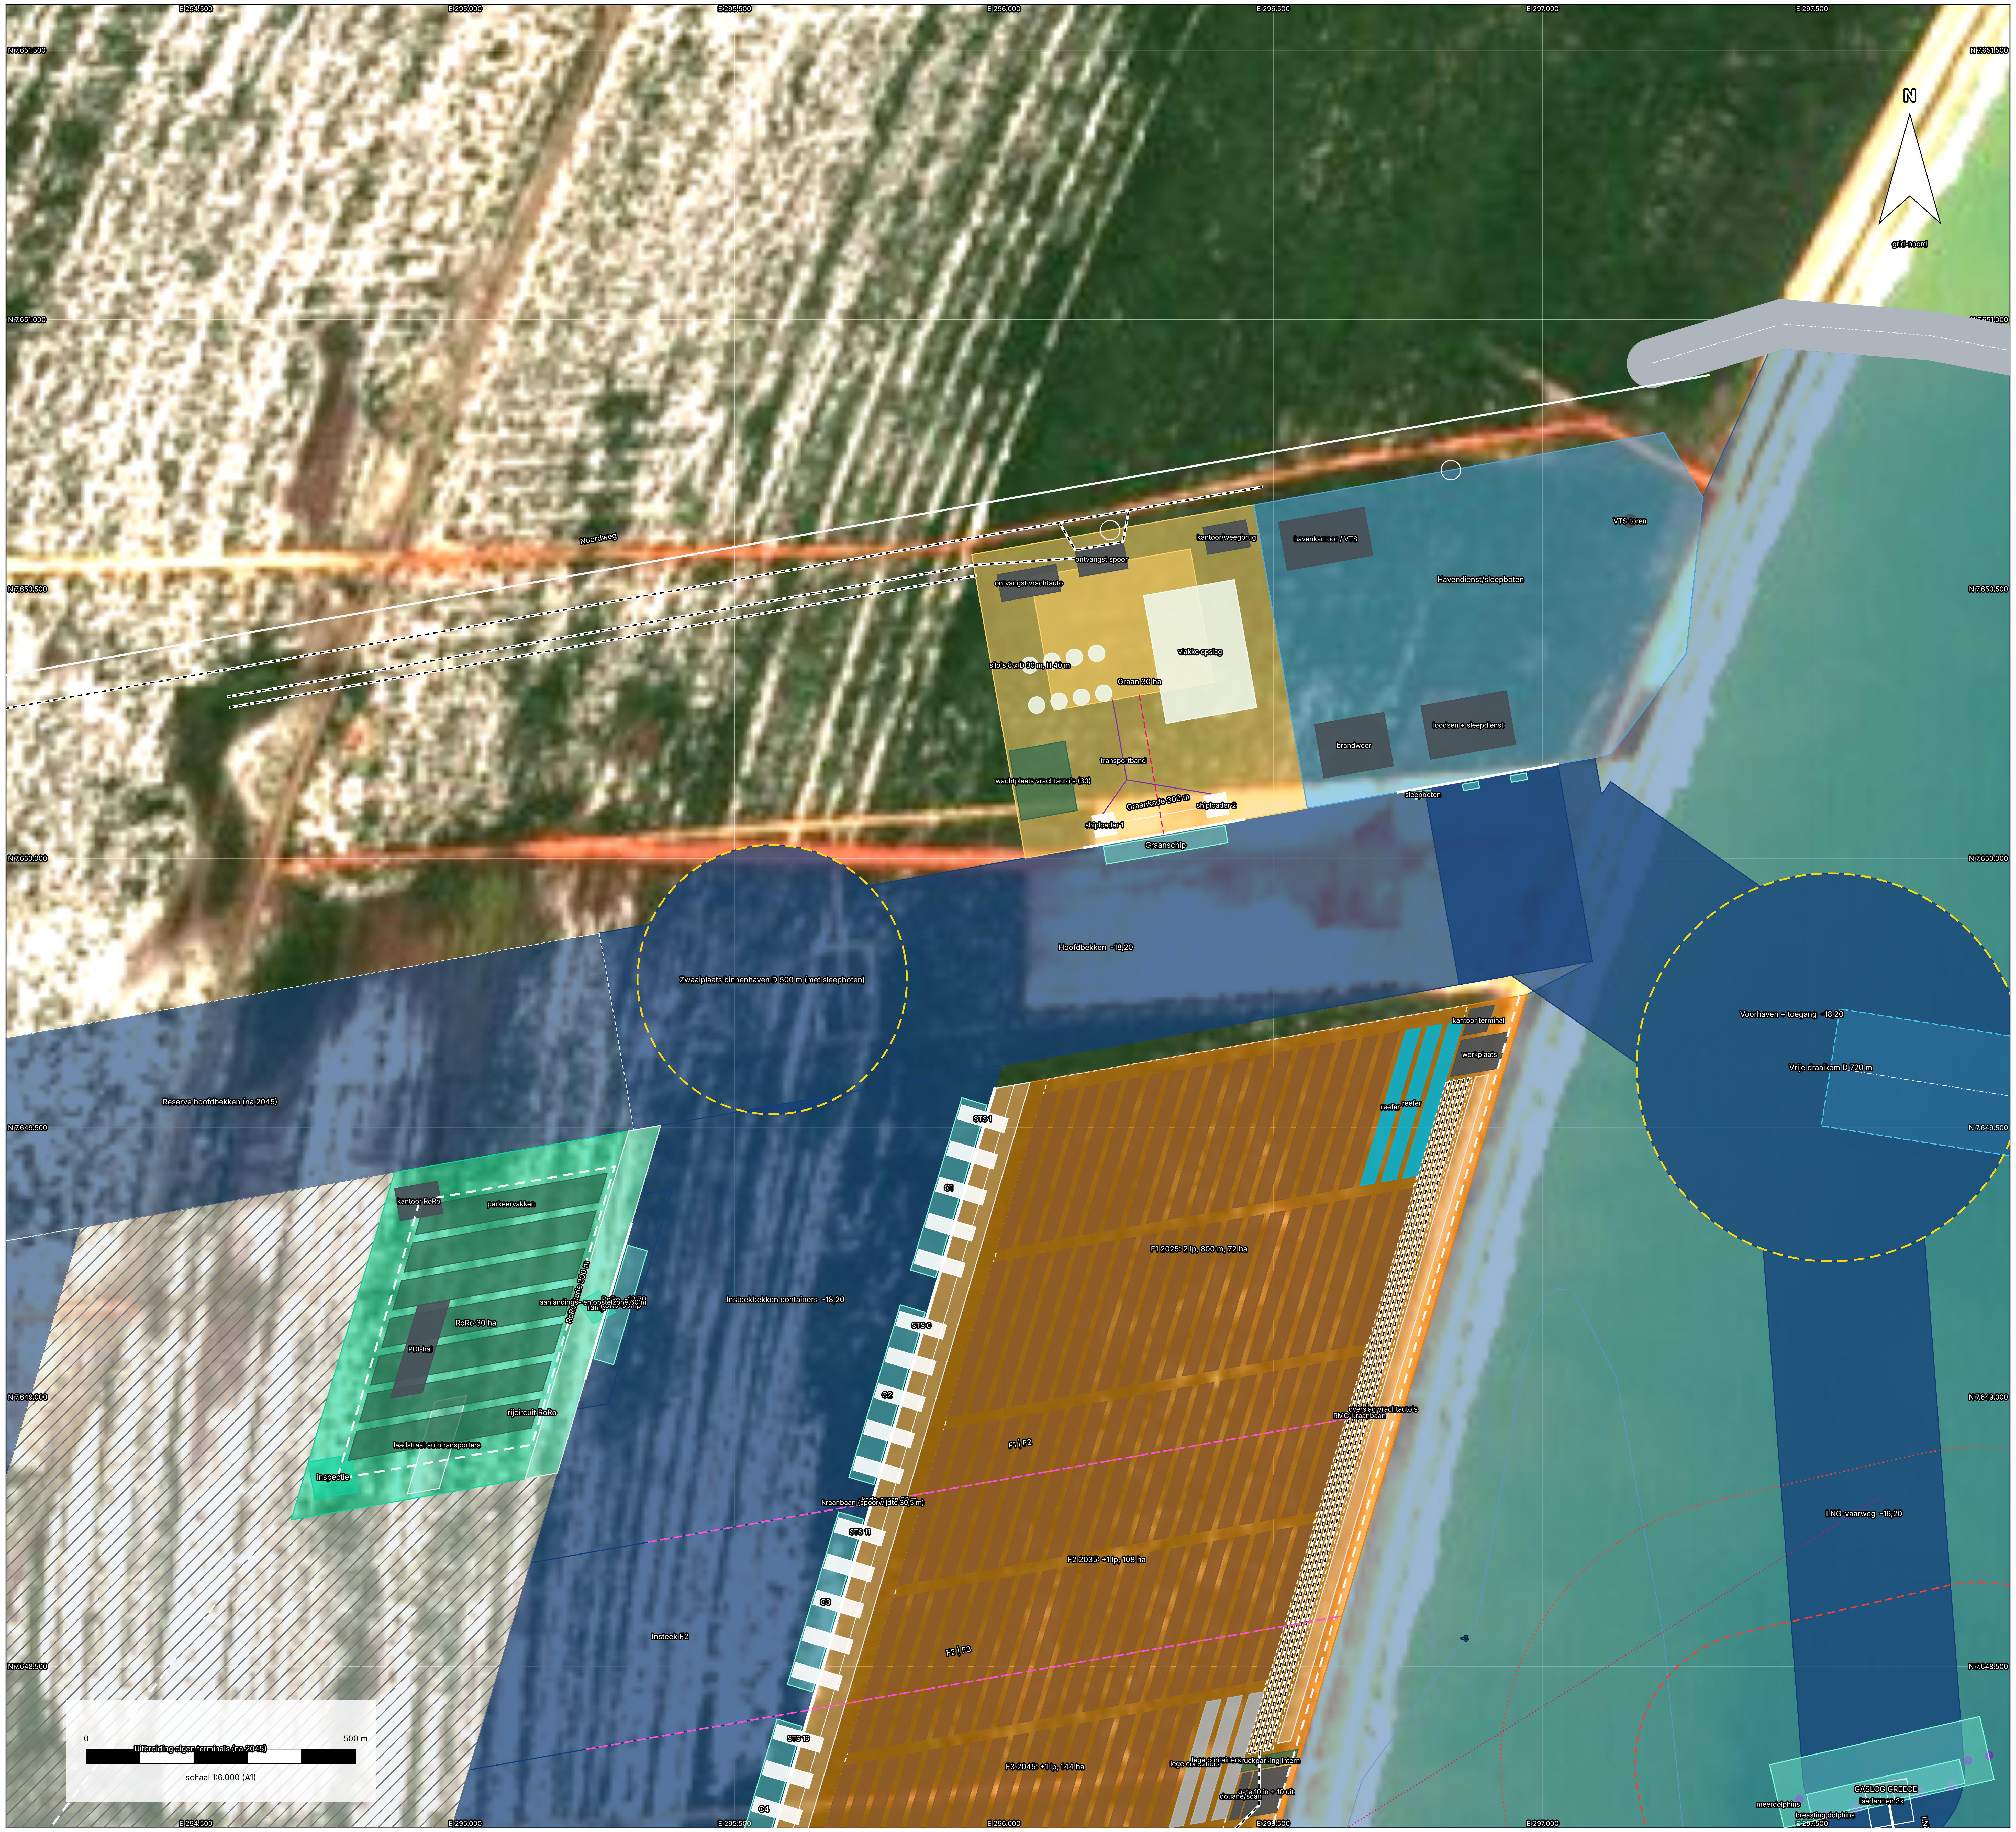

LEGENDA

━	Waterlijn 3-7-2026 (NDWI, geen MLWS-lijn)
╌	Zoekgebied locatie B (indicatief)
■	Voorhaven binnen de dammen (strandwal ontgraven)
■	Gebaggerd tot -18,20 m MLWS (voorlopig)
⬚	Geul 220 m bodembreedte
⬚	Vrije draaikom D = 720 m
⬚	Havenmond vrij 350 m
■	Golfbreker (footprint 90 m, voorlopig)
	Kade / steiger
□	Scheepsenveloppe aan ligplaats
■	Containerterminal
□	Graanterminal
■	RoRo / voertuigenterminal
■	LNG-steiger, tanks en hervergassing
■	Centrale + utilities (reservering)
■	Havendiensten, sleepboten, loodsen
▨	Reserveterrein / latere uitbreiding
━	Hoofdweg + terminalinritten
╌	Spoor
╌	LNG/gasleiding, koelwater (indicatief)
╌	Fasegrens 2025 / 2035 / 2045
⬚	Sleepbootkoppelpunt
+	Ontwerpankerpunt (E/N in maatstaat)
╌	Veiligheidszone LNG 250 m / controlezone 500 m (indicatief)
━	Dieptelijn t.o.v. MLWS (GEBCO 2026, indicatief)
□	Detail: apron, rijstroken, stackzone
■	Detail: stackblokken containers (RTG)
■	Detail: reefervakken
■	Detail: lege containers
□	Detail: kranen, kraanbanen, laadarmen
■	Detail: gebouwen
□	Detail: silo's, tanks, opslag
■	Detail: parkeervakken
■	Detail: installaties en dolphins

Graan (export): weg/spoor → stortput → silo →
transportband → shiploader → schip
Piekdag oogst 7.500 t (15% van jaar in een maand)
50% per vrachtauto = 101 trucks/dag;
wachtplaats 4 u = 26 trucks (getekend 30)
50% per spoor = 3,5 treinen/week van 1.400 m
→ 2 opstelsporen x 1.400 m langs de noordweg
Silo's 169.646 t (piek 154.100 t); 2 shiploaders
RoRo (import): schip → ramp → opstelzone → PDI
→ parkeervak → laadstraat autotransporters
Lossen 6.500 auto's / 150 per u = 43,3 u; ca. 20 chauffeurs
Parkeervakken ca. 9.698 auto's (piek 7.479)
Autotransporters (8 auto's): ca. 93 per piekdag
Havendienst: VTS, loodsen, 3 sleepboten, brandweer

Project	Havenontwerp Porto Central, Presidente Kennedy (ES) - Groep 1
Module	Atelier De Haven A | NHL Stenden Civiele Techniek
Bladnaam	**Graan, RoRo en havendienst**
Status	**DEFINITIEF ONTWERP (DO)**
Blad / versie	DO-07 | versie 7.0 | 22-10-2026
Schaal	1:6.000 op A1 (841 × 594 mm)
Stelsel	SIRGAS 2000 / UTM zone 24S EPSG:31984 eenheid m
Hoogtedatum	diepten in m t.o.v. MLWS, voorlopig; MLWS-DHN te verifiëren
Kaartbron	Copernicus Sentinel-2 L2A (ESA), 03-07-2026, 10 m tegels 24KTB/24KUB, AWS Open Data COG; geraadpleegd 22-10-2026
Kustlijn	waterlijn 03-07-2026 uit NDWI (geen MLWS-lijn)
Bathymetrie	GEBCO 2026 (ca. 450 m) + Copernicus DEM 30 m; MSL→MLWS +0,7 m (aanname) geen lodingen: peiling (multibeam) nodig vóór uitvoering

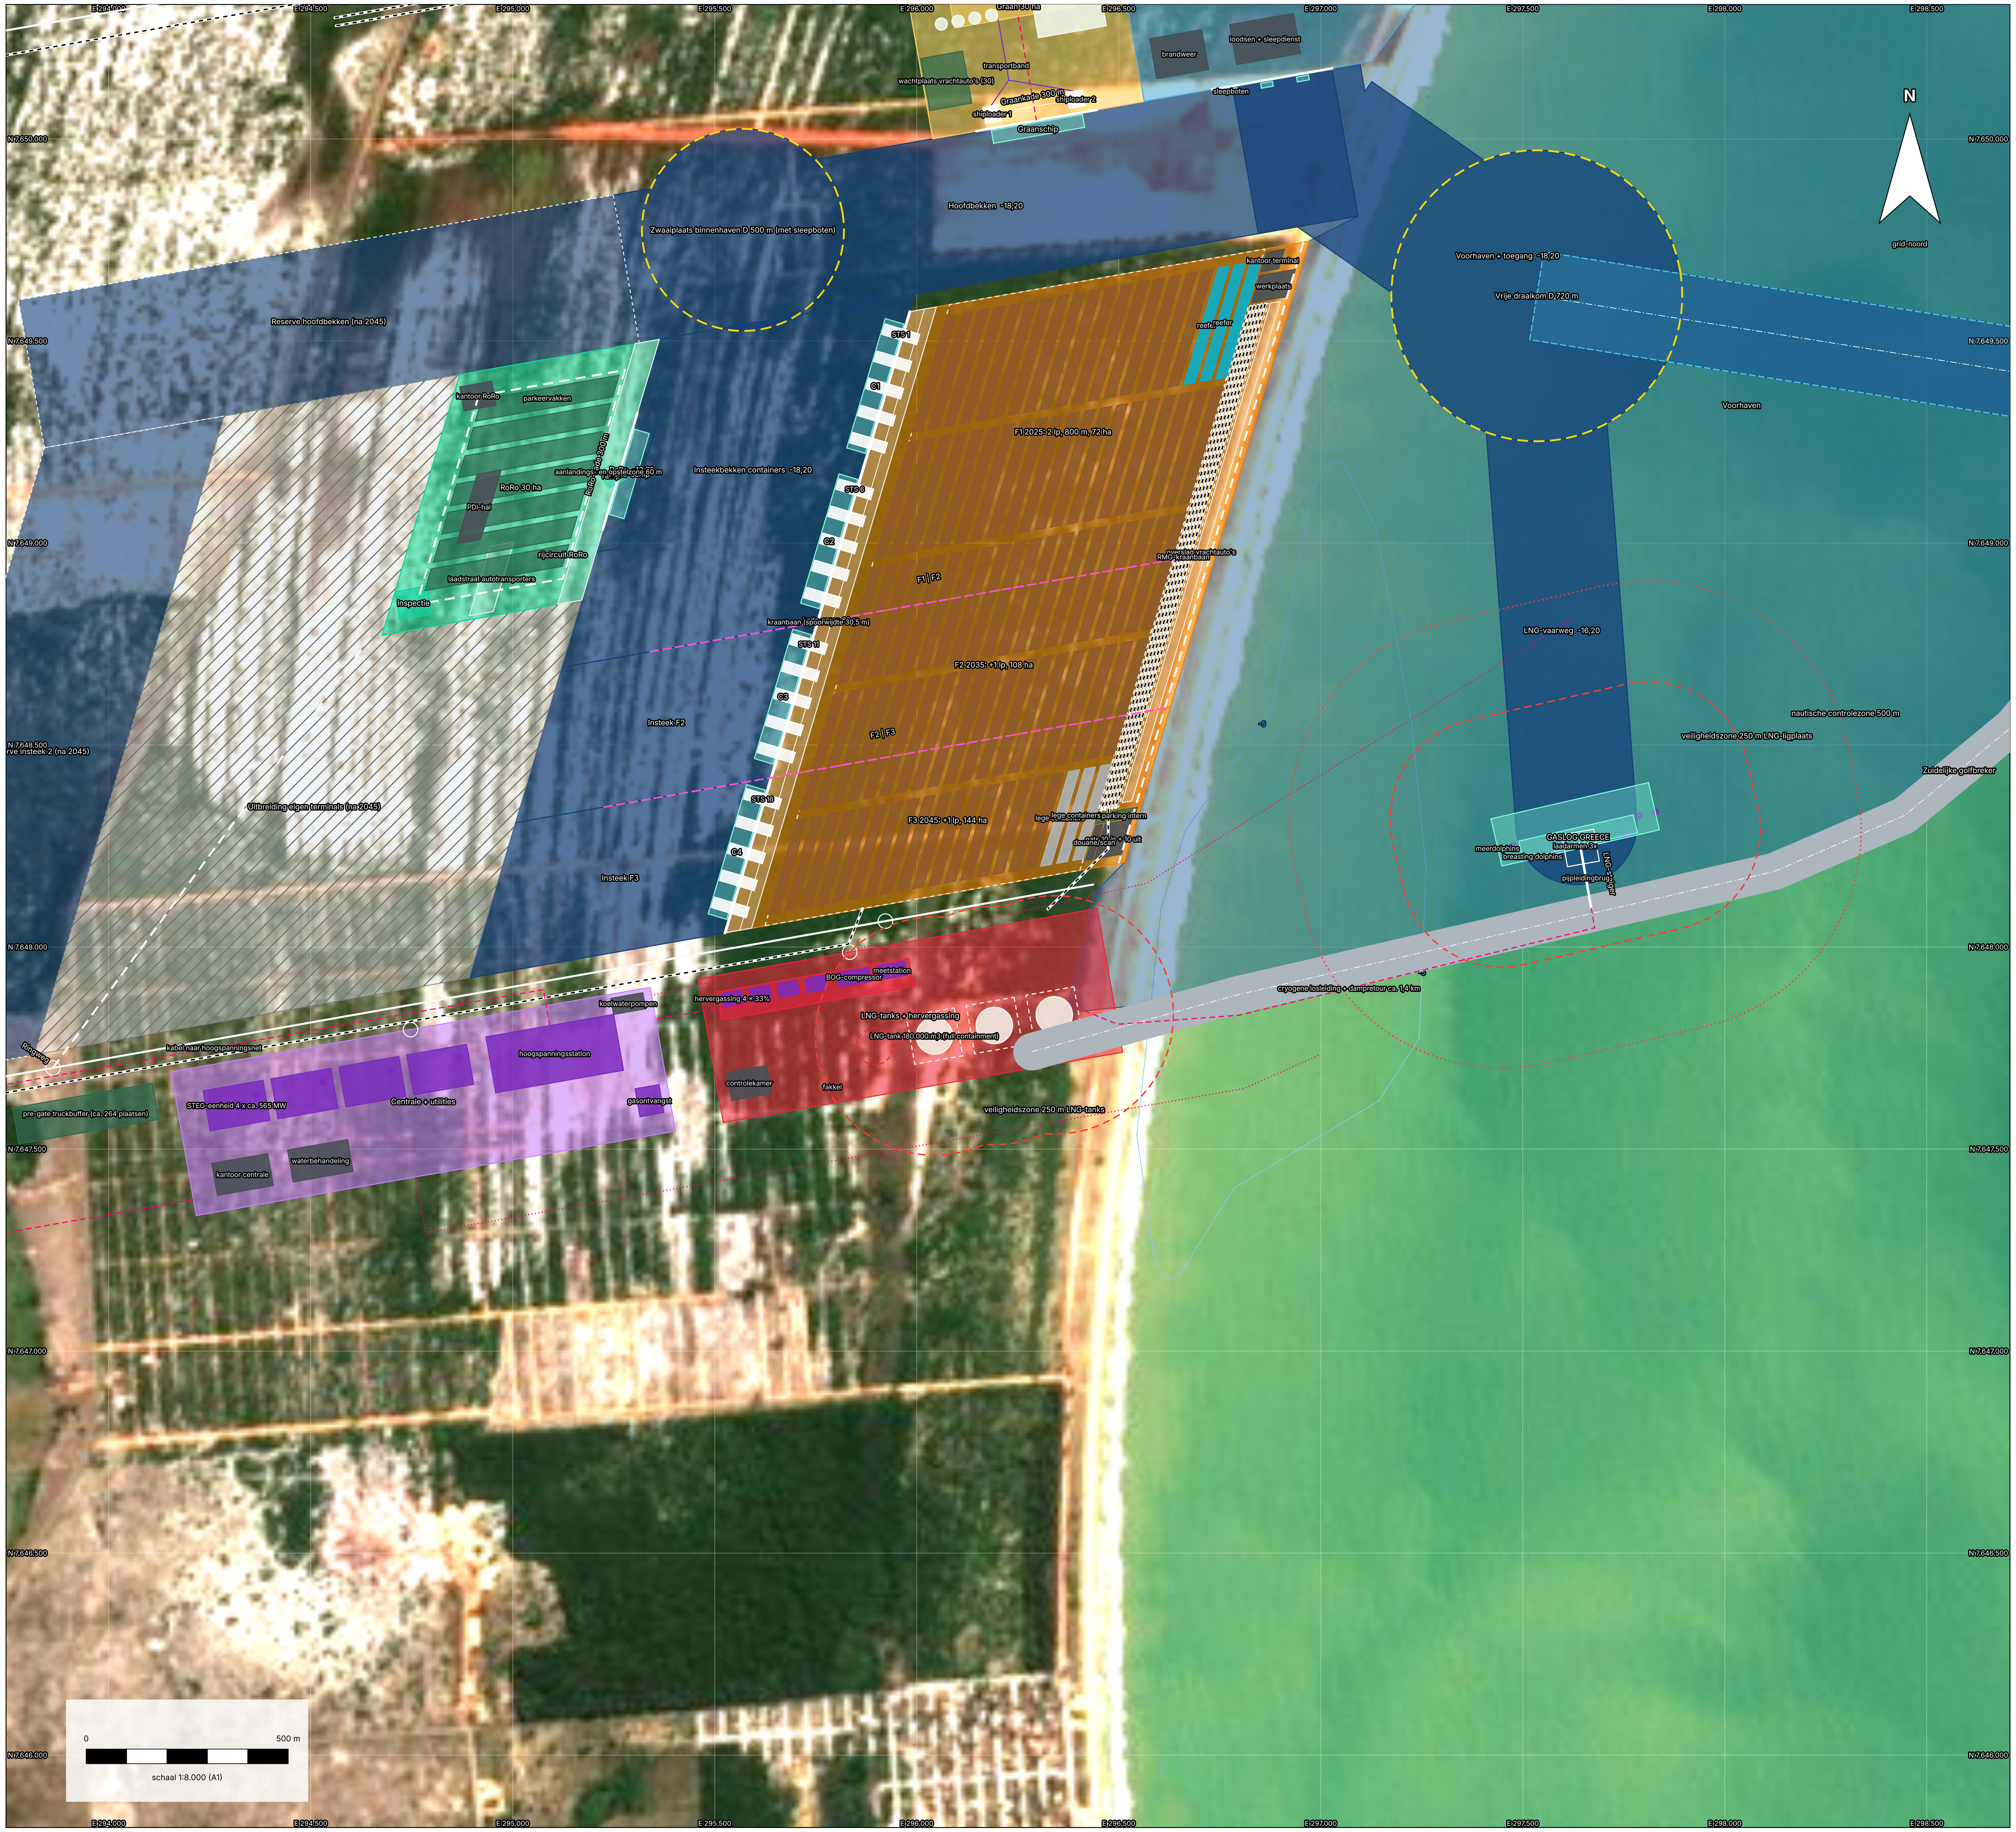

LEGENDA

- — Waterlijn 3-7-2026 (NDWI, geen MLWS-lijn)
- - - Zoekgebied locatie B (indicatief)
- ■ Voorhaven binnen de dammen (strandwal ontgraven)
- ■ Gebaggerd tot -18,20 m MLWS (voorlopig)
- ⬚ Geul 220 m bodembreedte
- ⬚ Vrije draaikom D = 720 m
- ⬚ Havenmond vrij 350 m
- ■ Golfbreker (footprint 90 m, voorlopig)
- Kade / steiger
- ■ Scheepsenveloppe aan ligplaats
- ■ Containerterminal
- ■ Graanterminal
- ■ RoRo / voertuigenterminal
- ■ LNG-steiger, tanks en hervergassing
- ■ Centrale + utilities (reservering)
- ■ Havendiensten, sleepboten, loodsen
- ▨ Reserveterrein / latere uitbreiding
- — Hoofdweg + terminalinritten
- - - Spoor
- - - LNG/gasleiding, koelwater (indicatief)
- - - Fasegrens 2025 / 2035 / 2045
- ⬚ Sleepbootkoppelpunt
- + Ontwerpankerpunt (E/N in maatstaat)
- - - Veiligheidszone LNG 250 m / controlezone 500 m (indicatief)
- — Dieptelijn t.o.v. MLWS (GEBCO 2026, indicatief)
- ■ Detail: apron, rijstroken, stackzone
- ■ Detail: stackblokken containers (RTG)
- ■ Detail: reefervakken
- ■ Detail: lege containers
- □ Detail: kranen, kraanbanen, laadarmen
- ■ Detail: gebouwen
- ■ Detail: silo's, tanks, opslag
- ■ Detail: parkeervakken
- ■ Detail: installaties en dolphins

LNG: schip → laadarmen → cryogene leiding
→ tanks → hervergassing → centrale / gasnet
Lossen 156.600 m3 / 10.000 m3/u + 8 u = 23,7 u per call
Steiger achter de zuidelijke dam (Hs 0,9 m < 1,0 m);
ligplaats -16,20 m MLWS (diepgang 12,5 + 3,7 m)
3 laadarmen; losleiding + dampretour ca. 1,4 km
(tanks oostelijk in de zone geplaatst)
Tanks 3 × 180.000 m3 in tankput, ruimte 4e tank

Veiligheid (indicatief, QRA volgt)
250 m veiligheidszone rond schip/steiger en tanks;
500 m nautische controlezone; geen andere
schepen of gebouwen binnen de 250 m-zones
Send-out gemiddeld 913 m3 LNG/u; hervergassing 4 × 33%
Fakkel, BOG-compressor, meetstation, controlekamer
Centrale: 4 STEG-eenheden ca. 565 MW = 2.260 MW
(rekenvoorbeeld 2.256 MW), hoogspanningsstation,
koelwaterpompen, gasontvangst

Project	Havenontwerp Porto Central, Presidente Kennedy (ES) - Groep 1
Module	Atelier De Haven A | NHL Stenden Civiele Techniek
Bladnaam	**LNG-terminal en centrale**
Status	**DEFINITIEF ONTWERP (DO)**
Blad / versie	DO-08 | versie 7.0 | 22-10-2026
Schaal	1:8.000 op A1 (841 × 594 mm)
Stelsel	SIRGAS 2000 / UTM zone 24S EPSG:31984 eenheid m
Hoogtedatum	diepten in m t.o.v. MLWS, voorlopig; MLWS-DHN te verifiëren
Kaartbron	Copernicus Sentinel-2 L2A (ESA), 03-07-2026, 10 m tegels 24KTB/24KUB, AWS Open Data COG; geraadpleegd 22-10-2026
Kustlijn	waterlijn 03-07-2026 uit NDWI (geen MLWS-lijn)
Bathymetrie	GEBCO 2026 (ca. 450 m) + Copernicus DEM 30 m; MSL→MLWS +0,7 m (aanname) geen lodingen: peiling (multibeam) nodig vóór uitvoering

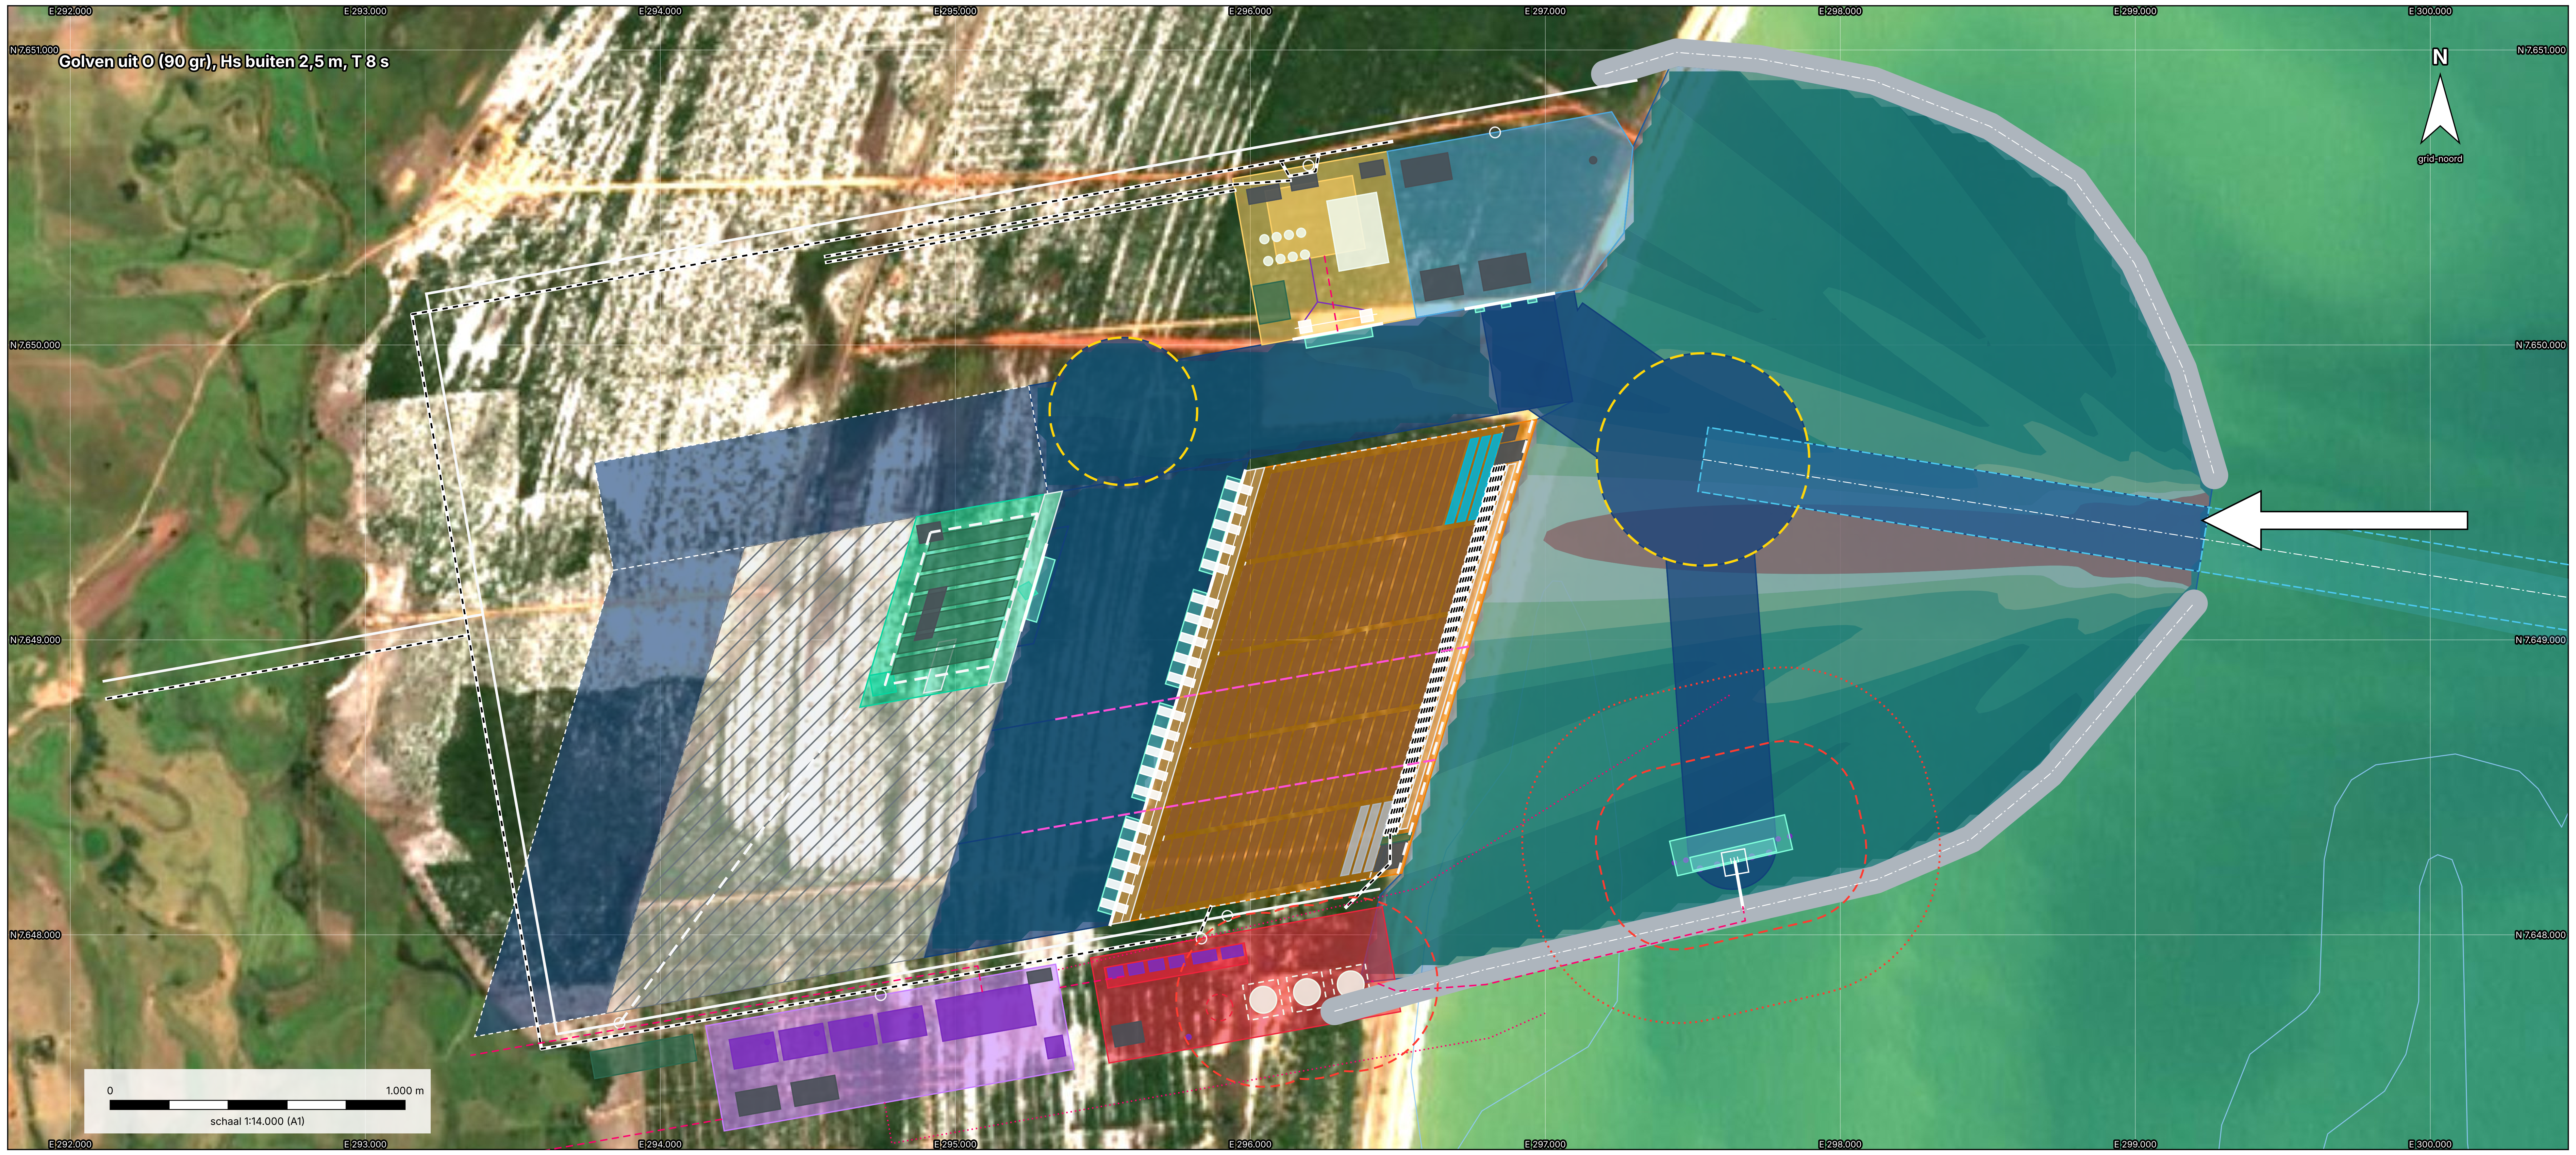
Golven uit O (90 gr), Hs buiten 2,5 m, T 8 s

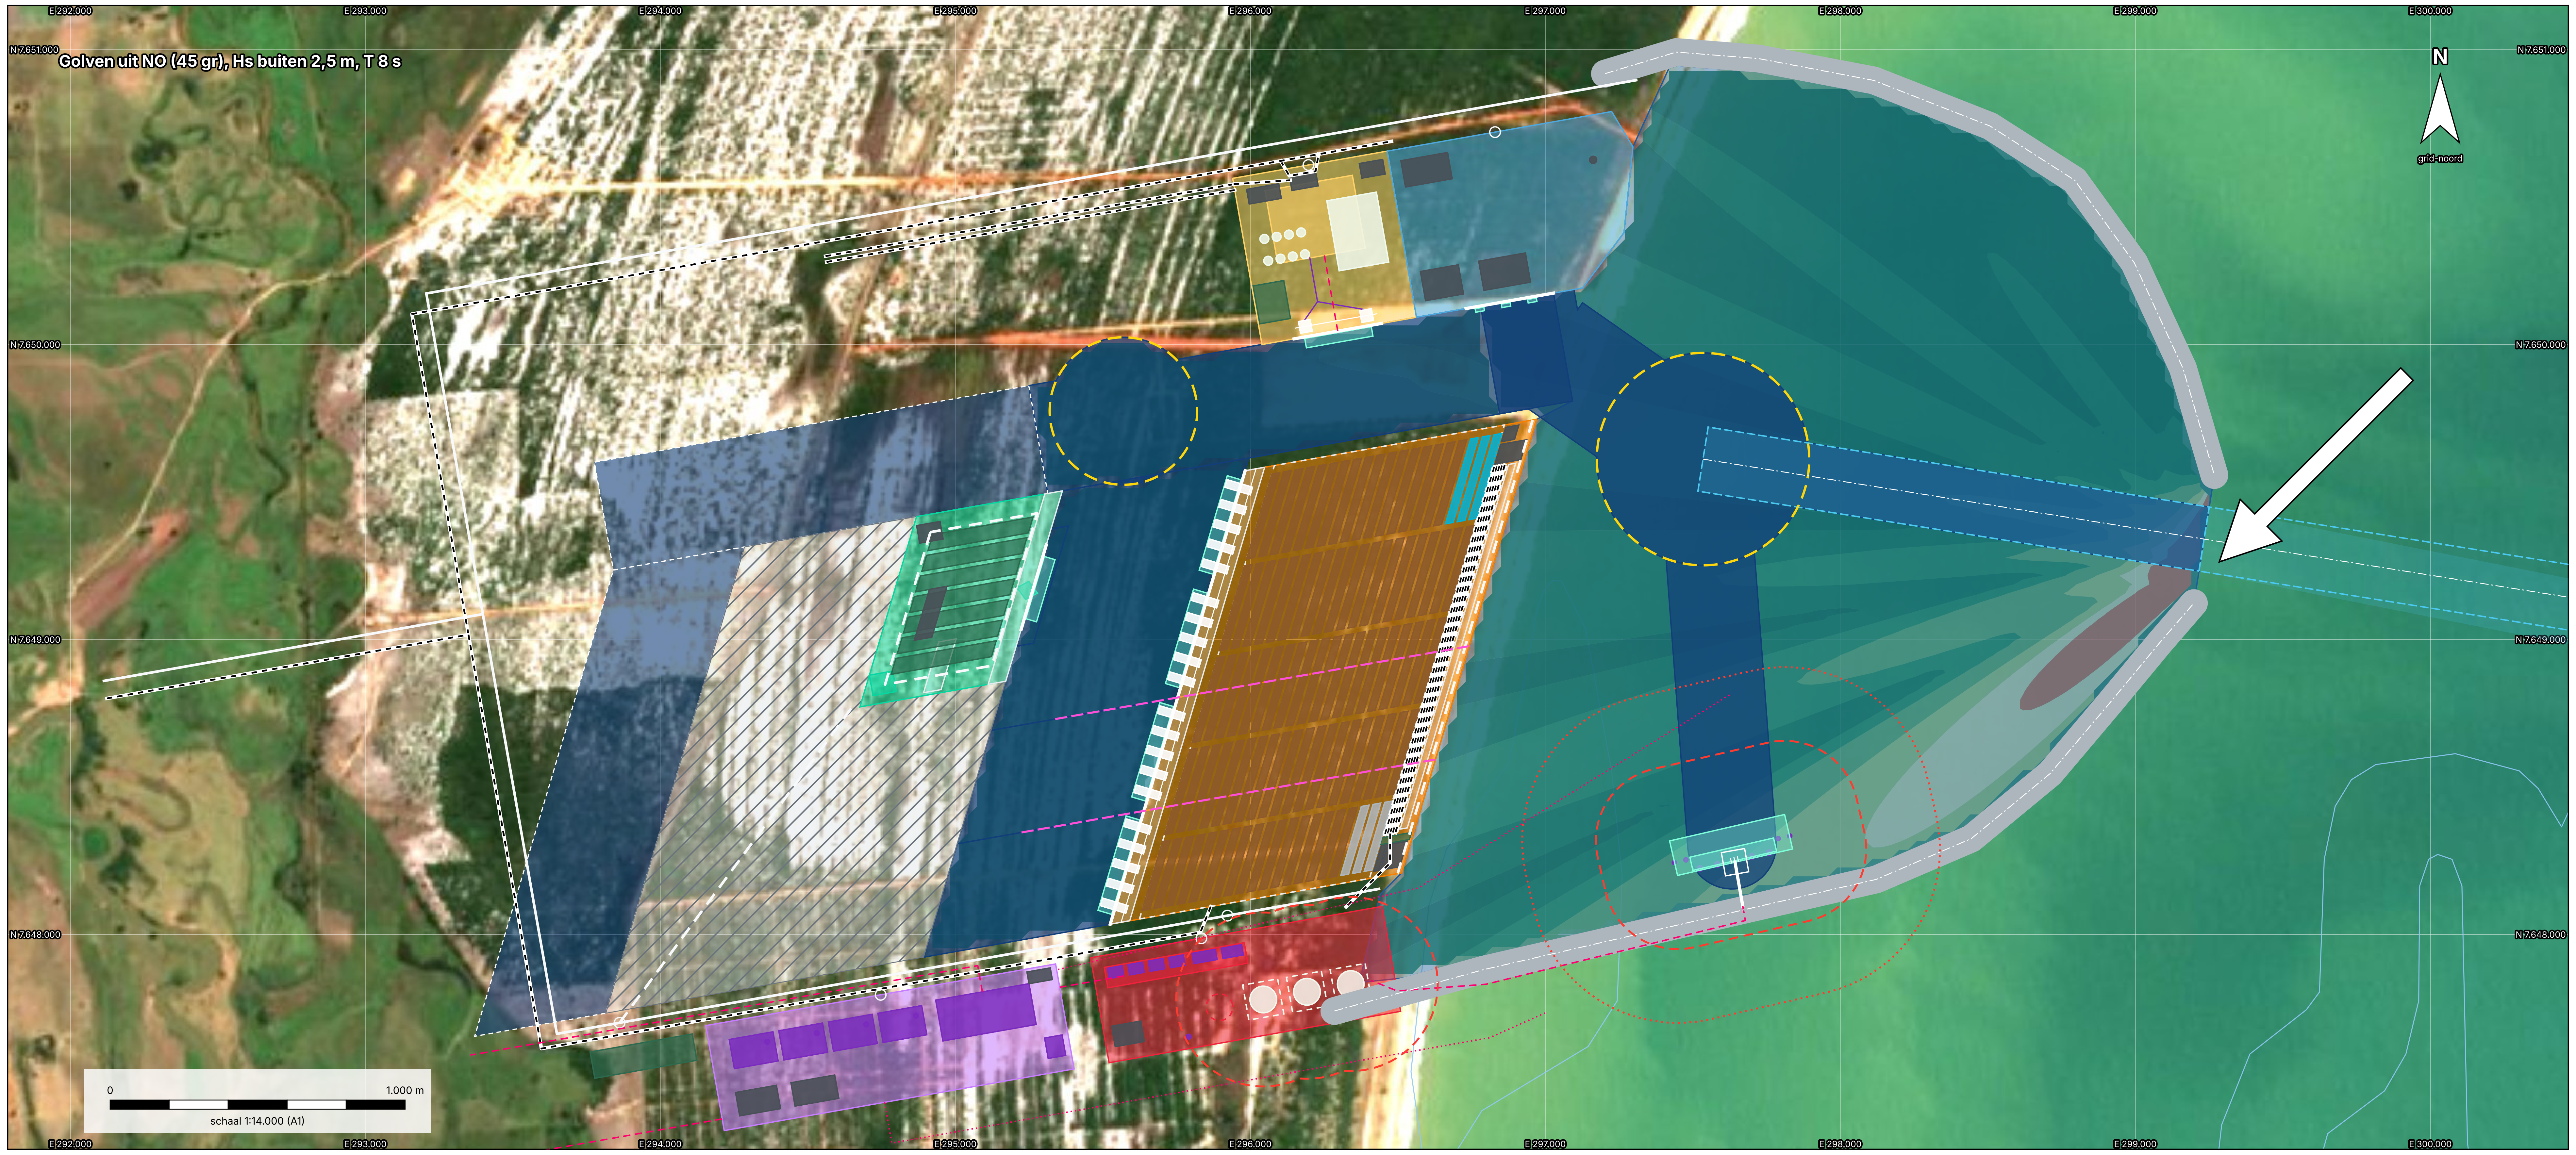
Golven uit NO (45 gr), Hs buiten 2,5 m, T 8 s

Hs aan de ligplaats (m) = Kd x Hs buiten

0,0 0,1 0,3 0,5 1,0 1,5 2,0

Toets per ligplaats (maatgevende richting NO-ZZO)

Ligplaats	Kd max	Hs (m)	grens	toets
Containers C1-C4 (insteek, westzijde)	0,01	0,01	0,5	voldoet
Graan (noordkade hoofdbekken)	0,29	0,73	1,0	voldoet
RoRo (insteek, vinger 7/8)	0,01	0,03	0,3	voldoet
LNG (achter zuidelijke dam)	0,36	0,90	1,0	voldoet
Var.: containerkade oostzijde (voorhav	0,66	1,66	0,5	VOLDOET NIET
Var.: LNG-steiger bij de havenmond (ou	0,43	1,08	1,0	VOLDOET NIET

Methode

Diffractie door opeenvolgende openingen (Huygens-Kirchhoff): havenmond → ingang hoofdbekken → insteek.
Golfrichtingen 45-157,5 gr (NO-ZZO), T 8 s, h 15 m.
Hs buiten 2,5 m = bovenkant bandbreedte Deel 1.
Grenzen (indicatief, PIANC/handboeken): containers 0,5 m, RoRo 0,3 m, graan 1,0 m, LNG 1,0 m.
Niet meegenomen: reflectie, refractie, lange golven; een numeriek golfmodel (bijv. SWAN/Boussinesq) en een schaalmodel volgen in de uitvoeringsfase.

Gevolgen voor het ontwerp

- containers aan de westzijde van vinger 6 (insteek); de oostzijde aan de voorhaven voldoet niet (1,7 m);
- LNG-steiger achter het midden van de zuidelijke dam; de plek bij de havenmond voldoet niet (1,1 m).

Project	Havenontwerp Porto Central, Presidente Kennedy (ES) - Groep 1
Module	Atelier De Haven A | NHL Stenden Civiele Techniek
Bladnaam	**Golftoets ligplaatsen (diffractie)**
Status	**DEFINITIEF ONTWERP (DO)**
Blad / versie	DO-09 | versie 7.0 | 22-10-2026
Schaal	1:14.000 op A1 (841 × 594 mm)
Stelsel	SIRGAS 2000 / UTM zone 24S EPSG:31984 eenheid m
Hoogtedatum	diepten in m t.o.v. MLWS, voorlopig; MLWS-DHN te verifiëren
Kaartbron	Copernicus Sentinel-2 L2A (ESA), 03-07-2026, 10 m
	tegels 24KTB/24KUB, AWS Open Data COG; geraadpleegd 22-10-2026
Kustlijn	waterlijn 03-07-2026 uit NDWI (geen MLWS-lijn)
Bathymetrie	GEBCO 2026 (ca. 450 m) + Copernicus DEM 30 m; MSL→MLWS +0,7 m (aanname)
	geen lodingen: peiling (multibeam) nodig vóór uitvoering

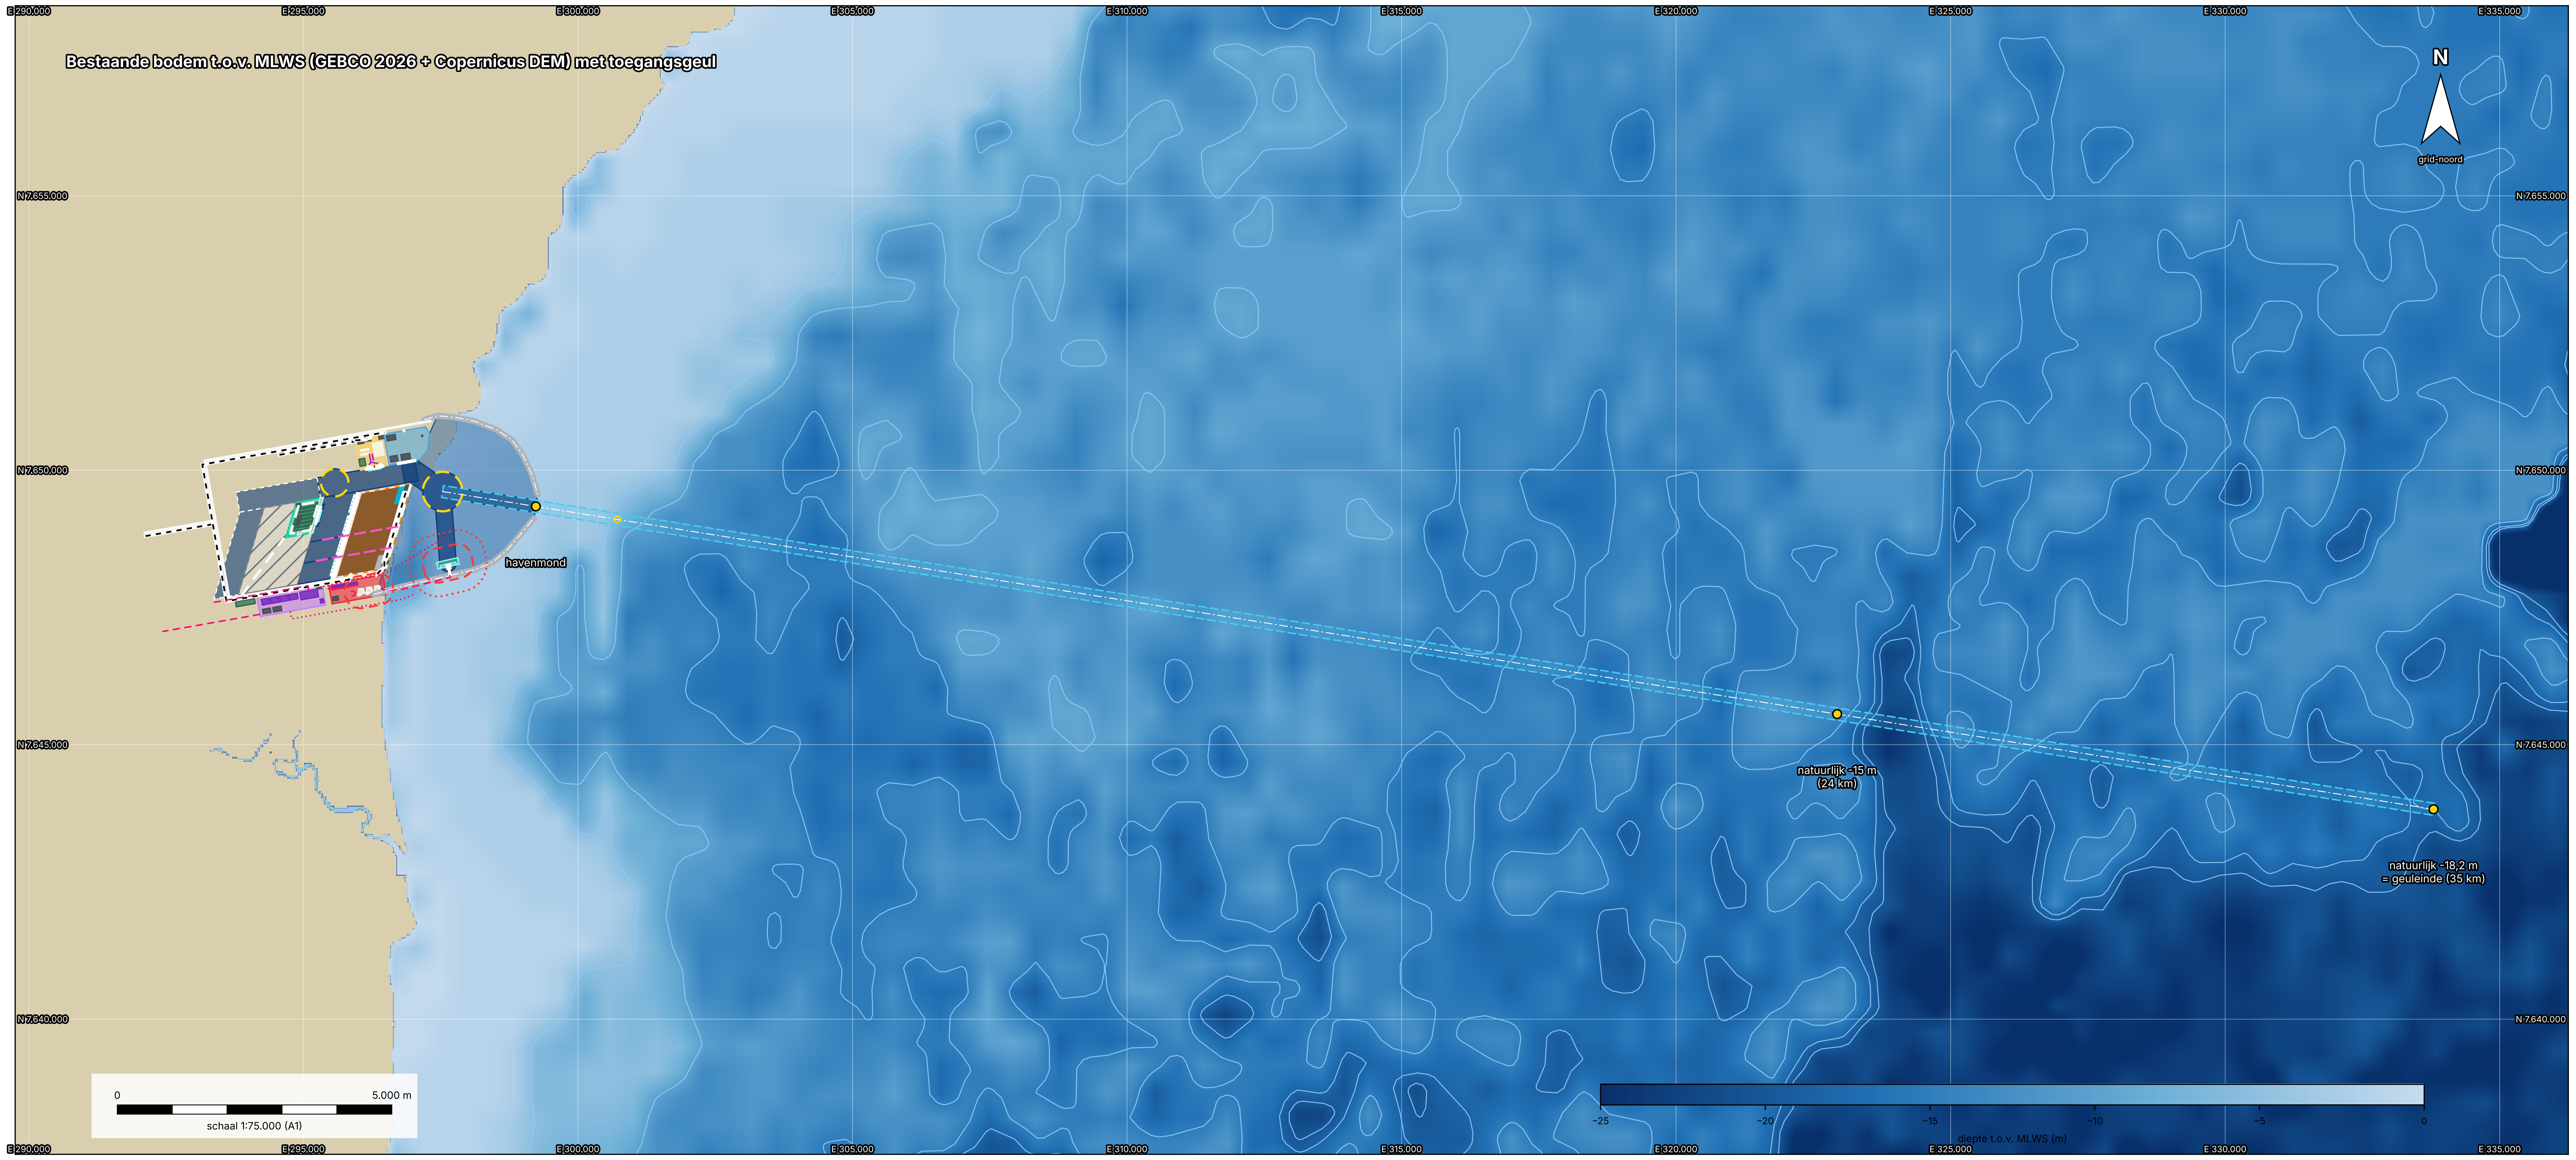

Lengteprofiel toegangsgeul (verticaal sterk overdreven)

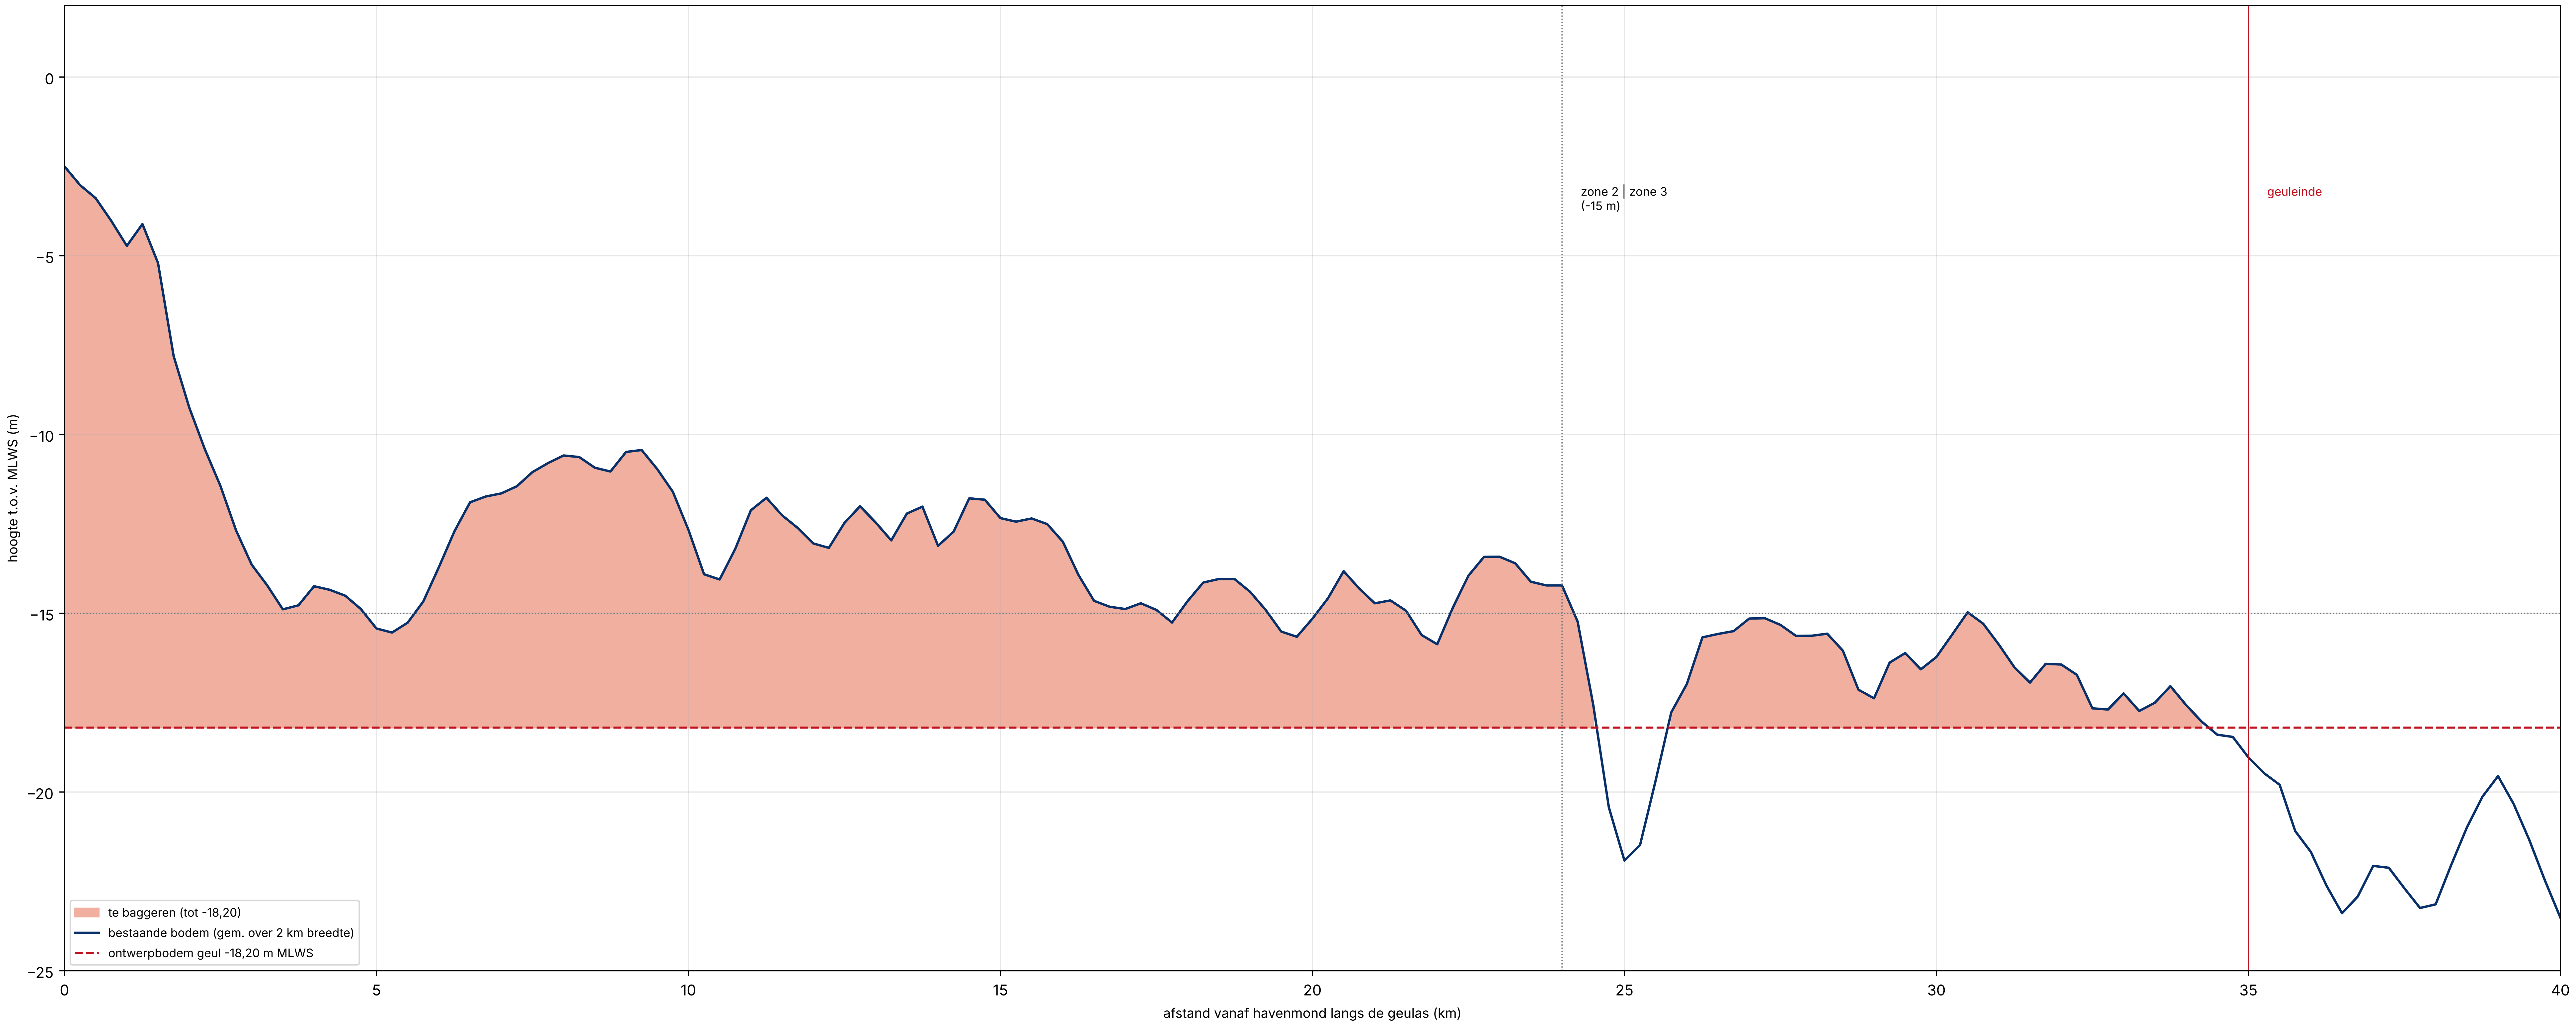

Baggervolumes per vak (celmethode 30 m)

Vak	bodem	ha	nu (gem.)	mln m3
Voorhaven + toegang -18,20	-18,20	90,3	-0,8	15,74
LNG-vaarweg -16,20	-16,20	32,4	-1,7	4,70
Hoofdbekken -18,20	-18,20	60,8	6,9	15,25
Insteekbekken containers -18,2	-18,20	46,3	7,0	11,64
Insteek F2	-18,20	23,1	6,0	5,59
Insteek F3	-18,20	22,9	6,5	5,67
RoRo -13,70	-13,70	2,2	7,2	0,47
Geul tot DHN -15 m	-18,20	528,0	-12,5	29,90
Geul voorbij DHN -15 m	-18,20	241,8	-17,1	3,57
Totaal baggeren		1.048,0		92,5

Besparing door dieptezones t.o.v. overal -18,20: 0,75 mln m3 (LNG-vaarweg -16,20 en RoRo-ligplaats -13,70).
Terrein 327 ha op +5,0 m MLWS: maaiveld nu gem. +7,2 m; afgraving 7,2 mln m3, ophoging 0,15 mln m3 (zetting 0,5 m). Let op: DEM = oppervlak incl. begroeiing, werkelijk maaiveld ligt lager.

Bronnen en aannamen

GEBCO 2026 (15'', ca. 450 m), Source Cooperative;
Copernicus DEM GLO-30 (AWS Open Data);
MLWS = MSL - 0,7 m (aanname, getijslag ca. 1,4 m).
Geuleinde waar de natuurlijke bodem, gemiddeld over 2 km, overal dieper is dan -18,20 m. Bij GEBCO-resolutie +-1 m onzekerheid: lengte kan enkele km verschuiven. Multibeampeiling vóór uitvoering nodig.
Geul kan in fasen: eerst -15,5 m (containerschepen deels beladen, met getij), eindmaat vóór 2045.

Project	Havenontwerp Porto Central, Presidente Kennedy (ES) - Groep 1
Module	Atelier De Haven A | NHL Stenden Civiele Techniek
Bladnaam	**Toegangsgeul, bodemprofiel en grondwerk**
Status	**DEFINITIEF ONTWERP (DO)**
Blad / versie	DO-10 | versie 7.0 | 22-10-2026
Schaal	1:75.000 op A1 (841 × 594 mm)
Stelsel	SIRGAS 2000 / UTM zone 24S EPSG:31984 eenheid m
Hoogtedatum	diepten in m t.o.v. MLWS, voorlopig; MLWS-DHN te verifiëren
Kaartbron	Copernicus Sentinel-2 L2A (ESA), 03-07-2026, 10 m tegels 24KTB/24KUB, AWS Open Data COG; geraadpleegd 22-10-2026
Kustlijn	waterlijn 03-07-2026 uit NDWI (geen MLWS-lijn)
Bathymetrie	GEBCO 2026 (ca. 450 m) + Copernicus DEM 30 m; MSL→MLWS +0,7 m (aanname) geen lodingen: peiling (multibeam) nodig vóór uitvoering