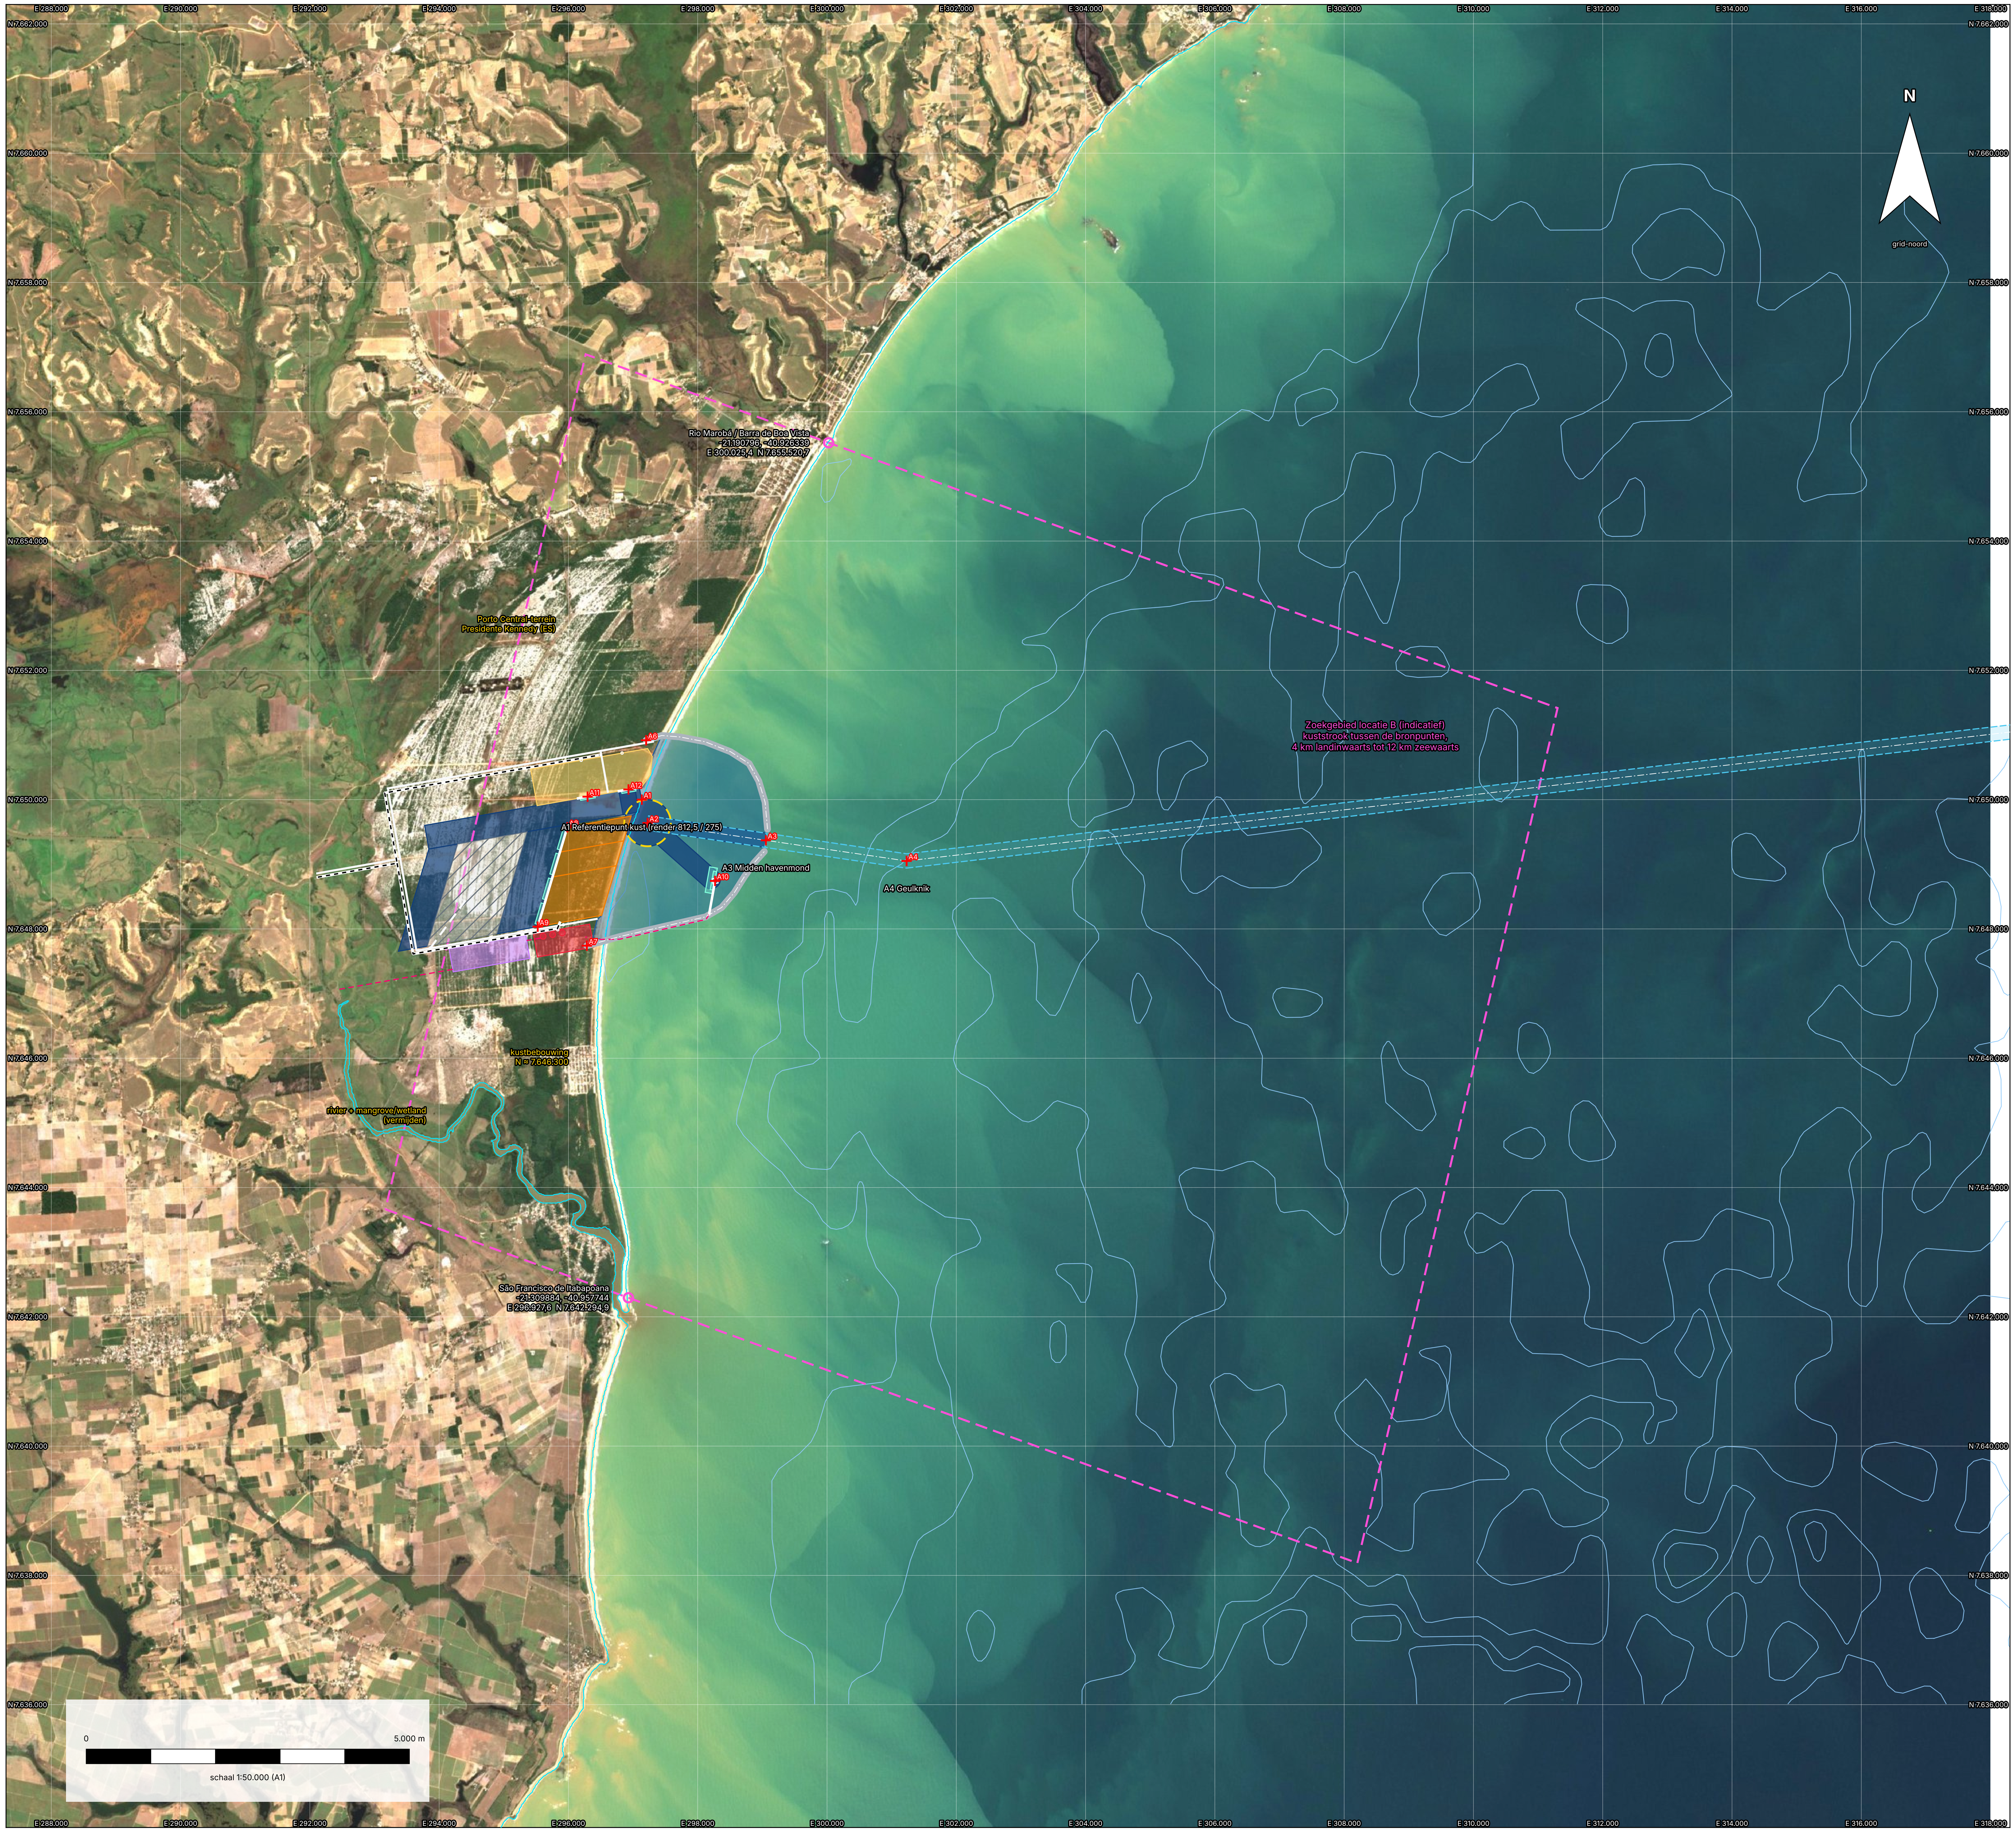
E 288.000
E 290.000
E 292.000
E 294.000
E 296.000
E 298.000
E 300.000
E 302.000
E 304.000
E 306.000
E 308.000
E 310.000
E 312.000
E 314.000
E 316.000
E 318.000
N 7.662.000
N 7.660.000
N 7.658.000
N 7.656.000
N 7.654.000
N 7.652.000
N 7.650.000
N 7.648.000
N 7.646.000
N 7.644.000
N 7.642.000
N 7.640.000
N 7.638.000
N 7.636.000
N
grid-noord
Rio Marobá / Barra de Boa Vista
-21.190796, -40.926339
E 300.025,4 N 7.655.520,7
Porto Central-terrein
Presidente Kennedy (ES)
Zoekgebied locatie B (indicatief)
kuststrook tussen de bronpunten,
4 km landinwaarts tot 12 km zeewaarts
A1
A2
A3
A4
A6
A7
A8
A9
A10
A11
A12
A1 Referentiepunt kust (render 812,5 / 275)
A3 Midden havenmond
A4 Geulknik
kustbebouwing
N ≈ 7.646.300
rivier + mangrove/wetland
(vermijden)
São Francisco de Itabapoana
-21.309884, -40.957744
E 296.927,6 N 7.642.294,9
0
5.000 m
schaal 1:50.000 (A1)

LEGENDA

━	Waterlijn 3-7-2026 (NDWI, geen MLWS-lijn)
- -	Zoekgebied locatie B (indicatief)
■	Voorhaven binnen de dammen (strandwal ontgraven)
■	Gebaggerd tot -18,20 m MLWS (voorlopig)
▨	Geul 220 m bodembreedte
☐	Vrije draaikom D = 720 m
☐	Havenmond vrij 350 m
■	Golfbreker (footprint 90 m, voorlopig)
	Kade / steiger
■	Scheepsenveloppe aan ligplaats
■	Containerterminal
■	Graanterminal
■	LNG-steiger, tanks en hervergassing
■	Centrale + utilities (reservering)
▨	Reserveterrein / latere uitbreiding
━	Hoofdweg + terminalinritten
- - - -	Spoor
— — ·	LNG/gasleiding, koelwater (indicatief)
+	Ontwerpankerpunt (E/N in maatstaat)
━	Dieptelijn t.o.v. MLWS (GEBCO 2026, indicatief)

Havenligging (vastgesteld)
Porto Central, Presidente Kennedy - ES, 29350-000
Havenas haaks op de kust: azimut 110 gr (kust 20.1 gr).
A1 kustpunt: E 297.135,0 N 7.650.000,0
= -21.240329, -40.954826 (WGS84)
Havenas door het bouwterrein fase 1 aan het strand
(lichte rechthoek op de luchtfoto 03-07-2026);
bekkens landinwaarts op het kale Porto Central-terrein.

Georeferentiecontrole
GSHHS-kust vs. S2-waterlijn: gem. 14 m, sd 66 m
(15 profielen, N 7.642-7.656 km)
Bekende afstand bronpunten: 13.582,4 m geodetisch,
13.583,8 m in grid (k = 1.00010)
Noordrichting: convergentie 0.70 gr

Vormreferentie: Porto Central masterplan 2016, p. 9 (ANTT)

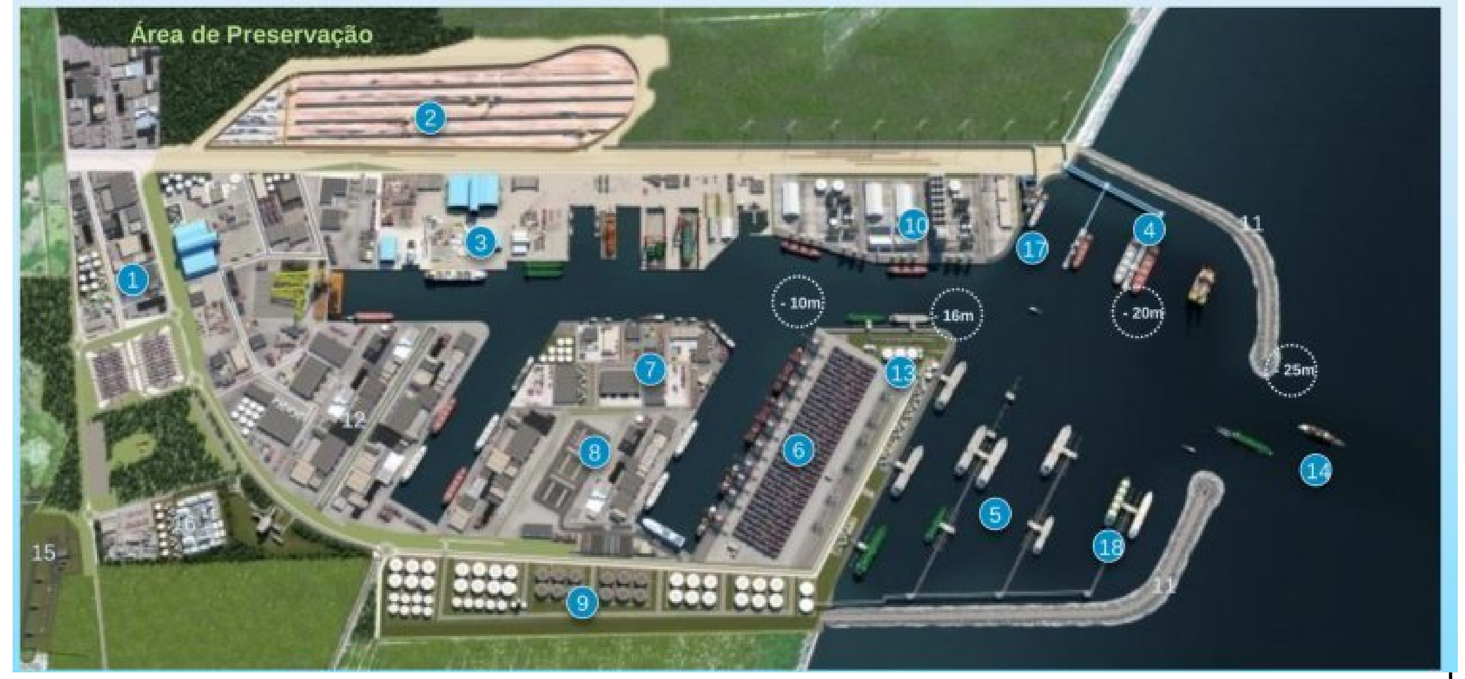
Área de Preservação
1
2
3
4
5
6
7
8
9
10
11
12
13
14
15
16
17
18
- 10m
16m
- 20m
25m

Overgenomen: 11/14 dammen | vingers en insteken | 6 containers | 10 graan | 7/8 RoRo
9 tankpark (LNG + centrale) | 18 LNG-steiger. Weggelaten (niet in opdracht): 2, 3, 5, 12, 1

Project	Havenontwerp Porto Central, Presidente Kennedy (ES) - Groep 1
Module	Atelier De Haven A | NHL Stenden Civiele Techniek
Bladnaam	**Overzicht zoekgebied en havenligging**
Status	**SCHETSONTWERP (SO)**
Blad / versie	SO-01 | versie 4.0 | 22-10-2026
Schaal	1:50.000 op A1 (841 × 594 mm)
Stelsel	SIRGAS 2000 / UTM zone 24S EPSG:31984 eenheid m
Hoogtedatum	diepten in m t.o.v. MLWS, voorlopig; MLWS-DHN te verifiëren
Kaartbron	Copernicus Sentinel-2 L2A (ESA), 03-07-2026, 10 m tegels 24KTB/24KUB, AWS Open Data COG; geraadpleegd 22-10-2026
Kustlijn	waterlijn 03-07-2026 uit NDWI (geen MLWS-lijn)
Bathymetrie	GEBCO 2026 (ca. 450 m) + Copernicus DEM 30 m; MSL→MLWS +0,7 m (aanname) geen lodingen: peiling (multibeam) nodig vóór uitvoering

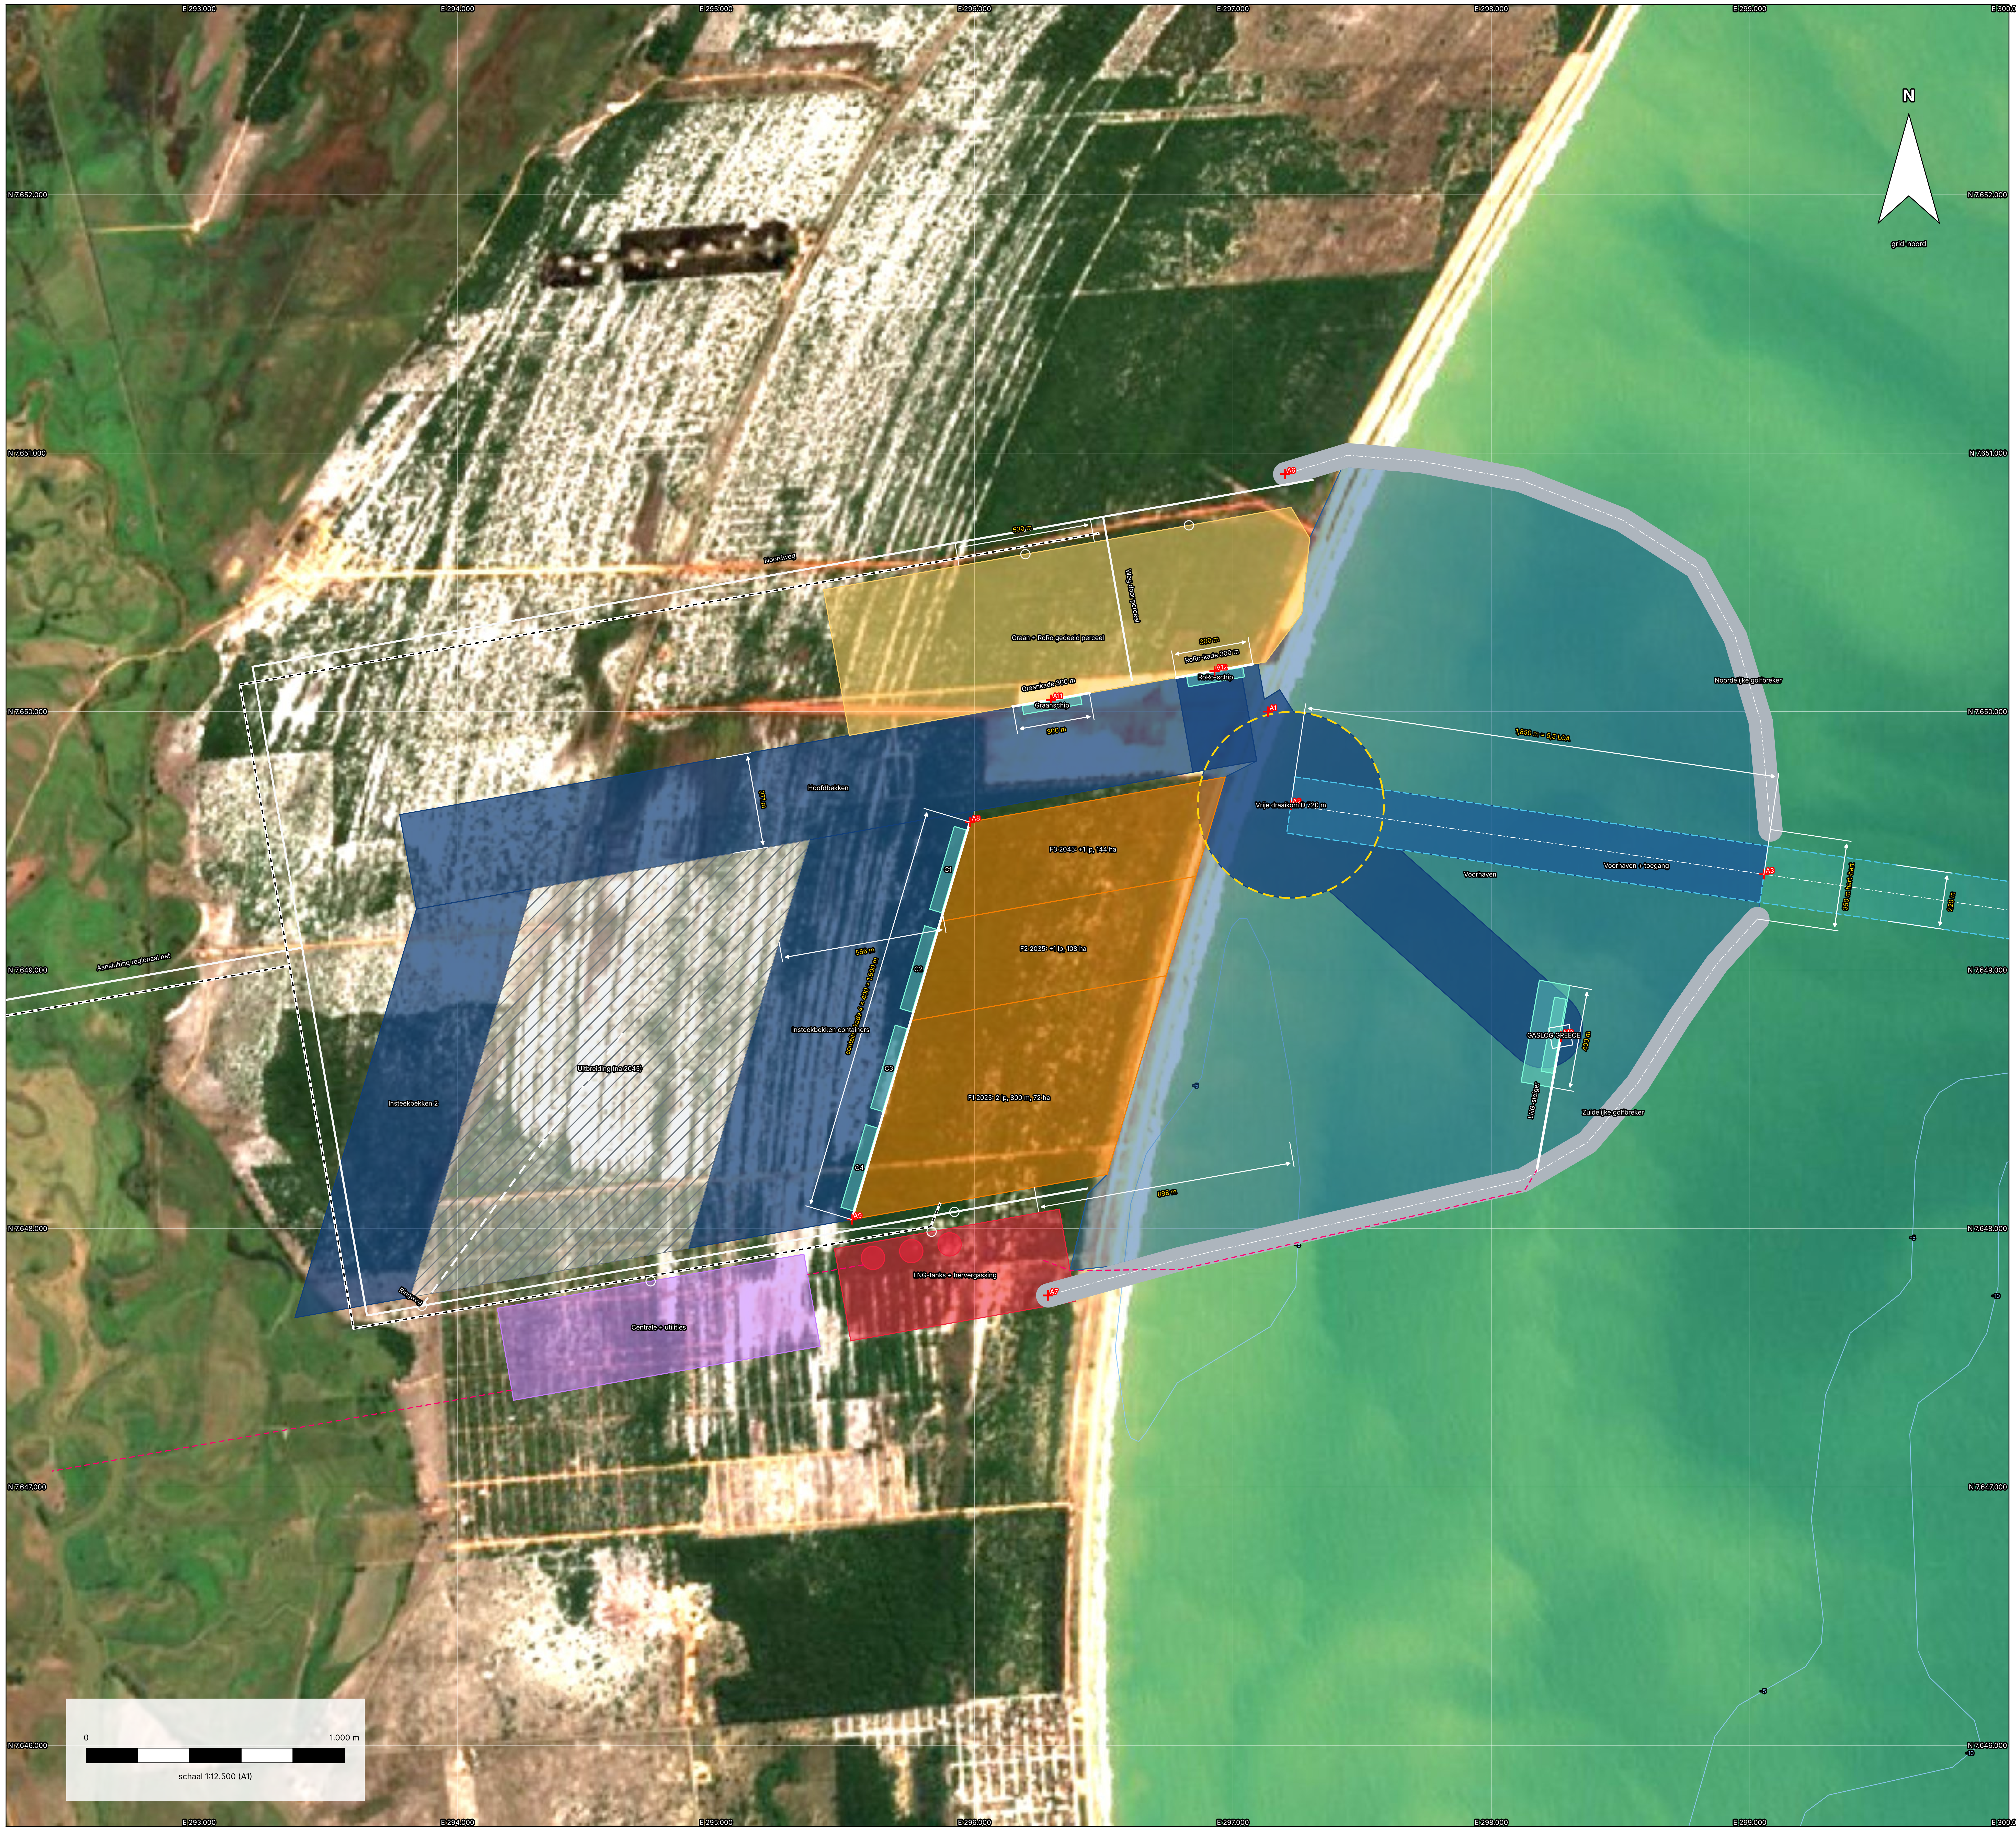
E 293.000
E 294.000
E 295.000
E 296.000
E 297.000
E 298.000
E 299.000
E 300.000
N 7.652.000
N 7.651.000
N 7.650.000
N 7.649.000
N 7.648.000
N 7.647.000
N 7.646.000
N
grid-noord
Noordweg
530 m
Weg door perceel
Graan + RoRo gedeeld perceel
A6
300 m
RoRo-kade 300 m
A12
RoRo-schip
Graankade 300 m
A11
Graanschip
300 m
A1
Hoofdbekken
371 m
A8
F3 2045: +1 lp, 144 ha
Vrije draaikom D 720 m
A2
1.850 m = 5,5 LOA
Noordelijke golfbreker
Voorhaven + toegang
Voorhaven
A3
350 m hart-hart
220 m
C1
C2
C3
C4
556 m
containerkade 4 × 400 = 1.600 m
F2 2035: +1 lp, 108 ha
Insteekbekken containers
F1 2025: 2 lp, 800 m, 72 ha
Uitbreiding (na 2045)
Insteekbekken 2
Aansluiting regionaal net
GASLOG GREECE
400 m
LNG-steiger
Zuidelijke golfbreker
-5
898 m
A9
A7
LNG-tanks + hervergassing
Centrale + utilities
Ringweg
-10
0
1.000 m
schaal 1:12.500 (A1)

LEGENDA

- ▬ Waterlijn 3-7-2026 (NDWI, geen MLWS-lijn)
- ╍ Zoekgebied locatie B (indicatief)
- ■ Voorhaven binnen de dammen (strandwal ontgraven)
- ■ Gebaggerd tot -18,20 m MLWS (voorlopig)
- ▭ Geul 220 m bodembreedte
- ▭ Vrije draaikom D = 720 m
- ▭ Havenmond vrij 350 m
- ■ Golfbreker (footprint 90 m, voorlopig)
- Kade / steiger
- ■ Scheepsenveloppe aan ligplaats
- ■ Containerterminal
- ■ Graanterminal
- ■ LNG-steiger, tanks en hervergassing
- ■ Centrale + utilities (reservering)
- ▨ Reserveterrein / latere uitbreiding
- ▬ Hoofdweg + terminalinritten
- ╍ Spoor
- ╍ LNG/gasleiding, koelwater (indicatief)
- + Ontwerpankerpunt (E/N in maatstaat)
- ▬ Dieptelijn t.o.v. MLWS (GEBCO 2026, indicatief)

Hoofdmaten (gemeten in tekening)

Geul bodembreedte 220 m, bodem -18,20 m MLWS (voorlopig)
Geul buiten de mond: 35.500 m (voorlopig)
Havenmond vrij tussen dammen: 260 m
Draaikom D 720 m; vrij van schepen 167 m
Stopweg mond-draaikom 1.850 m = 5,5 LOA
Containerkade 802 / 1.203 / 1.604 m
Containerterrein 72,0 / 108,0 / 144,0 ha
Graan 103,8 ha, RoRo 103,8 ha, kades 300 m
LNG-zone 31,9 ha; centrale (reservering) 43,5 ha
Vrije breedte binnenbekken 334 m

Fasen (globaal)

F1 = zuideinde containervinger, F2/F3 richting hoofdbekken (zie DO)

Vormreferentie: Porto Central masterplan 2016, p. 9 (ANTT)

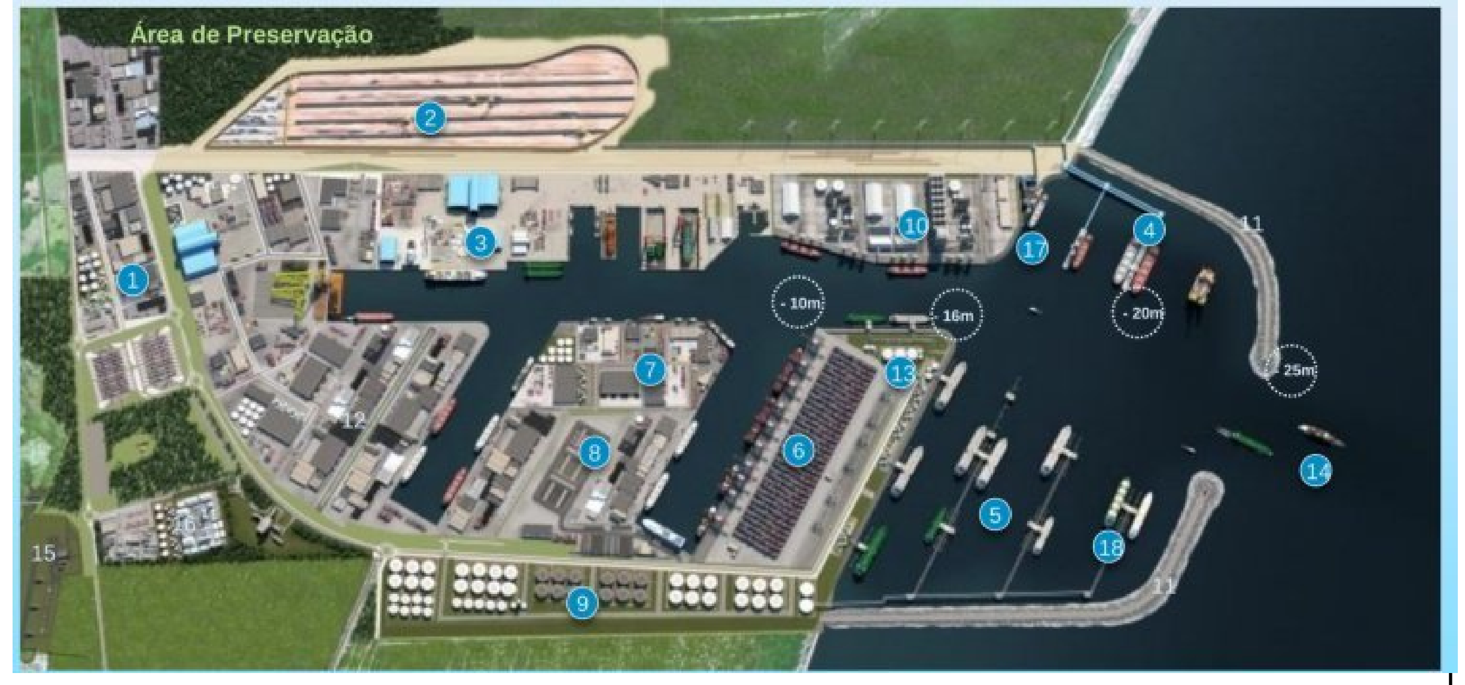
Área de Preservação
1
2
3
4
5
6
7
8
9
10
11
12
13
14
15
16
17
18
- 10m
16m
- 20m
25m

Overgenomen: 11/14 dammen | vingers en insteken | 6 containers | 10 graan | 7/8 RoRo
9 tankpark (LNG + centrale) | 18 LNG-steiger. Weggelaten (niet in opdracht): 2, 3, 5, 12, 1

Project	Havenontwerp Porto Central, Presidente Kennedy (ES) - Groep 1
Module	Atelier De Haven A | NHL Stenden Civiele Techniek
Bladnaam	**Havenindeling**
Status	**SCHETSONTWERP (SO)**
Blad / versie	SO-02 | versie 4.0 | 22-10-2026
Schaal	1:12.500 op A1 (841 × 594 mm)
Stelsel	SIRGAS 2000 / UTM zone 24S EPSG:31984 eenheid m
Hoogtedatum	diepten in m t.o.v. MLWS, voorlopig; MLWS-DHN te verifiëren
Kaartbron	Copernicus Sentinel-2 L2A (ESA), 03-07-2026, 10 m tegels 24KTB/24KUB, AWS Open Data COG; geraadpleegd 22-10-2026
Kustlijn	waterlijn 03-07-2026 uit NDWI (geen MLWS-lijn)
Bathymetrie	GEBCO 2026 (ca. 450 m) + Copernicus DEM 30 m; MSL→MLWS +0,7 m (aanname) geen lodingen: peiling (multibeam) nodig vóór uitvoering

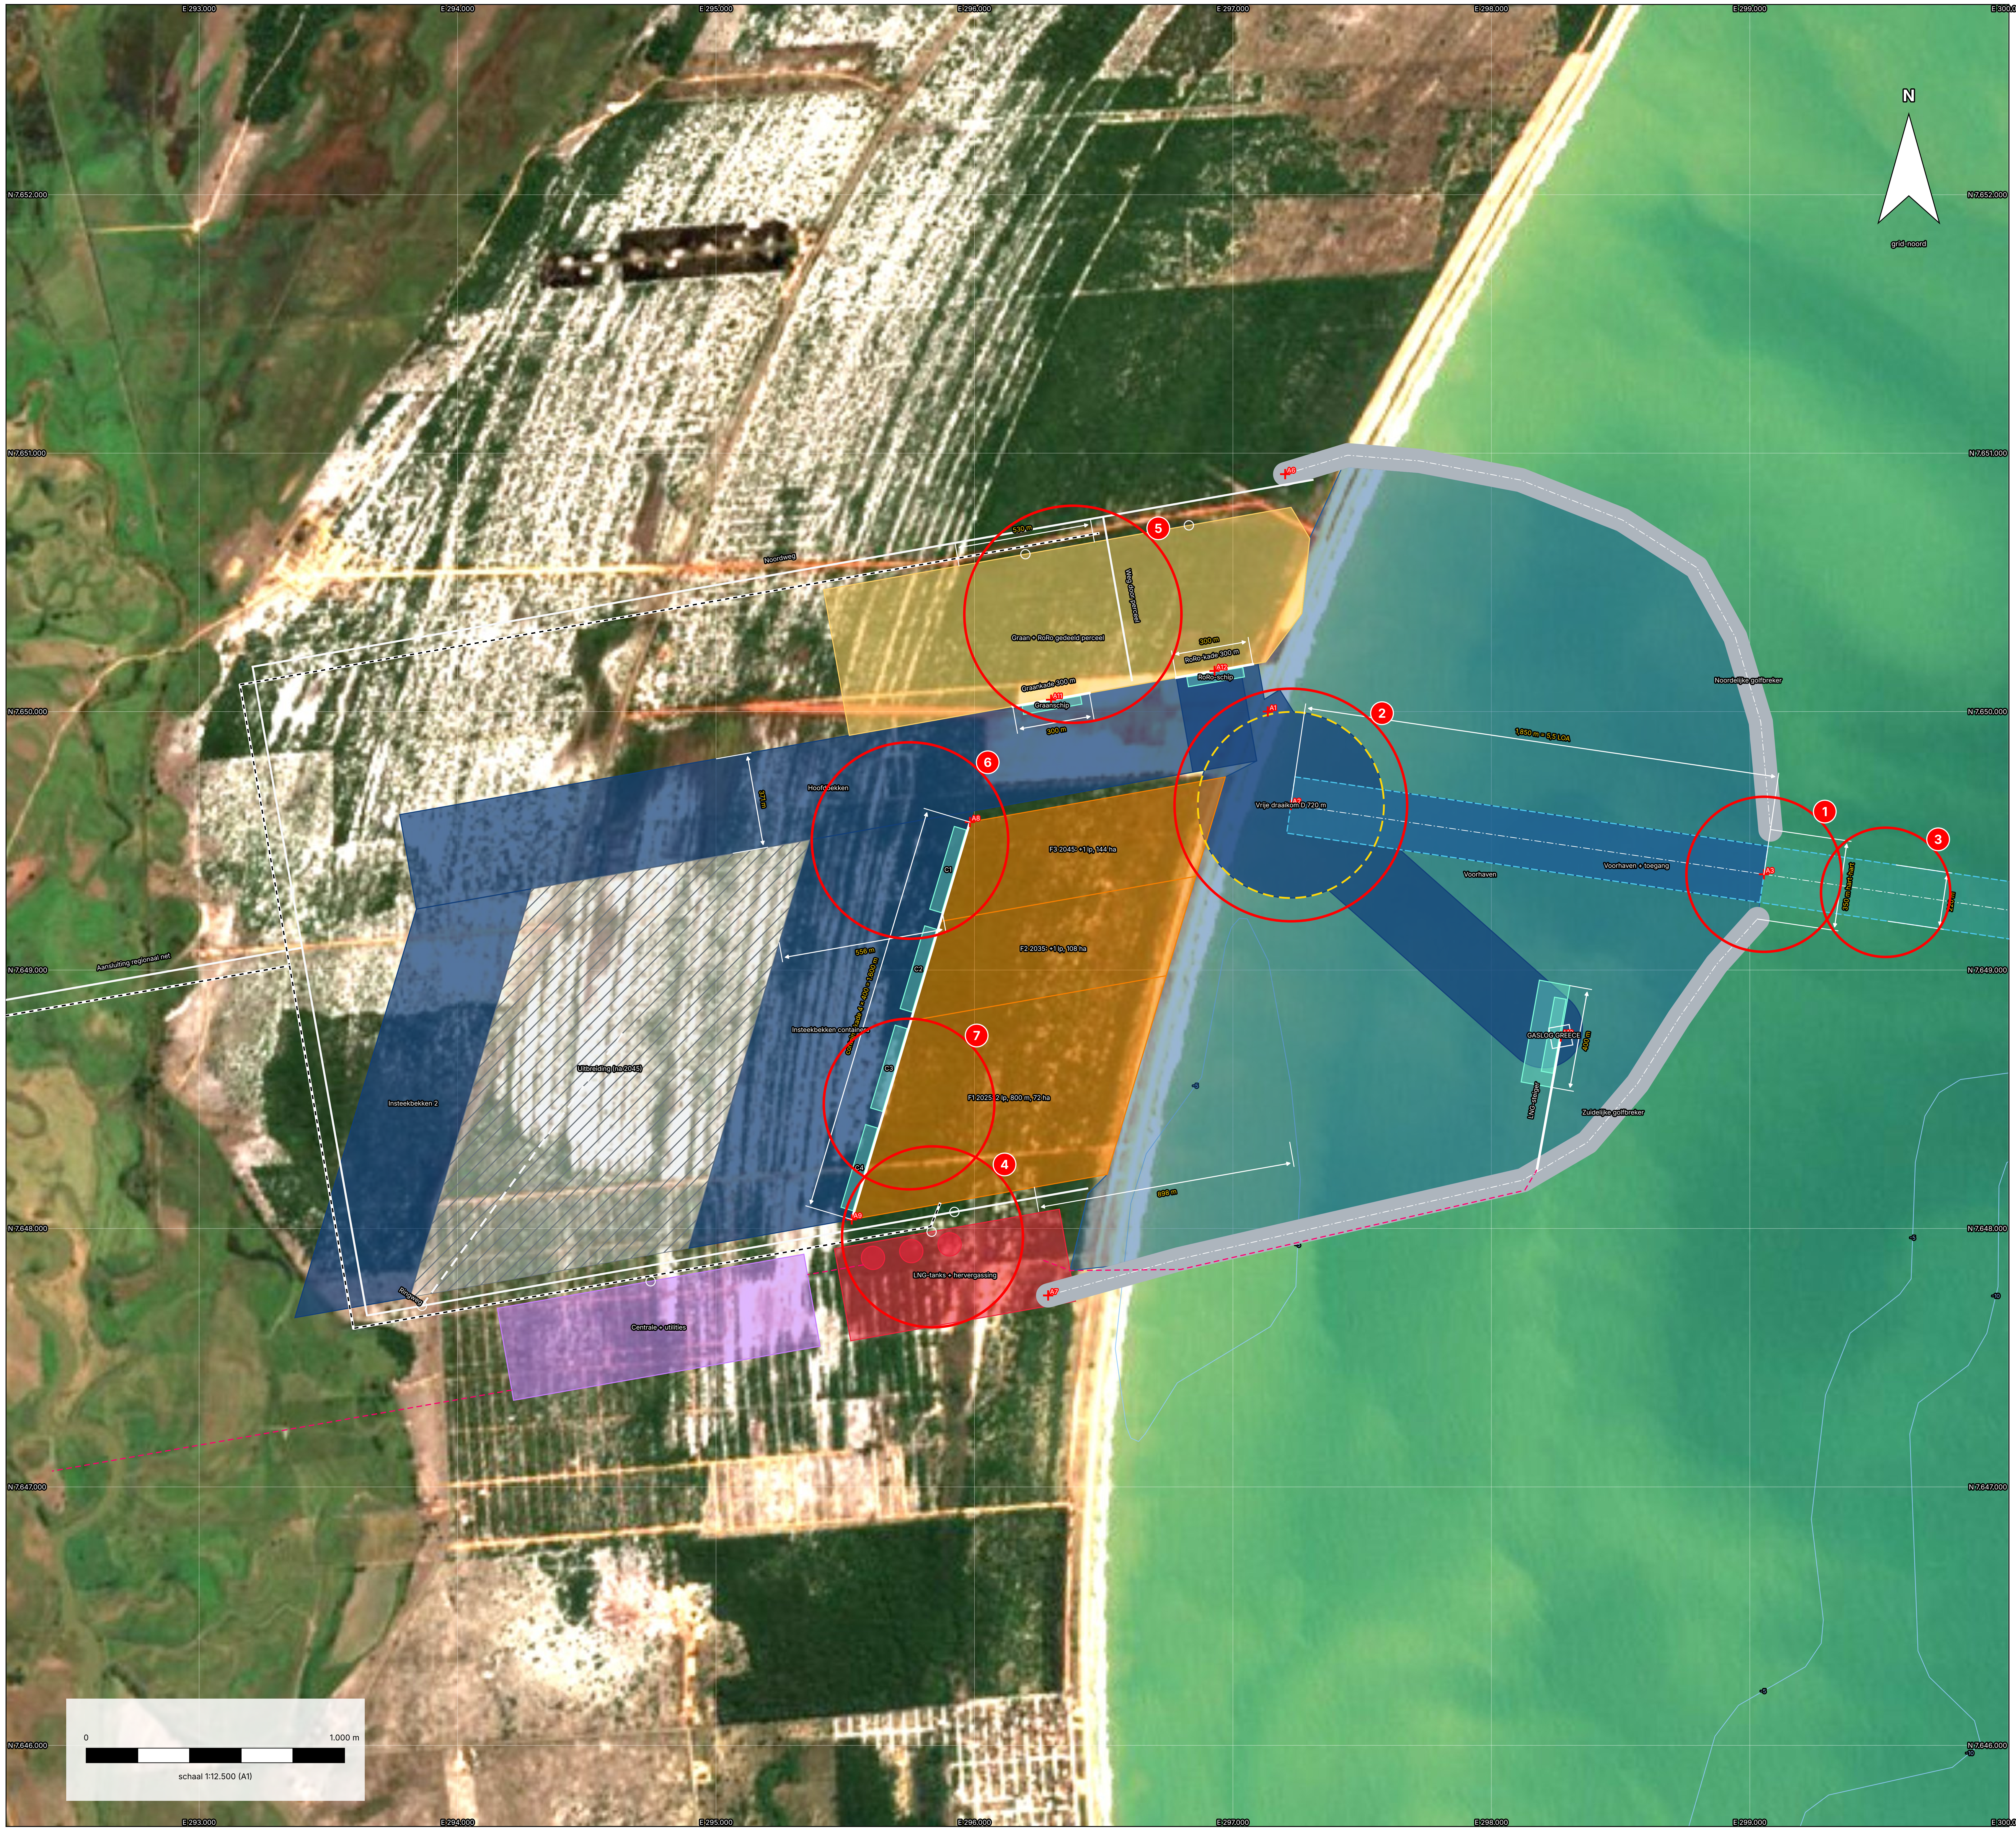
E 293.000
E 294.000
E 295.000
E 296.000
E 297.000
E 298.000
E 299.000
E 300.000
N 7.652.000
N 7.651.000
N 7.650.000
N 7.649.000
N 7.648.000
N 7.647.000
N 7.646.000
N
grid-noord
Noordweg
530 m
Weg door perceel
Graan + RoRo gedeeld perceel
Graankade 300 m
A11
Graanschip
300 m
RoRo-kade 300 m
300 m
A12
RoRo-schip
A6
A1
A2
Vrije draaikom D 720 m
1,850 m = 5,5 LOA
Noordelijke golfbreker
Voorhaven + toegang
Voorhaven
A3
350 m hart-hart
220 m
GASLOG GREECE
400 m
LNG-steiger
Zuidelijke golfbreker
Hoofdbekken
371 m
A8
C1
C2
C3
C4
F3 2045: +1 lp, 144 ha
F2 2035: +1 lp, 108 ha
F1 2025: 2 lp, 800 m, 72 ha
556 m
containerkade 4 × 400 = 1600 m
Insteekbekken containers
Insteekbekken 2
Uitbreiding (na 2045)
Aansluiting regionaal net
Ringweg
A9
898 m
LNG-tanks + hervergassing
A7
Centrale + utilities
-5
-10
1
2
3
4
5
6
7
0
1.000 m
schaal 1:12.500 (A1)

LEGENDA

— Waterlijn 3-7-2026 (NDWI, geen MLWS-lijn)
– – Zoekgebied locatie B (indicatief)
■ Voorhaven binnen de dammen (strandwal ontgraven)
■ Gebaggerd tot -18,20 m MLWS (voorlopig)
▭ Geul 220 m bodembreedte
▭ Vrije draaikom D = 720 m
▭ Havenmond vrij 350 m
■ Golfbreker (footprint 90 m, voorlopig)
Kade / steiger
■ Scheepsenveloppe aan ligplaats
■ Containerterminal
■ Graanterminal
■ LNG-steiger, tanks en hervergassing
■ Centrale + utilities (reservering)
▨ Reserveterrein / latere uitbreiding
— Hoofdweg + terminalinritten
- - - Spoor
– – · LNG/gasleiding, koelwater (indicatief)
+ Ontwerpankerpunt (E/N in maatstaat)
— Dieptelijn t.o.v. MLWS (GEBCO 2026, indicatief)

Bespreekpunten SO (zie rode markering)

1. Havenmond 260 m vrij tussen dammen (350 m hart-hart gemeten)
2. Draaikom overlapt de containervinger (1,5 ha)
3. Geen sleepbootkoppelpunt; geul knikt 15 gr op 2,2 km buiten de mond
4. LNG-tanks op 116 m van het containerterrein
5. Graan + RoRo op één perceel aan de noordkade; weg kruist het terrein
6. Containerschip 334 m moet 63 gr draaien van hoofdbekken (370 m) naar insteek: niet haalbaar
7. Containers F1 aan het zuideinde; geen draaikom binnen voor graan/RoRo; alles in F1 baggeren

Vormreferentie: Porto Central masterplan 2016, p. 9 (ANTT)

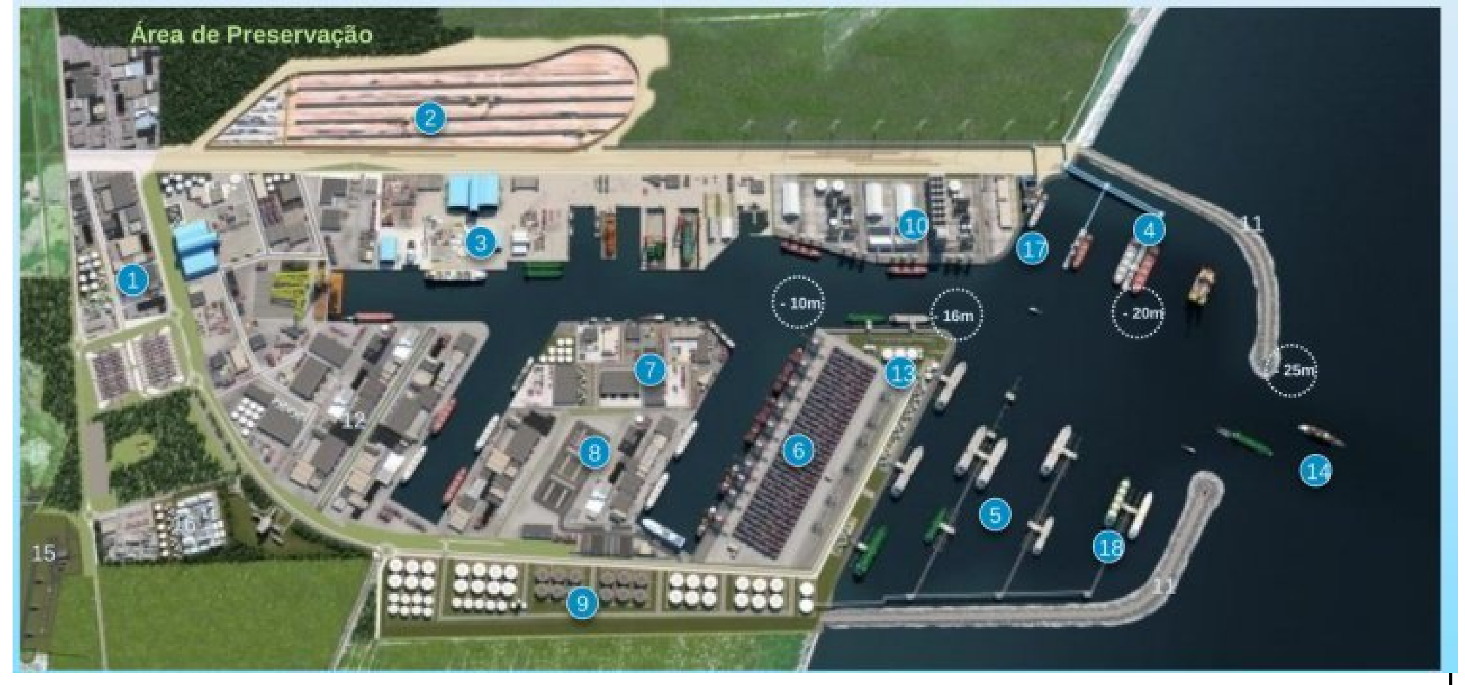
Área de Preservação
1
2
3
4
5
6
7
8
9
10
11
12
13
14
15
16
17
18
- 10m
16m
- 20m
25m

Overgenomen: 11/14 dammen | vingers en insteken | 6 containers | 10 graan | 7/8 RoRo
9 tankpark (LNG + centrale) | 18 LNG-steiger. Weggelaten (niet in opdracht): 2, 3, 5, 12, 1

Project	Havenontwerp Porto Central, Presidente Kennedy (ES) - Groep 1
Module	Atelier De Haven A | NHL Stenden Civiele Techniek
Bladnaam	**Bespreking SO - bespreekpunten**
Status	**SCHETSONTWERP (SO)**
Blad / versie	SO-03 | versie 4.0 | 22-10-2026
Schaal	1:12.500 op A1 (841 × 594 mm)
Stelsel	SIRGAS 2000 / UTM zone 24S EPSG:31984 eenheid m
Hoogtedatum	diepten in m t.o.v. MLWS, voorlopig; MLWS-DHN te verifiëren
Kaartbron	Copernicus Sentinel-2 L2A (ESA), 03-07-2026, 10 m tegels 24KTB/24KUB, AWS Open Data COG; geraadpleegd 22-10-2026
Kustlijn	waterlijn 03-07-2026 uit NDWI (geen MLWS-lijn)
Bathymetrie	GEBCO 2026 (ca. 450 m) + Copernicus DEM 30 m; MSL→MLWS +0,7 m (aanname) geen lodingen: peiling (multibeam) nodig vóór uitvoering