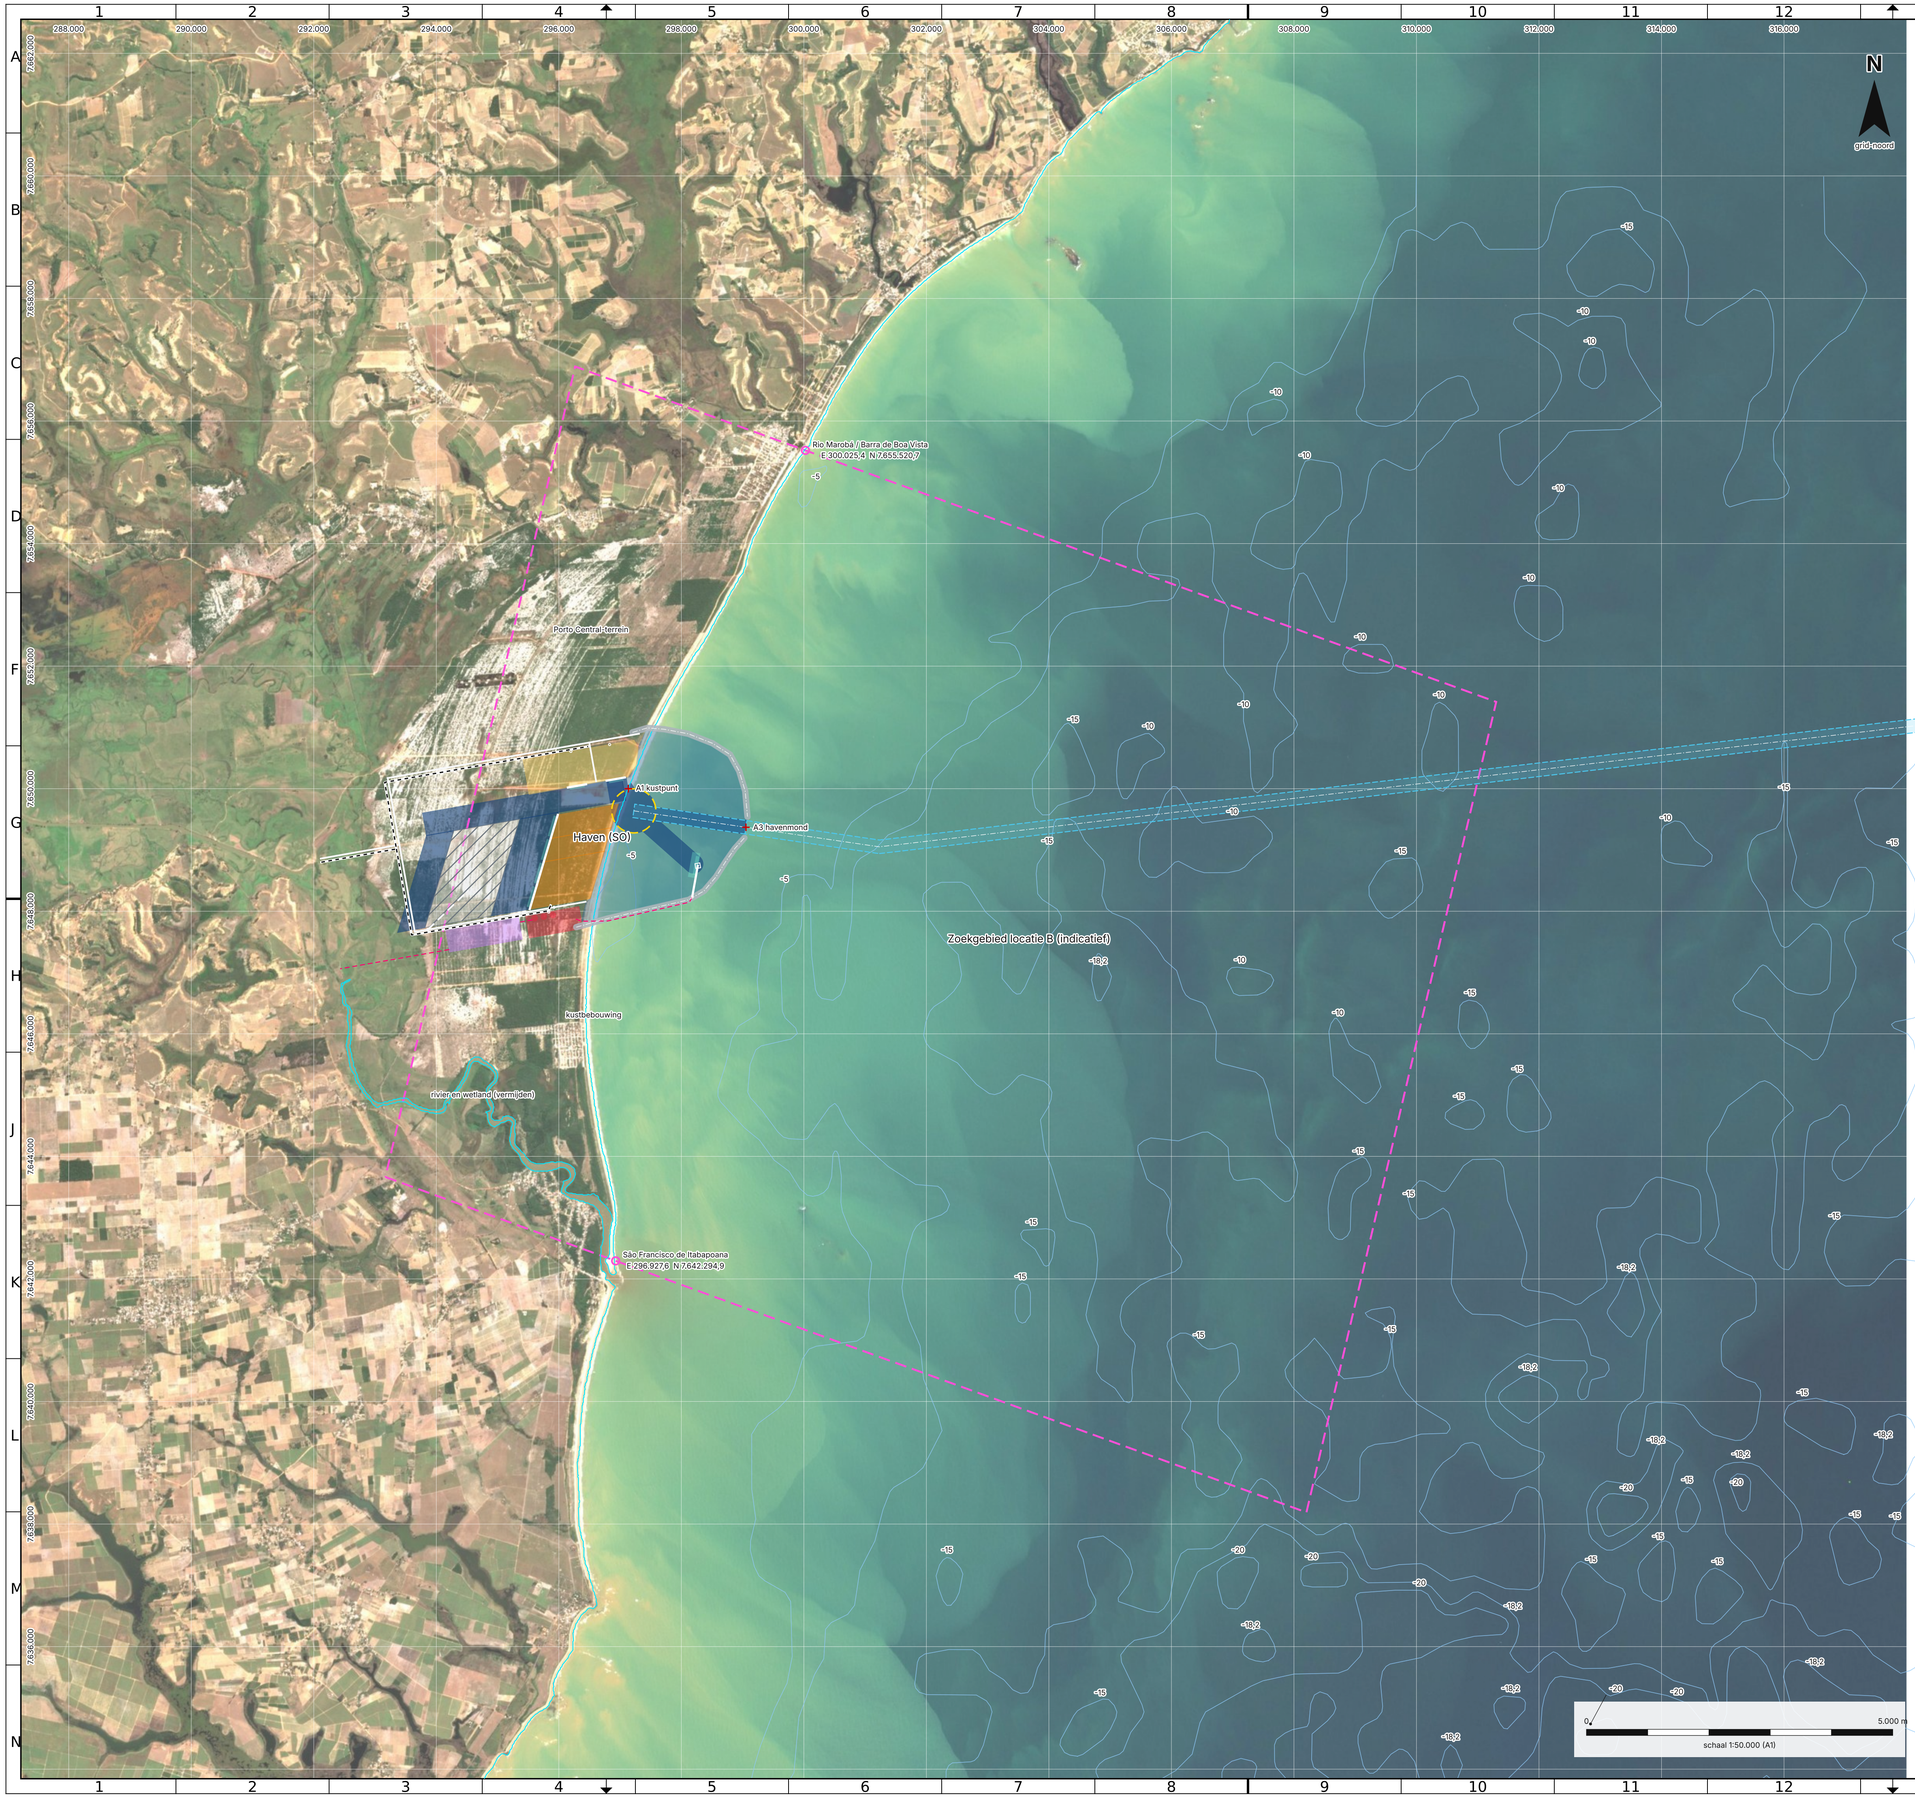


LEGENDA

- Waterlijn 3-7-2026 (NDWI, geen MLWS-lijn)
- Zoekgebied locatie B (indicatief)
- Voorhaven binnen de dammen (strandwal ontgraven)
- Gebaggerd tot -18,20 m MLWS (voorlopig)
- Geul 220 m bodembreedte
- Vrije draaikom D = 720 m
- Havenmond vrij 350 m
- Golfbreker (footprint 90 m, voorlopig)
- Kade / steiger
- Scheepsenveloppe aan ligplaats
- Containerterminal
- Graanterminal
- LNG-steiger, tanks en hervergassing
- Centrale + utilities (reservering)
- Reserveterrein / latere uitbreiding
- Hoofdweg + terminalinritten
- Spoor
- LNG/gasleiding, koelwater (indicatief)
- Ontwerpankerpunt (E/N in maatstaat)
- Dieptelijn t.o.v. MLWS (GEBCO 2026, indicatief)

Havenligging (vastgesteld)
Porto Central, Presidente Kennedy - ES, 29350-000
Havenas haaks op de kust: azimut 110 gr (kust 20.1 gr).
A1 kustpunt: E 297.135,0 N 7.650.000,0
= -21.240329, -40.954826 (WGS84)
Havenas door het bouwterrein fase 1 aan het strand
(lichte rechthoek op de luchtfoto 03-07-2026);
bekkens landinwaarts op het kale Porto Central-terrein.

Georeferentiecontrole
GSHHS-kust vs. S2-waterlijn: gem. 14 m, sd 66 m
(15 profielen, N 7.642–7.656 km)
Bekende afstand bronpunten: 13.582,4 m geodetisch,
13.583,8 m in grid (k = 1.00010)
Noordrichting: convergentie 0.70 gr

Algemene gegevens
Stelsel: SIRGAS 2000 / UTM zone 24S (EPSG:31984), eenheid m
Hoogte: m t.o.v. MLWS (voorlopig; MLWS = MSL − 0,7 m)
Luchtfoto: Copernicus Sentinel-2 L2A, 03-07-2026, 10 m
Bathymetrie: GEBCO 2026 + Copernicus DEM; geen peiling
Atelier De Haven A, NHL Stenden | 22-10-2026 | schaal 1:50.000

	07	
	06	
	05	
	04	
	03	
v4.1: NHL-template, teksten zonder overlap, rustiger tekenbeeld	02	22-10-2026
v4.0: schetsontwerp op de Porto Central-render met bespreekpunten	01	22-10-2026
Opmerkingen:	Versie:	Datum:


Opdrachtgever:
NHL Stenden

Get: Groep 1	Formaat: A1	Projectnummer: Groep 1	
Gec: -	Schaal: 1:50.000	Tekeningnummer: HAVEN-SO-01	
Vrijg: -	Bladnummer: 1 van 3	Status: SO	Versie: 4.1

Projectnaam:
Havenontwerp Porto Central
Presidente Kennedy (ES), Brazilië

Omschrijving:
SO-01 Overzicht zoekgebied en havenligging

Bureau Schmidt
ingenieurs en adviseurs

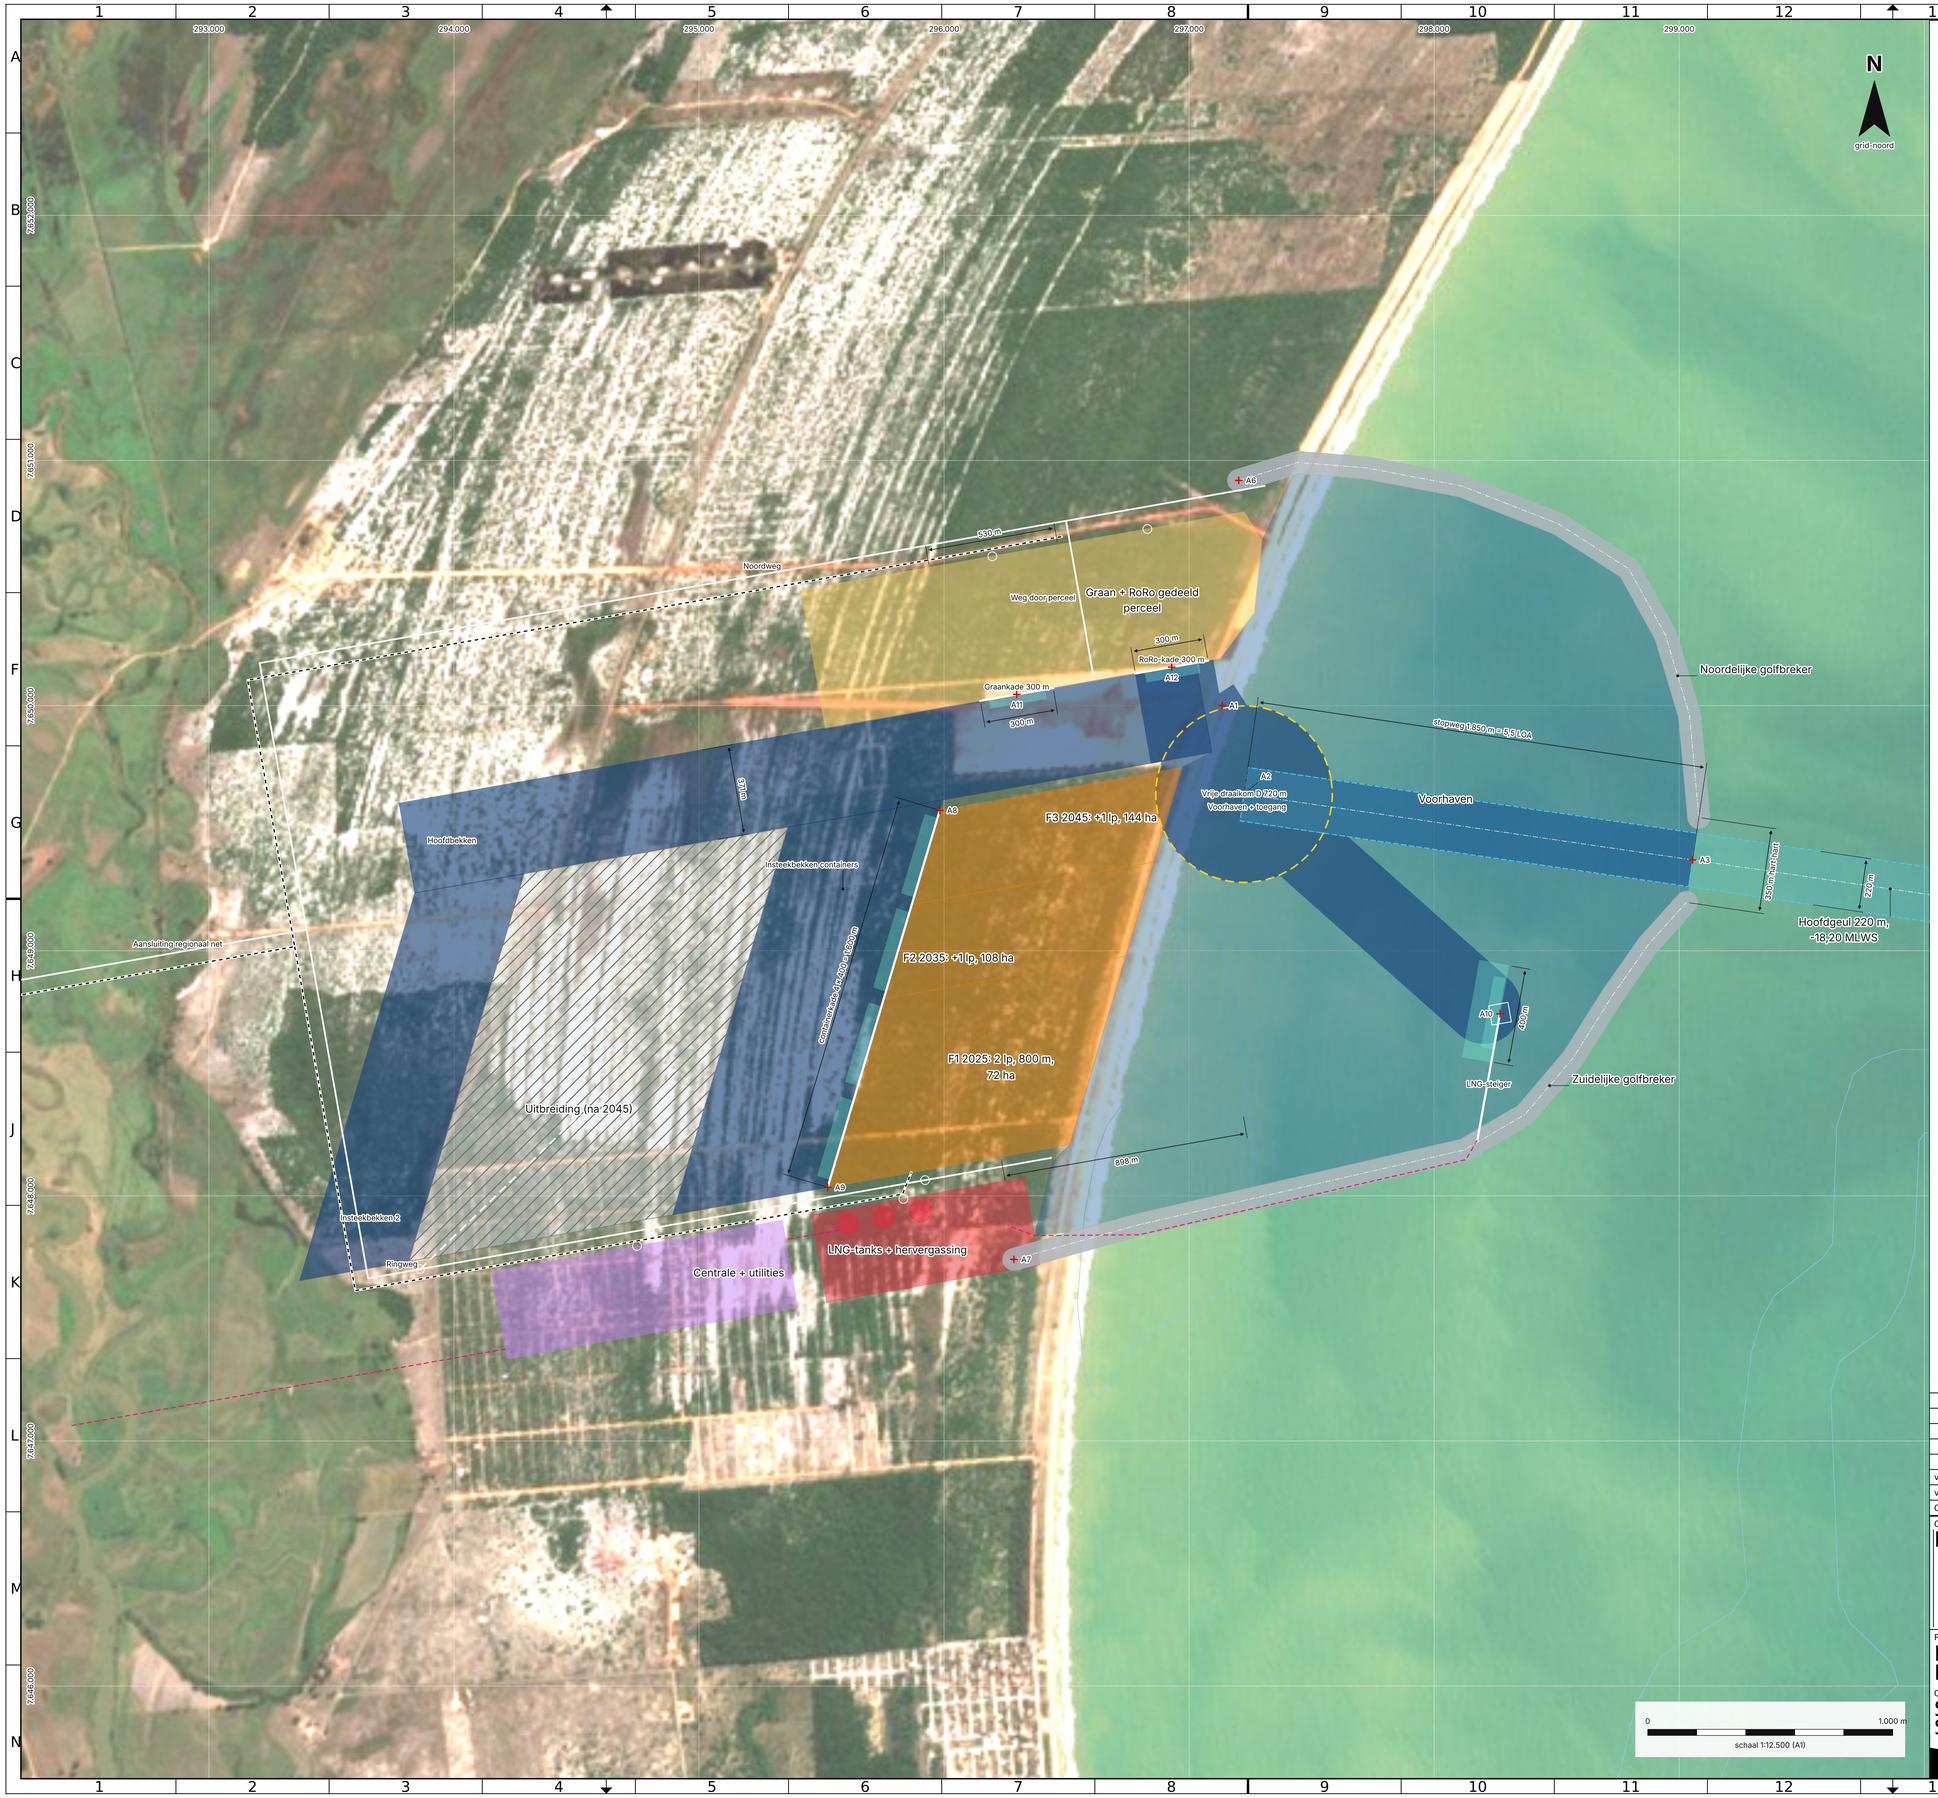

LEGENDA

- Waterlijn 3-7-2026 (NDWI, geen MLWS-lijn)
- Zoekgebied locatie B (indicatief)
- Voorhaven binnen de dammen (strandwal ontgraven)
- Gebaggerd tot -18,20 m MLWS (voorlopig)
- Geul 220 m bodembreedte
- Vrije draaikom D = 720 m
- Havenmond vrij 350 m
- Golfbreker (footprint 90 m, voorlopig)
- Kade / steiger
- Scheepsenveloppe aan ligplaats
- Containerterminal
- Graanterminal
- LNG-steiger, tanks en hervergassing
- Centrale + utilities (reservering)
- Reserveterrein / latere uitbreiding
- Hoofdweg + terminalinritten
- Spoor
- LNG/gasleiding, koelwater (indicatief)
- Ontwerpankerpunt (E/N in maatstaat)
- Dieptelijn t.o.v. MLWS (GEBCO 2026, indicatief)

Hoofdmaten (gemeten in tekening)
Geul bodembreedte 220 m, bodem -18,20 m MLWS (voorlopig)
Geul buiten de mond: 35.500 m (voorlopig)
Havenmond vrij tussen dammen: 260 m
Draaikom D 720 m; vrij van schepen 167 m
Stopweg mond-draaikom 1.850 m = 5,5 LOA
Containerkade 802 / 1.203 / 1.604 m
Containerterrein 72,0 / 108,0 / 144,0 ha
Graan 103,8 ha, RoRo 103,8 ha, kades 300 m
LNG-zone 31,9 ha; centrale (reservering) 43,5 ha
Vrije breedte binnenbekken 334 m
Fasen (globaal)
F1 = zuideinde containervinger, F2/F3 richting hoofdbekken (zie DO)

Algemene gegevens
Stelsel: SIRGAS 2000 / UTM zone 24S (EPSG:31984), eenheid m
Hoogte: m t.o.v. MLWS (voorlopig; MLWS = MSL - 0,7 m)
Luchtfoto: Copernicus Sentinel-2 L2A, 03-07-2026, 10 m
Bathymetrie: GEBCO 2026 + Copernicus DEM; geen peiling
Atelier De Haven A, NHL Stenden | 22-10-2026 | schaal 1:12.500

	07	
	06	
	05	
	04	
	03	
v4.1: NHL-template, teksten zonder overlap, rustiger tekenbeeld	02	22-10-2026
v4.0: schetsontwerp op de Porto Central-render met bespreekpunten	01	22-10-2026
Opmerkingen:	Versie:	Datum:


Opdrachtgever: NHL Stenden

Get:	Formaat:	Projectnummer:
Groep 1	A1	Groep 1
Gec:	Schaal:	Tekeningnummer:
-	1:12.500	HAVEN-SO-02
Vrijg:	Bladnummer:	Status: Versie:
-	2 van 3	SO 4.1

Projectnaam:
Havenontwerp Porto Central Presidente Kennedy (ES), Brazilië

Omschrijving:
SO-02 Havenindeling Schetsontwerp (SO)

Bureau Schmidt
ingenieurs en adviseurs

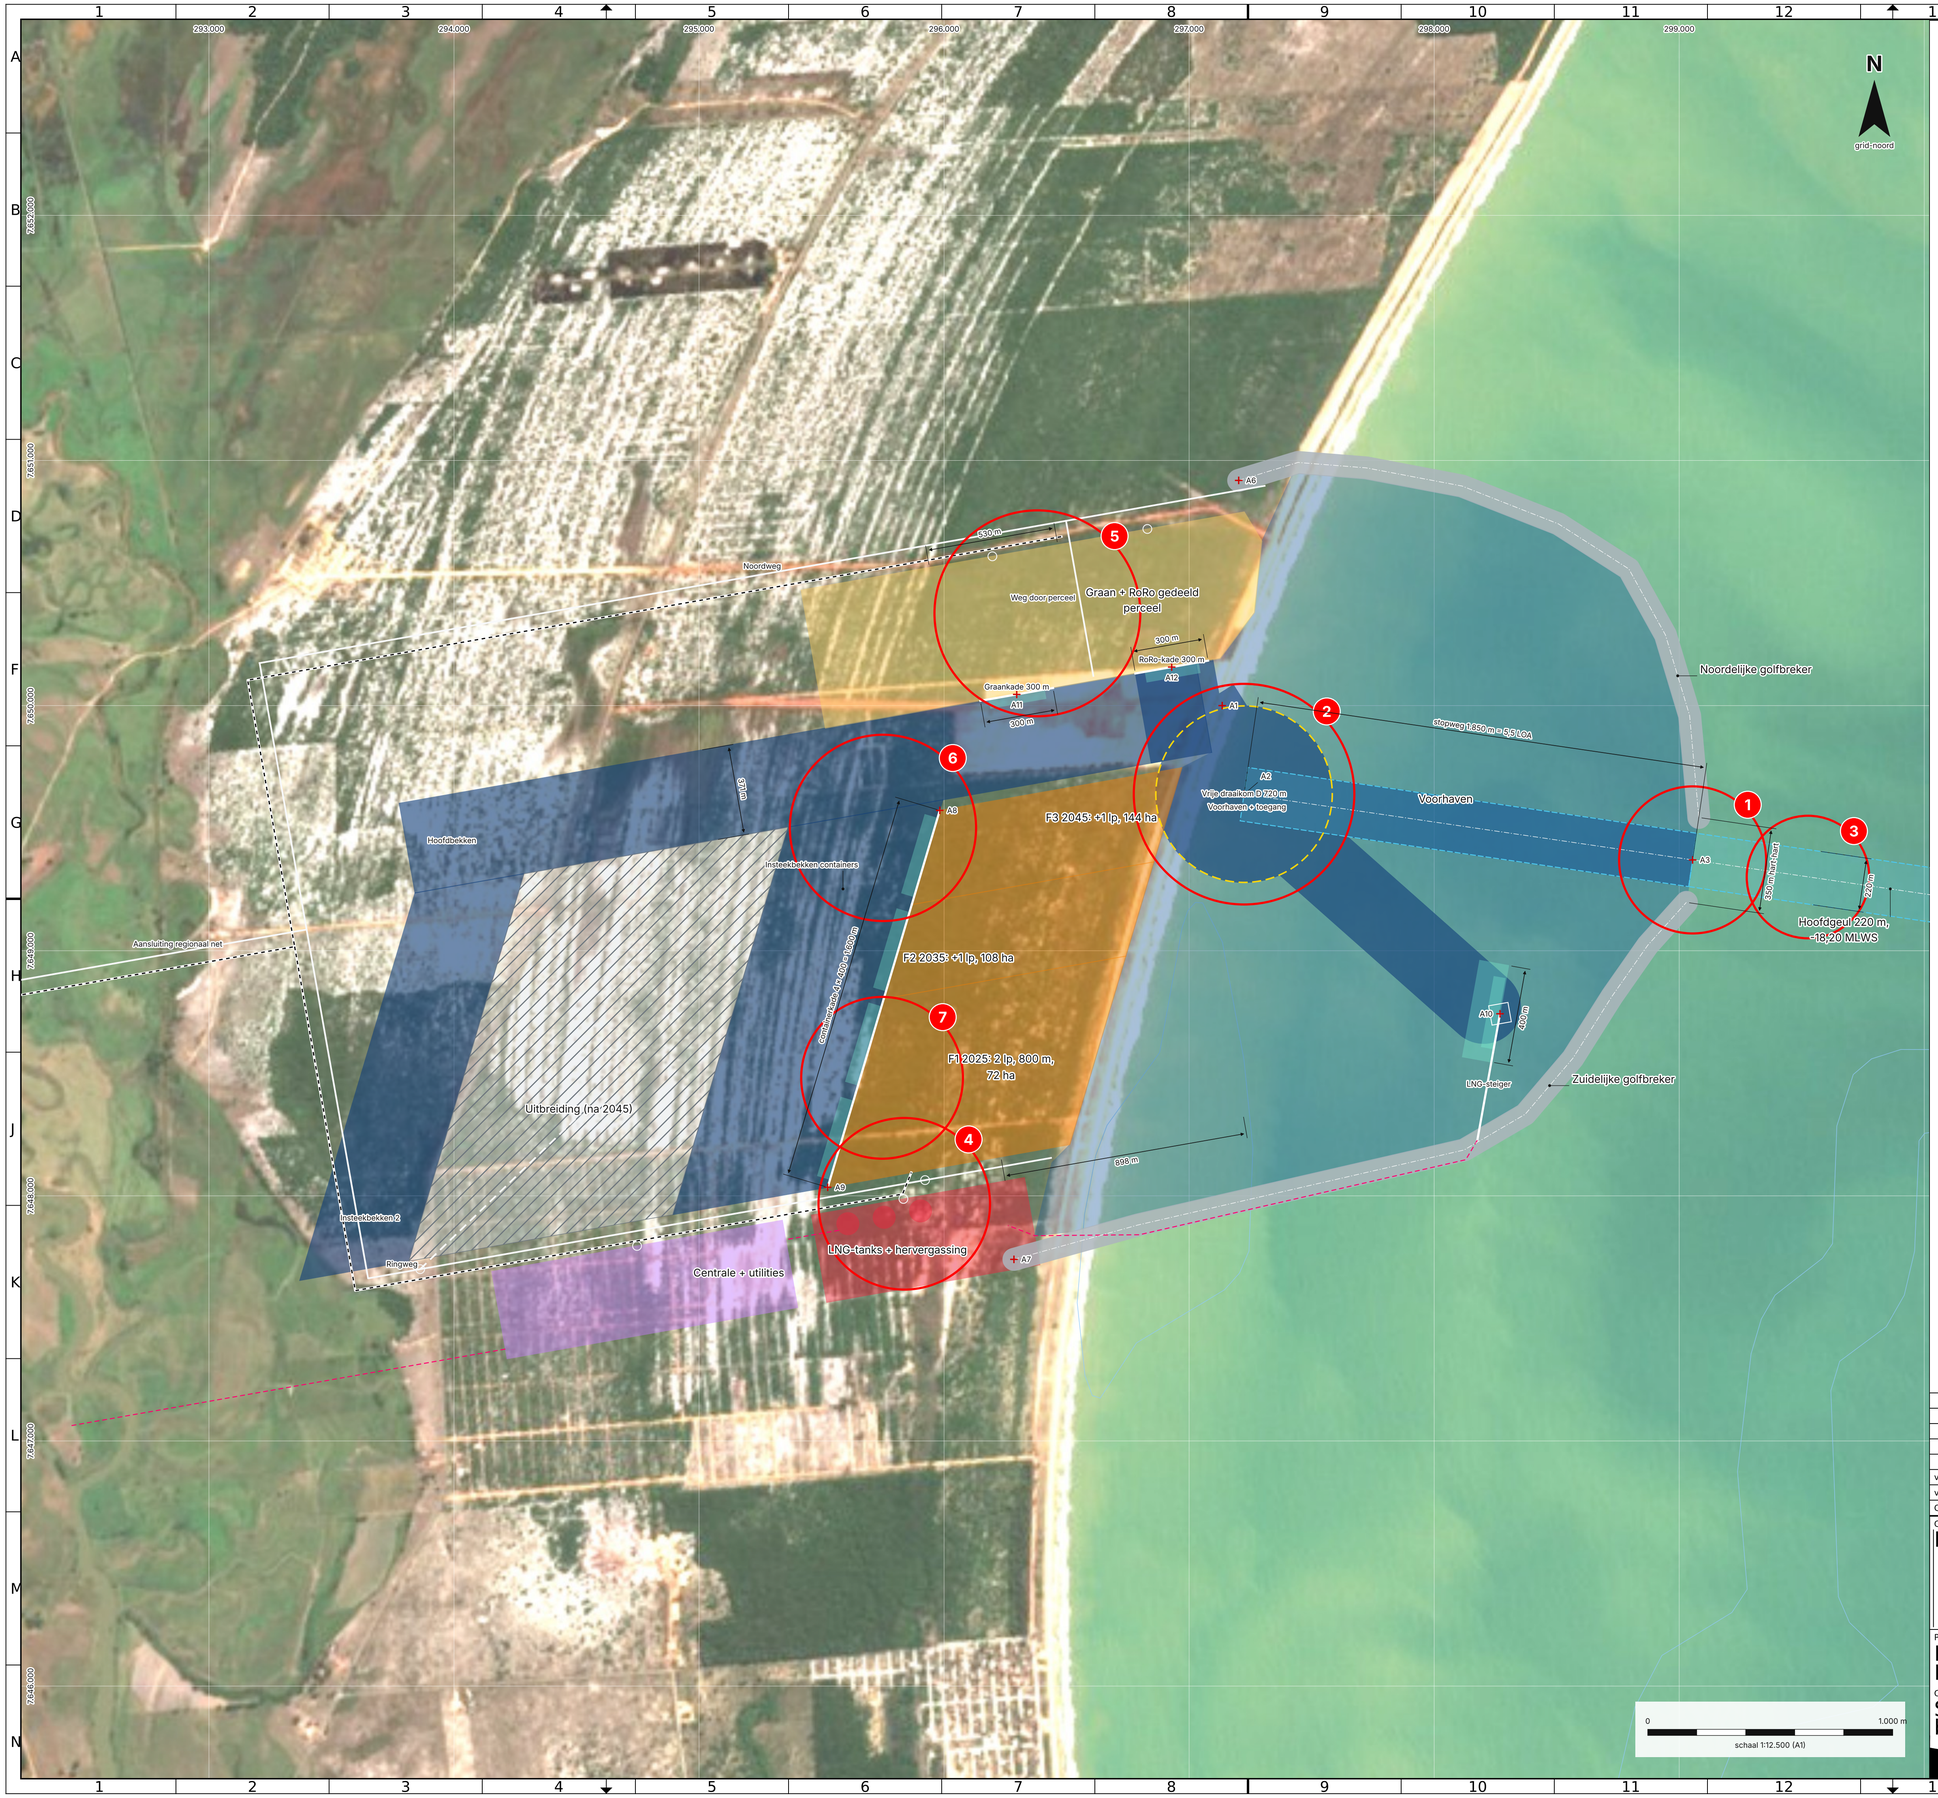

LEGENDA

- Waterlijn 3-7-2026 (NDWI, geen MLWS-lijn)
- Zoekgebied locatie B (indicatief)
- Voorhaven binnen de dammen (strandwal ontgraven)
- Gebaggerd tot -18,20 m MLWS (voorlopig)
- Geul 220 m bodembreedte
- Vrije draaikom D = 720 m
- Havenmond vrij 350 m
- Golfbreker (footprint 90 m, voorlopig)
- Kade / steiger
- Scheepsenveloppe aan ligplaats
- Containerterminal
- Graanterminal
- LNG-steiger, tanks en hervergassing
- Centrale + utilities (reservering)
- Reserveterrein / latere uitbreiding
- Hoofdweg + terminalinritten
- Spoor
- LNG/gasleiding, koelwater (indicatief)
- Ontwerpankerpunt (E/N in maatstaat)
- Dieptelijn t.o.v. MLWS (GEBCO 2026, indicatief)

Bespreekpunten SO (zie rode markering)

1. Havenmond 260 m vrij tussen dammen (350 m hart-hart gemeten)
2. Draaikom overlapt de containervinger (1,5 ha)
3. Geen sleepbootkoppelpunt; geul knikt 15 gr op 2,2 km buiten de mond
4. LNG-tanks op 116 m van het containerterrein
5. Graan + RoRo op één perceel aan de noordkade; weg kruist het terrein
6. Containerschip 334 m moet 63 gr draaien van hoofdbekken (370 m) naar insteek: niet haalbaar
7. Containers F1 aan het zuideinde; geen draaikom binnen voor graan/RoRo; alles in F1 baggeren

Algemene gegevens

Stelsel: SIRGAS 2000 / UTM zone 24S (EPSG:31984), eenheid m
Hoogte: m t.o.v. MLWS (voorlopig; MLWS = MSL - 0,7 m)
Luchtfoto: Copernicus Sentinel-2 L2A, 03-07-2026, 10 m
Bathymetrie: GEBCO 2026 + Copernicus DEM; geen peiling
Atelier De Haven A, NHL Stenden | 22-10-2026 | schaal 1:12.500

	07	
	06	
	05	
	04	
	03	
v4.1: NHL-template, teksten zonder overlap, rustiger tekenbeeld	02	22-10-2026
v4.0: schetsontwerp op de Porto Central-render met bespreekpunten	01	22-10-2026
Opmerkingen:	Versie:	Datum:

Opdrachtgever: NHL Stenden

Get:	Formaat:	Projectnummer:
Groep 1	A1	Groep 1
Gec:	Schaal:	Tekeningnummer:
-	1:12.500	HAVEN-SO-03
Vrijg:	Bladnummer:	Status: Versie:
-	3 van 3	SO 4.1

Projectnaam:
Havenontwerp Porto Central Presidente Kennedy (ES), Brazilië

Omschrijving:
SO-03 Bespreking SO - bespreekpunten

Bureau Schmidt
ingenieurs en adviseurs