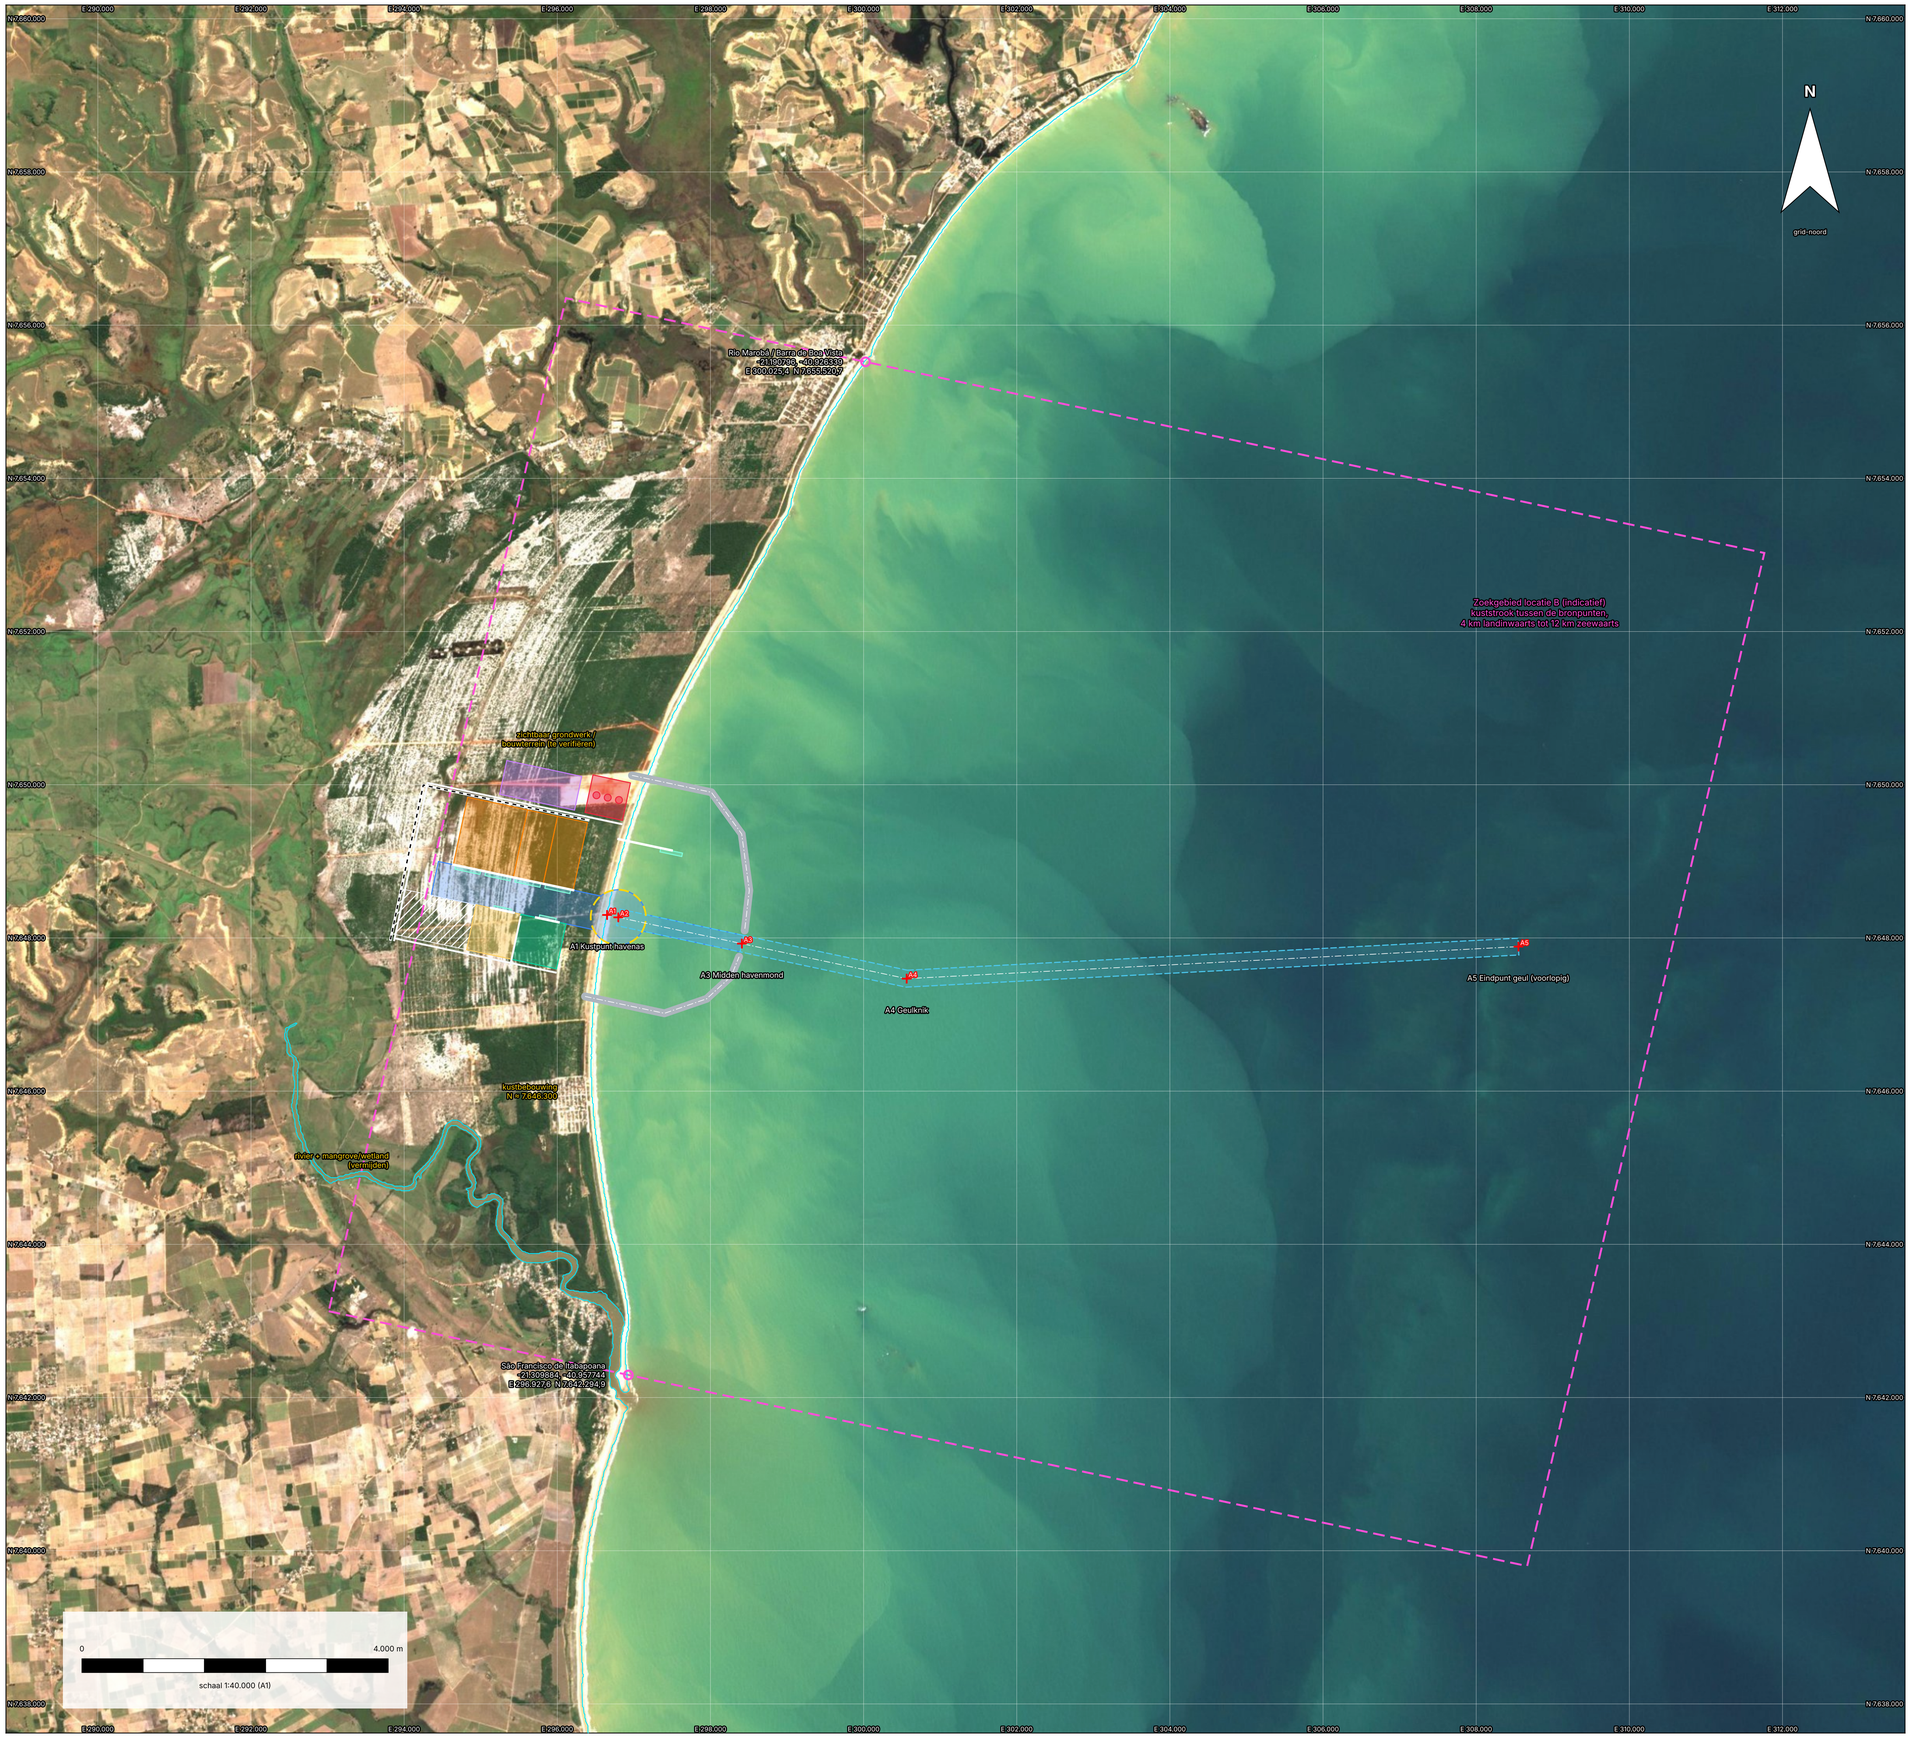


LEGENDA

- Waterlijn 3-7-2026 (NDWI, geen MLWS-lijn)
- Zoekgebied locatie B (indicatief)
- Gebaggerd tot -18,20 m MLWS (voorlopig)
- Geul 220 m bodembreedte
- Vrije draaikom D = 720 m
- Havenmond vrij 350 m
- Golfbreker (footprint 90 m, voorlopig)
- Kade / steiger
- Scheepsenveloppe aan ligplaats
- Containerterminal
- Graanterminal
- RoRo / voertuigenterminal
- LNG-steiger, tanks en hervergassing
- Centrale + utilities (reservering)
- Havendiensten, sleepboten, loodsen
- Reserveterrein / latere uitbreiding
- Hoofdweg + terminalinritten
- Spoor
- LNG/gasleiding, koelwater (indicatief)
- Fasegrens 2025 / 2035 / 2045
- Ontwerpankerpunt (E/N in maatstaat)


Gekozen havenligging

Havenas haaks op de kust: azimut 102 gr (kust 11.8 gr).
A1 kustpunt: E 296.650,0 N 7.648.300,0
= -21.255626, -40.959701 (WGS84)
Tussen kustbebouwing (zuid) en grondwerk (noord);
rivier/wetland in het zuidwesten vermeden;
rechte, open kust met bereikbaar achterland.

Georeferentiecontrole

GSHHS-kust vs. S2-waterlijn: gem. 14 m, sd 66 m
(15 profielen, N 7.642-7.656 km)
Bekende afstand bronpunten: 13.582,4 m geodetisch,
13.583,8 m in grid (k = 1.00010)
Noordrichting: convergentie 0.70 gr

Project	Havenontwerp Porto Central-referentie, Groep 1
Module	Atelier De Haven A | NHL Stenden Civiele Techniek
Bladnaam	**Overzicht zoekgebied en havenligging**
Status	**SCHETSONTWERP (SO)**
Blad / versie	SO-01 | versie 1.0 | 22-10-2026
Schaal	1:40.000 op A1 (841 × 594 mm)
Stelsel	SIRGAS 2000 / UTM zone 24S EPSG:31984 eenheid m
Hoogtedatum	diepten in m t.o.v. MLWS, voorlopig; MLWS-DHN te verifiëren
Kaartbron	Copernicus Sentinel-2 L2A (ESA), 03-07-2026, 10 m
	tegels 24KTB/24KUB, AWS Open Data COG; geraadpleegd 22-10-2026
Kustlijn	waterlijn 03-07-2026 uit NDWI (geen MLWS-lijn)

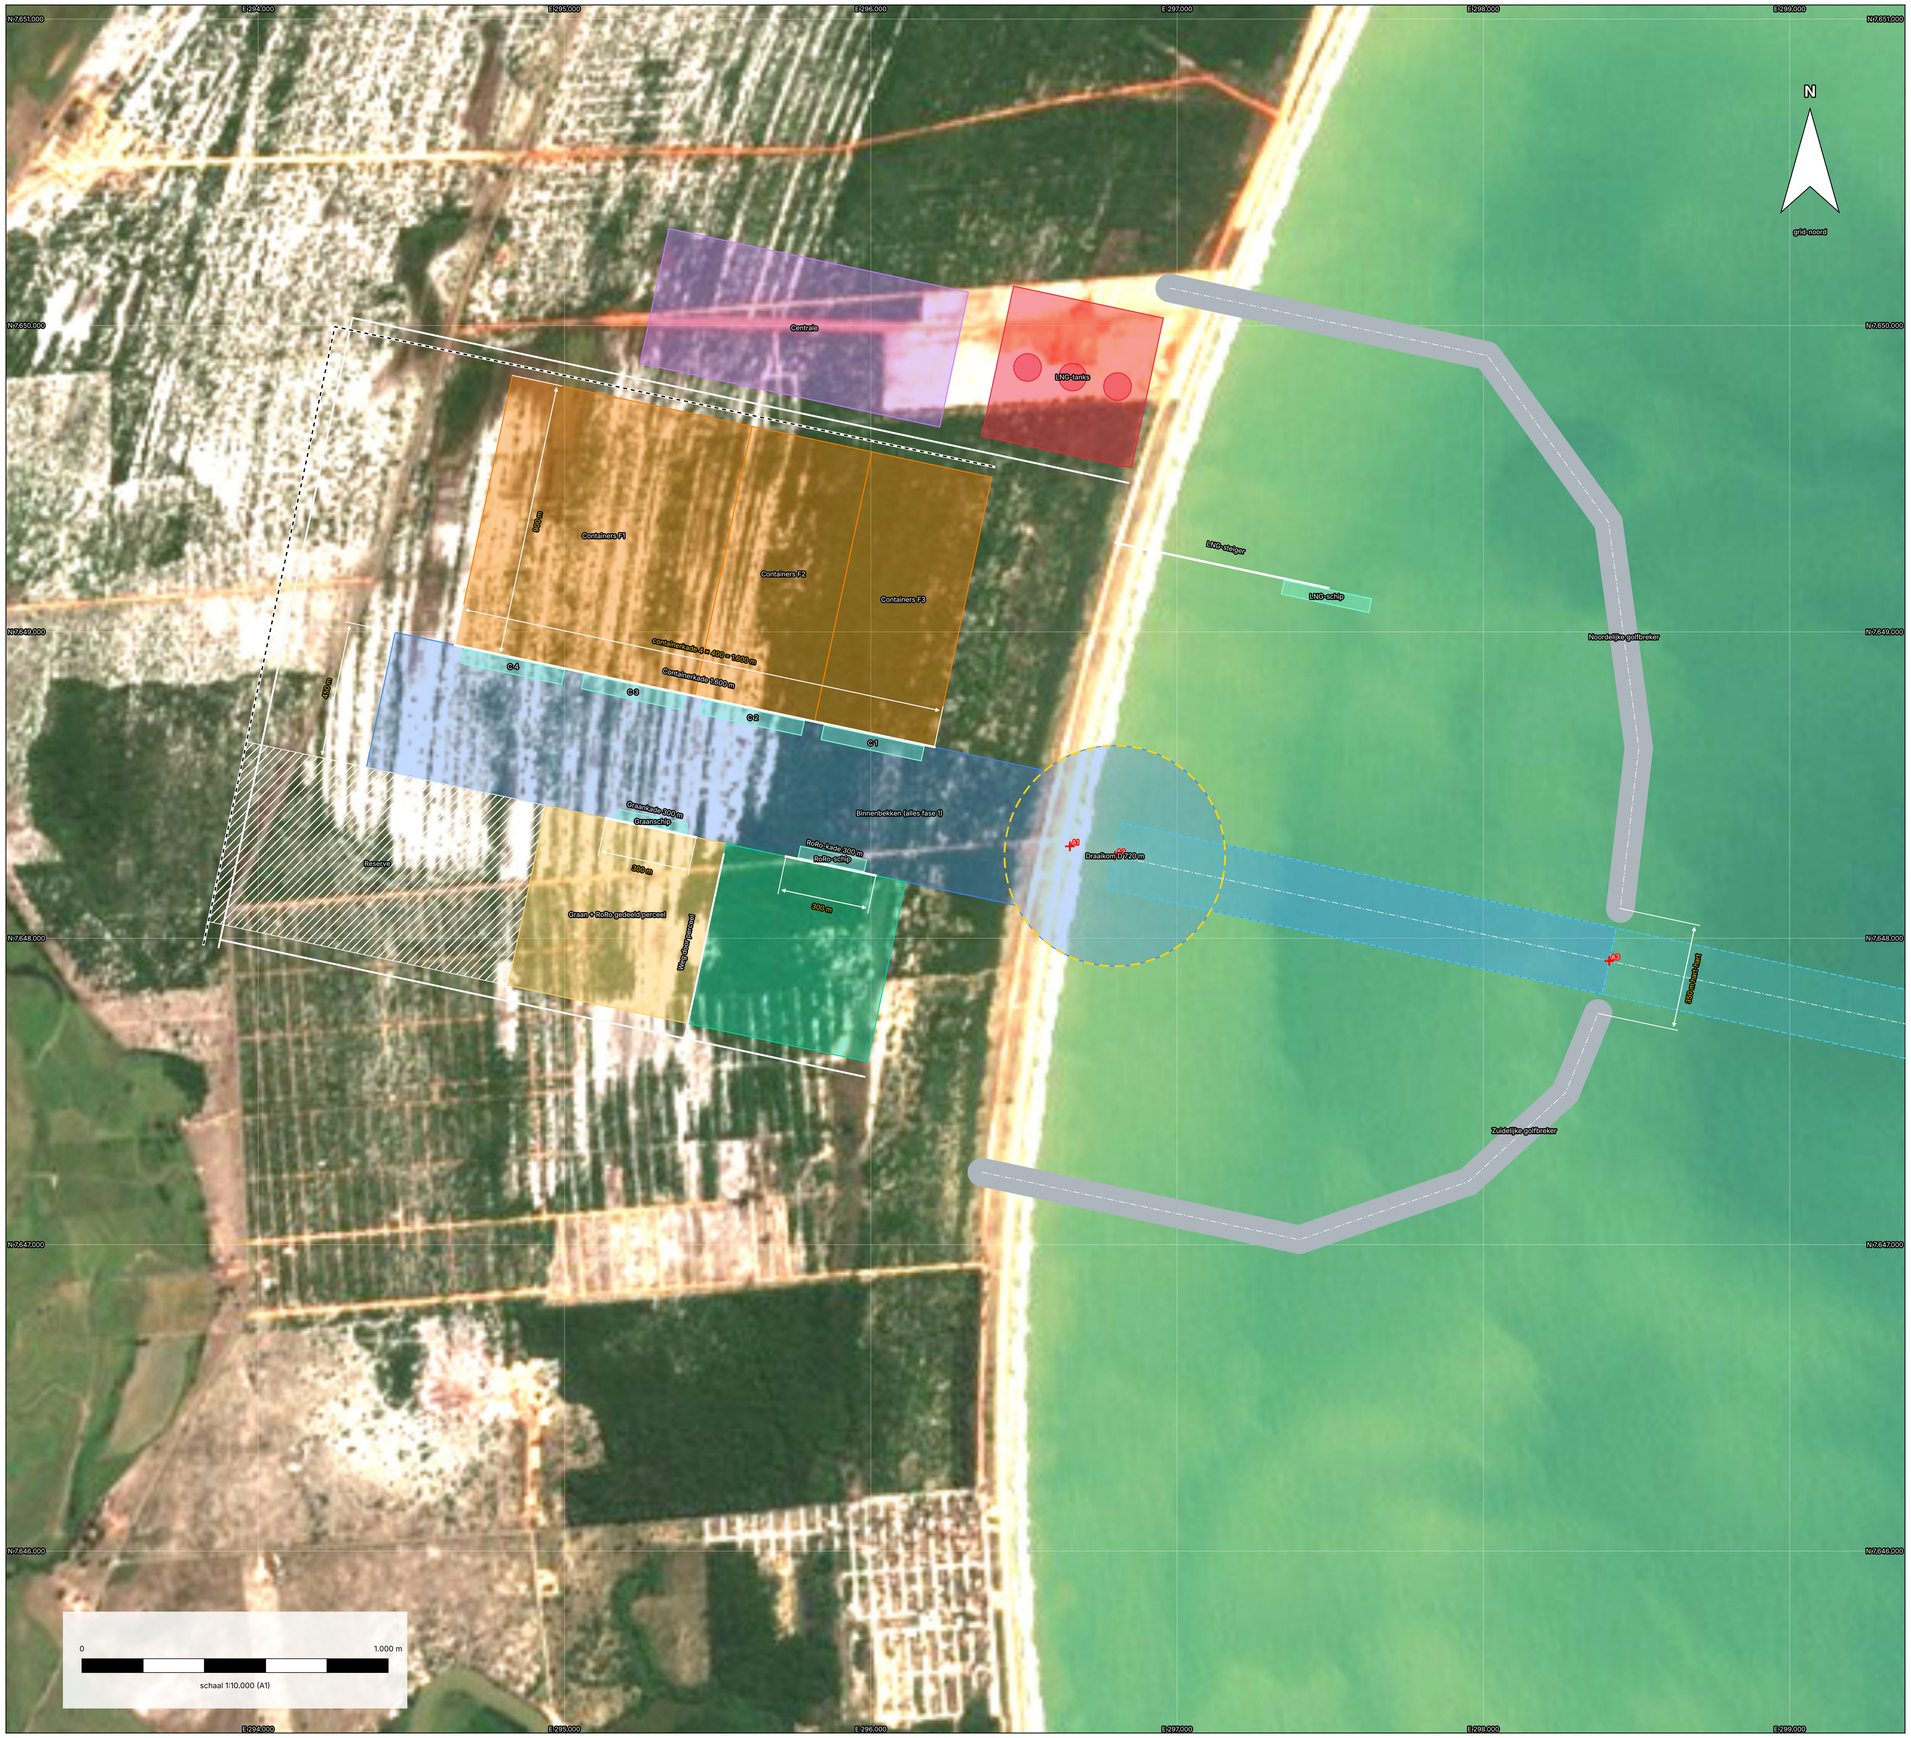


LEGENDA

- Waterlijn 3-7-2026 (NDWI, geen MLWS-lijn)
- Zoekgebied locatie B (indicatief)
- Gebaggerd tot -18,20 m MLWS (voorlopig)
- Geul 220 m bodembreedte
- Vrije draaikom D = 720 m
- Havenmond vrij 350 m
- Golfbreker (footprint 90 m, voorlopig)
- Kade / steiger
- Scheepsenveloppe aan ligplaats
- Containerterminal
- Graanterminal
- RoRo / voertuigenterminal
- LNG-steiger, tanks en hervergassing
- Centrale + utilities (reservering)
- Havendiensten, sleepboten, loodsen
- Reserveterrein / latere uitbreiding
- Hoofdweg + terminalinritten
- Spoor
- LNG/gasleiding, koelwater (indicatief)
- Fasegrens 2025 / 2035 / 2045
- Ontwerpankerpunt (E/N in maatstaat)

Hoofdmaten (gemeten in tekening)
Geul bodembreedte 220 m, bodem -18,20 m MLWS (voorlopig)
Geul buiten de mond: 10.200 m (voorlopig)
Havenmond vrij tussen dammen: 260 m
Draaikom D 720 m; vrij van schepen 344 m
Stopweg mond-draaikom 1.650 m = 4,9 LOA
Containerkade 800 / 1.200 / 1.600 m
Containerterrein 72,0 / 108,0 / 144,0 ha
Graan 36,0 ha, RoRo 36,0 ha, kades 300 m
LNG-zone 25,0 ha; centrale (reservering) 45,0 ha
Vrije breedte binnenbekken 354 m
Fasen (globaal)
F1 = landzijde, F2/F3 richting ingang (zie DO voor herziening)

Project	Havenontwerp Porto Central-referentie, Groep 1
Module	Atelier De Haven A | NHL Stenden Civiele Techniek
Bladnaam	**Havenindeling**
Status	**SCHETSONTWERP (SO)**
Blad / versie	SO-02 | versie 1.0 | 22-10-2026
Schaal	1:10.000 op A1 (841 × 594 mm)
Stelsel	SIRGAS 2000 / UTM zone 24S EPSG:31984 eenheid m
Hoogtedatum	diepten in m t.o.v. MLWS, voorlopig; MLWS-DHN te verifiëren
Kaartbron	Copernicus Sentinel-2 L2A (ESA), 03-07-2026, 10 m
	tegels 24KTB/24KUB, AWS Open Data COG; geraadpleegd 22-10-2026
Kustlijn	waterlijn 03-07-2026 uit NDWI (geen MLWS-lijn)

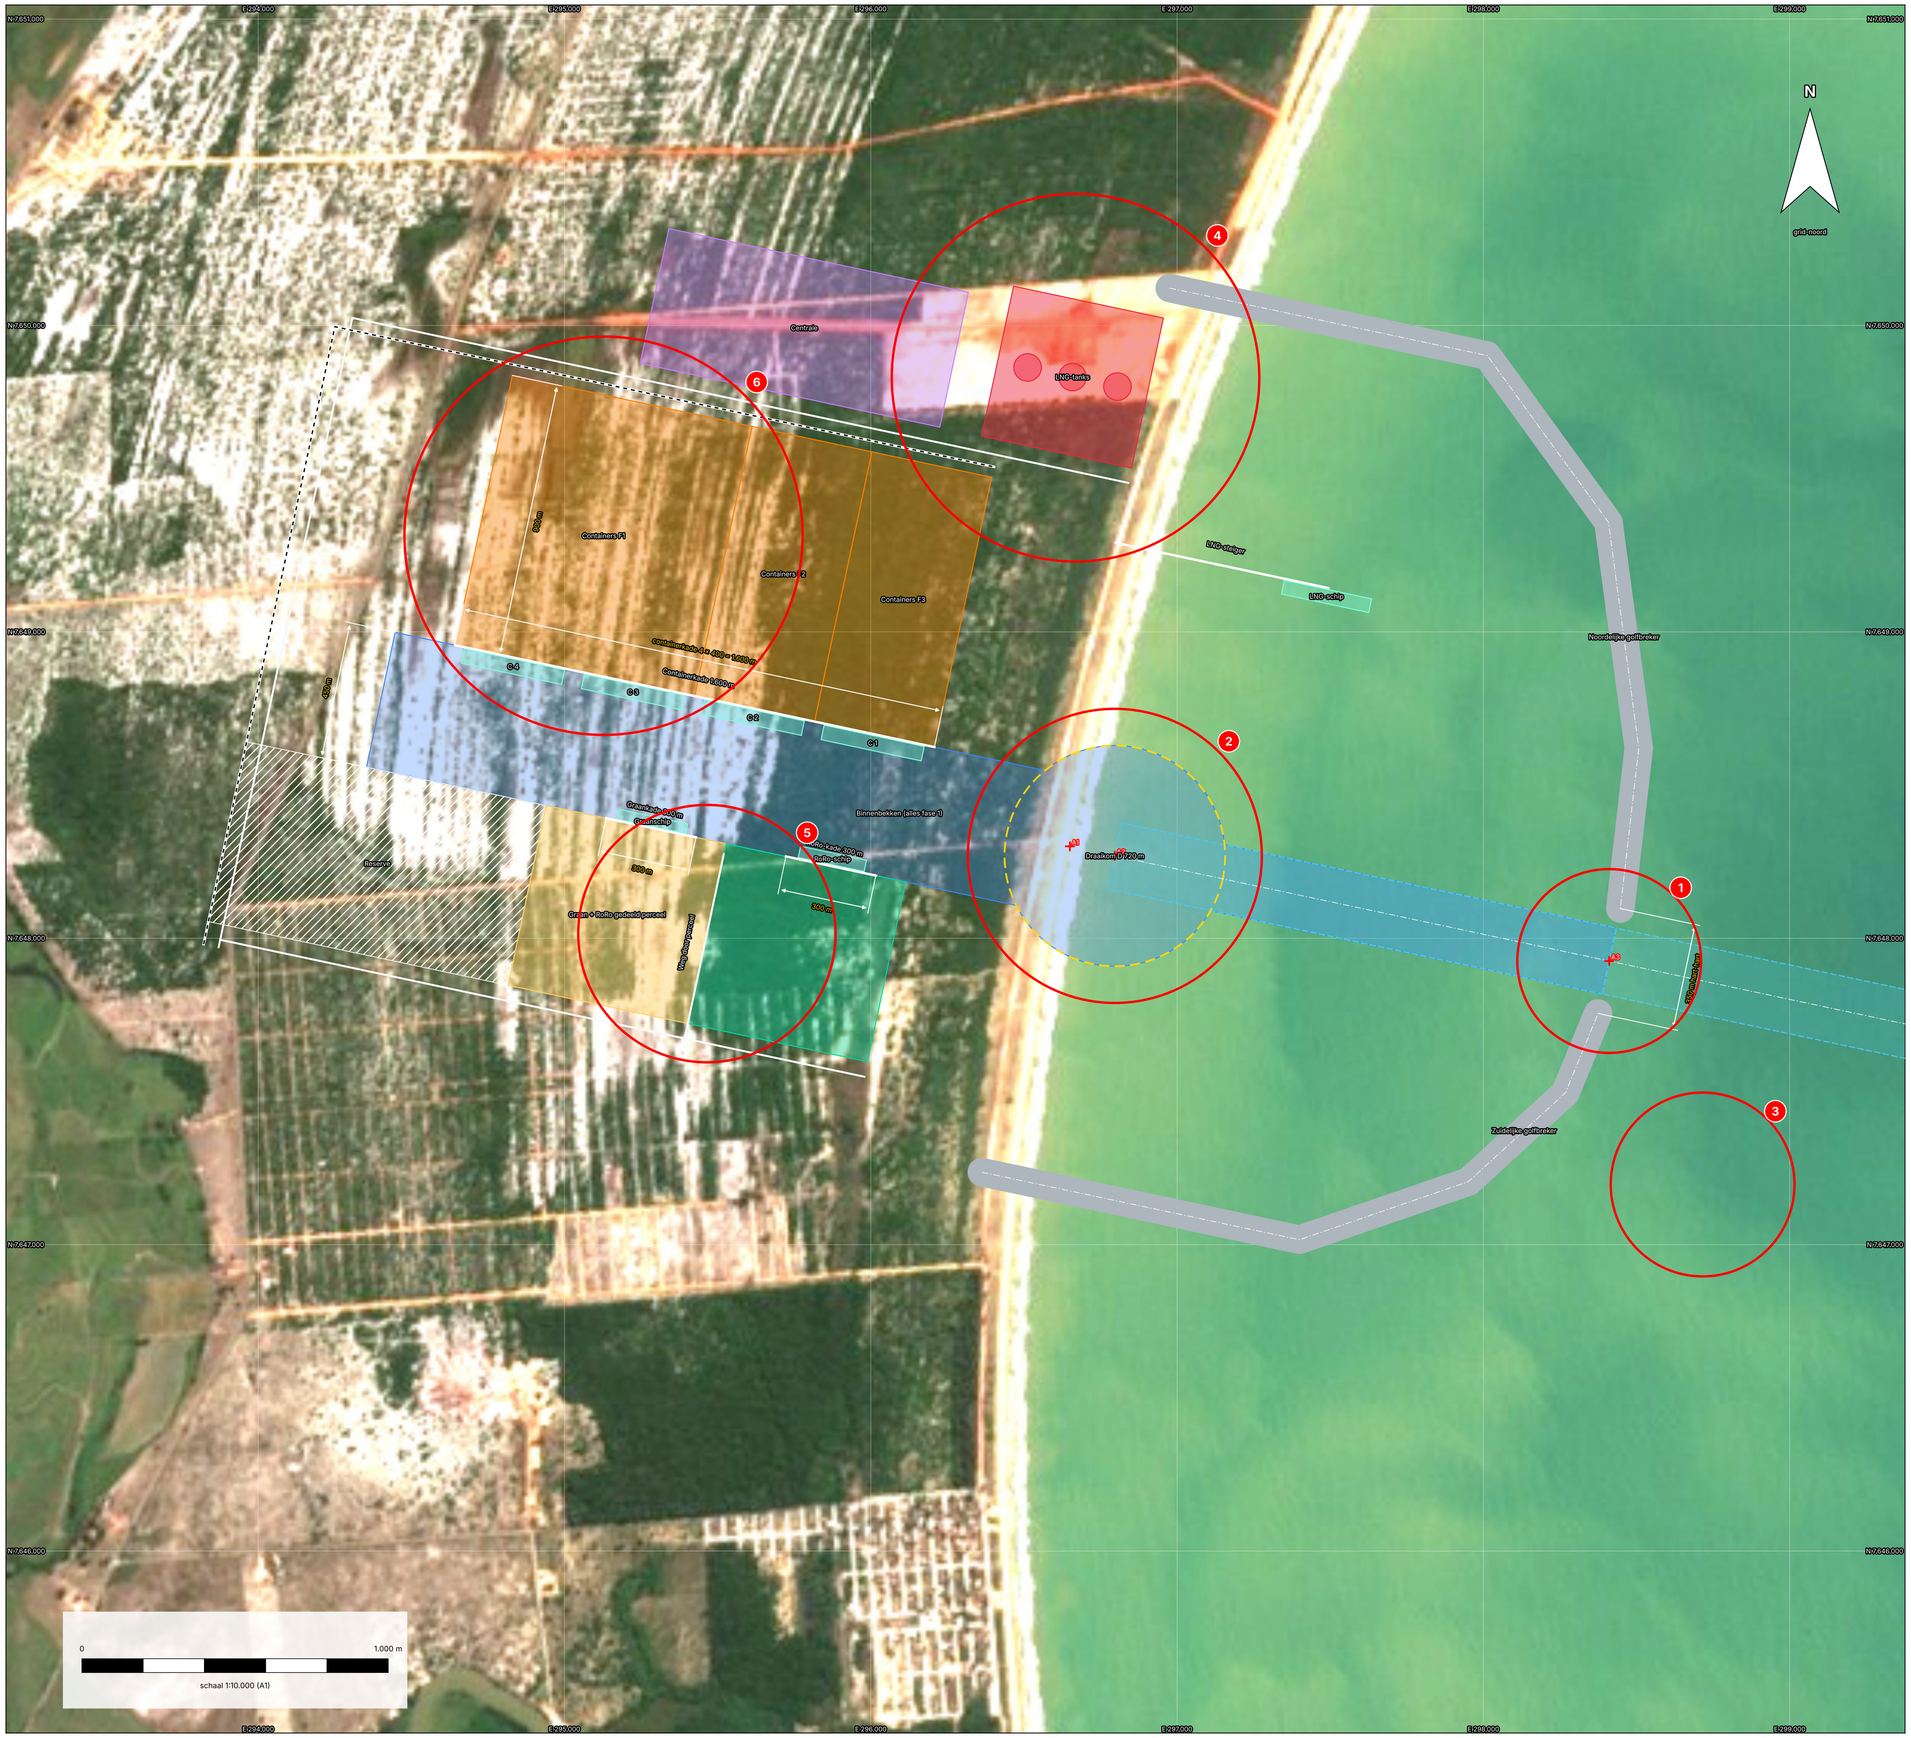

LEGENDA

- Waterlijn 3-7-2026 (NDWI, geen MLWS-lijn)
- Zoekgebied locatie B (indicatief)
- Gebaggerd tot -18,20 m MLWS (voorlopig)
- Geul 220 m bodembreedte
- Vrije draaikom D = 720 m
- Havenmond vrij 350 m
- Golfbreker (footprint 90 m, voorlopig)
- Kade / steiger
- Scheepsenveloppe aan ligplaats
- Containerterminal
- Graanterminal
- RoRo / voertuigenterminal
- LNG-steiger, tanks en hervergassing
- Centrale + utilities (reservering)
- Havendiensten, sleepboten, loodsen
- Reserveterrein / latere uitbreiding
- Hoofdweg + terminalinritten
- Spoor
- LNG/gasleiding, koelwater (indicatief)
- Fasegrens 2025 / 2035 / 2045
- Ontwerpankerpunt (E/N in maatstaat)

Bespreekpunten SO (zie rode markering)

1. Havenmond 260 m vrij tussen dammen (350 m hart-hart gemeten)
2. Draaikom raakt landhoeken (1,6 ha); stopweg 1.650 m < 5 LOA
3. Geen sleepbootkoppelpunt buiten de dammen; geulknik buiten blad
4. LNG en wortel N-dam bij grondwerk N 7.650 km; tanks tegen containeruitbreiding
5. Graan + RoRo op één perceel; weg kruist het terrein
6. Containers F1 aan landeinde: heel bekken in F1 baggeren

Project	Havenontwerp Porto Central-referentie, Groep 1
Module	Atelier De Haven A | NHL Stenden Civiele Techniek
Bladnaam	**Bespreking SO - bespreekpunten**
Status	**SCHETSONTWERP (SO)**
Blad / versie	SO-03 | versie 1.0 | 22-10-2026
Schaal	1:10.000 op A1 (841 × 594 mm)
Stelsel	SIRGAS 2000 / UTM zone 24S EPSG:31984 eenheid m
Hoogtedatum	diepten in m t.o.v. MLWS, voorlopig; MLWS-DHN te verifiëren
Kaartbron	Copernicus Sentinel-2 L2A (ESA), 03-07-2026, 10 m
	tegels 24KTB/24KUB, AWS Open Data COG; geraadpleegd 22-10-2026
Kustlijn	waterlijn 03-07-2026 uit NDWI (geen MLWS-lijn)